

Client : SAUDI GLOBAL PORTS

Project : DAMMAM LOGISTICS ZONE

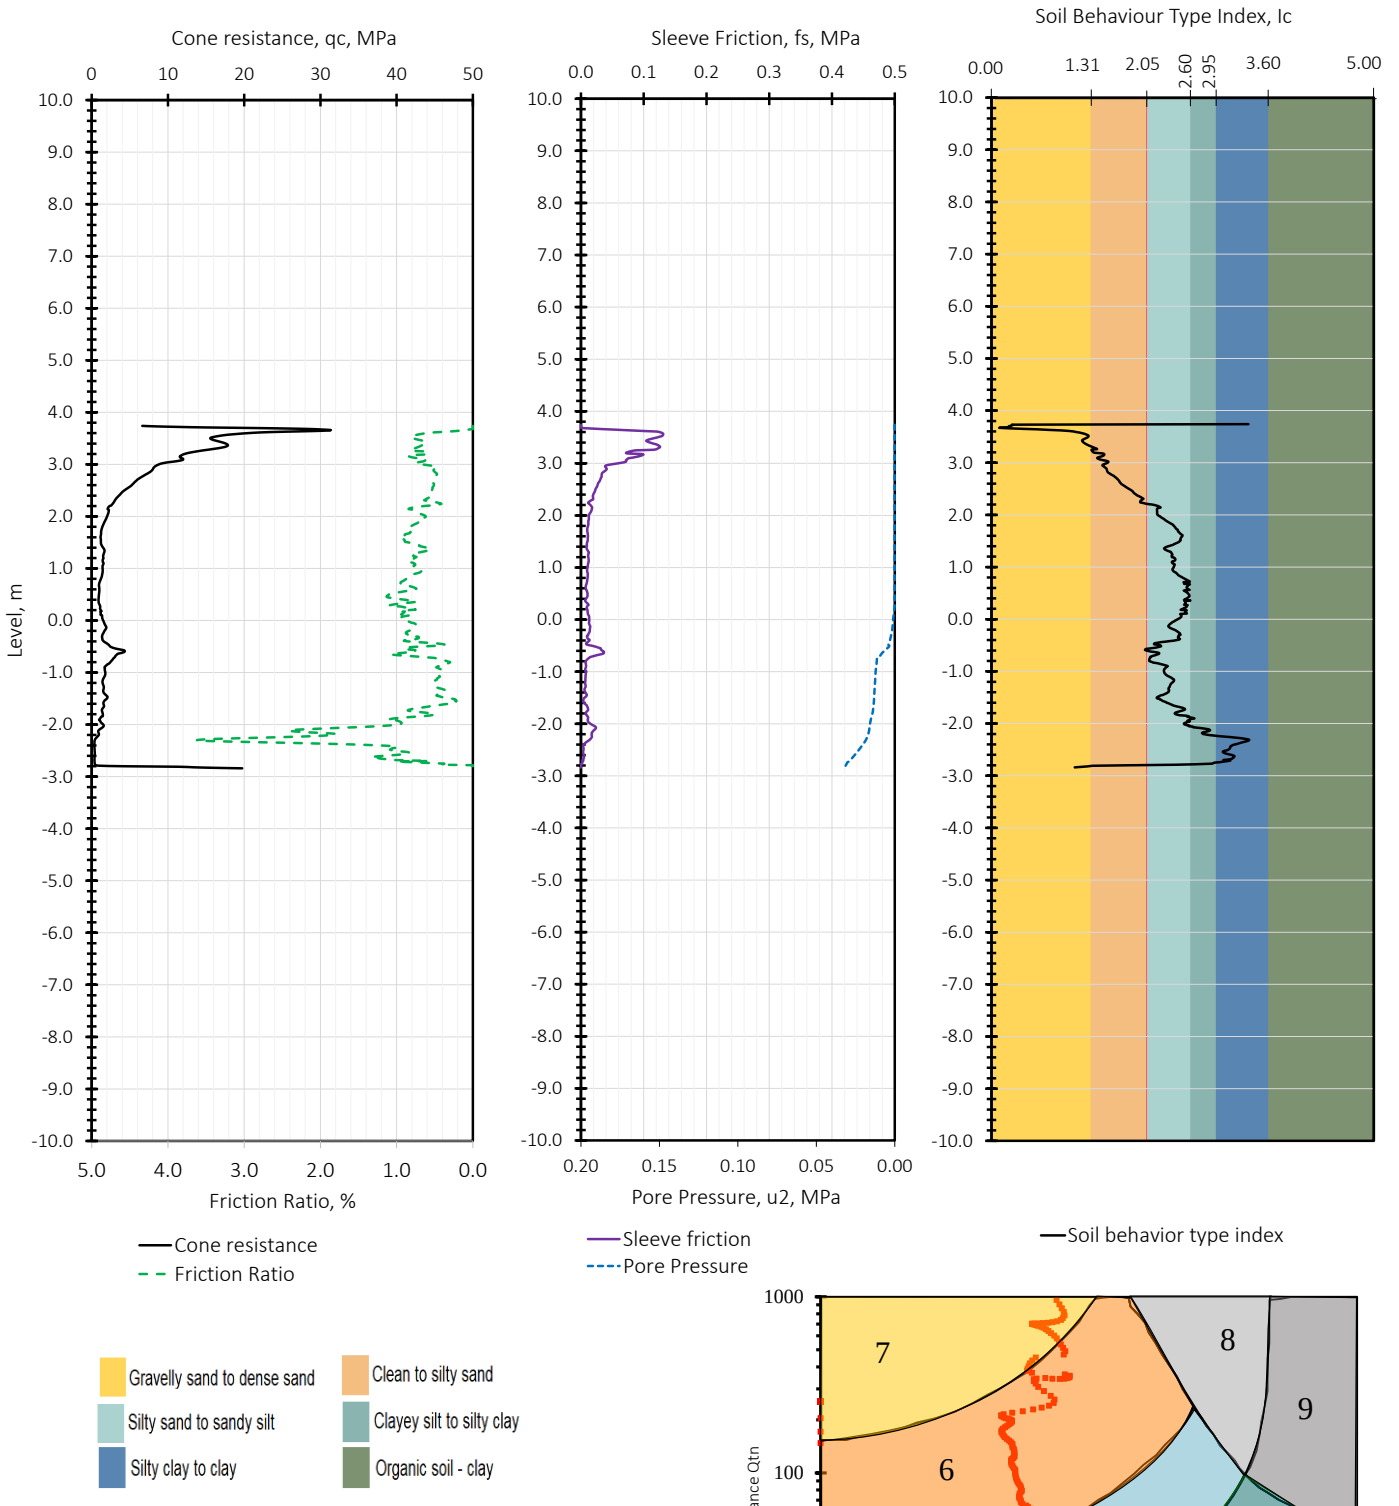

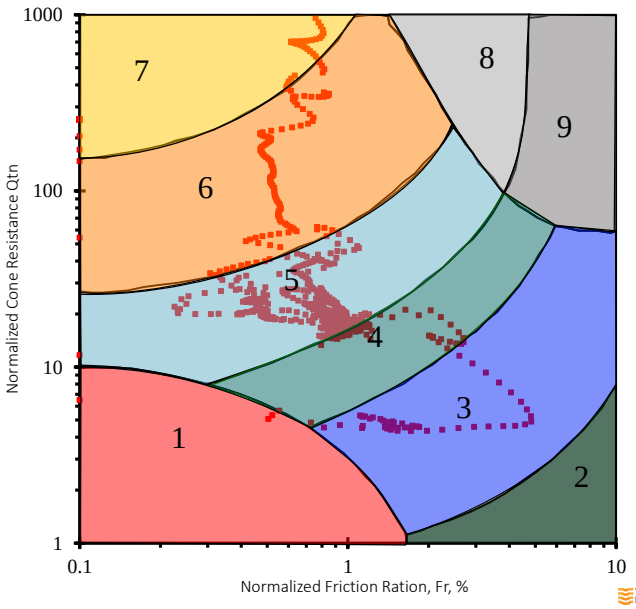

Main Contractor:	CTS GULF	
Test Location:	CPT-A1-B364-100	
Ground Elevation:	3.74	
	Easting	**Northing**
Coordinates:	421214.237	2928221.04
Cone ID:	DP15-CFPTxy.71431	
Test Date	19-Sep-2026	