
Client : SAUDI GLOBAL PORTS

Project : DAMMAM LOGISTICS ZONE

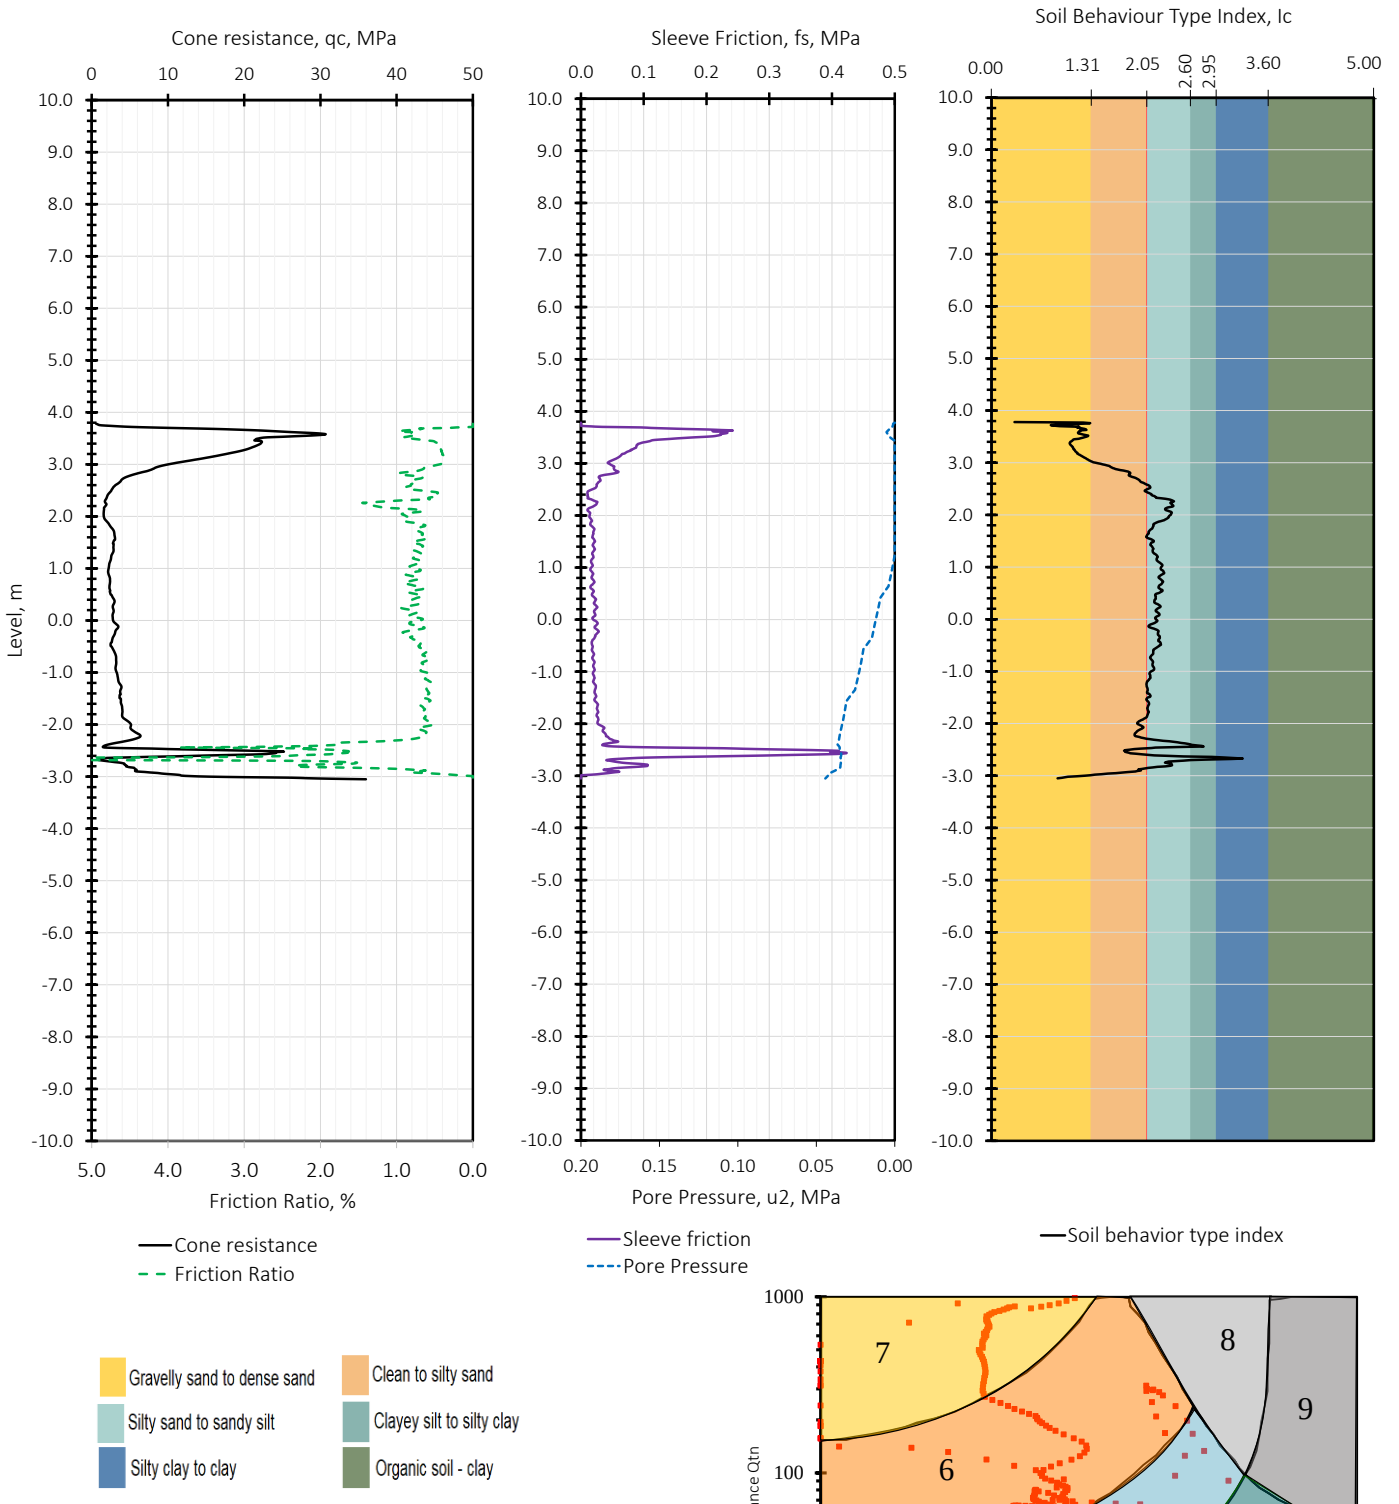

Main Contractor:	CTS GULF	
Test Location:	CPT-A1-B369-100	
Ground Elevation:	3.78	
	Easting	**Northing**
Coordinates:	421123.037	2928091.951
Cone ID:	DP15-CFPTxy.71431	
Test Date	8-Oct-2026	