
**Client : SAUDI GLOBAL PORTS**

**Project : DAMMAM LOGISTICS ZONE**

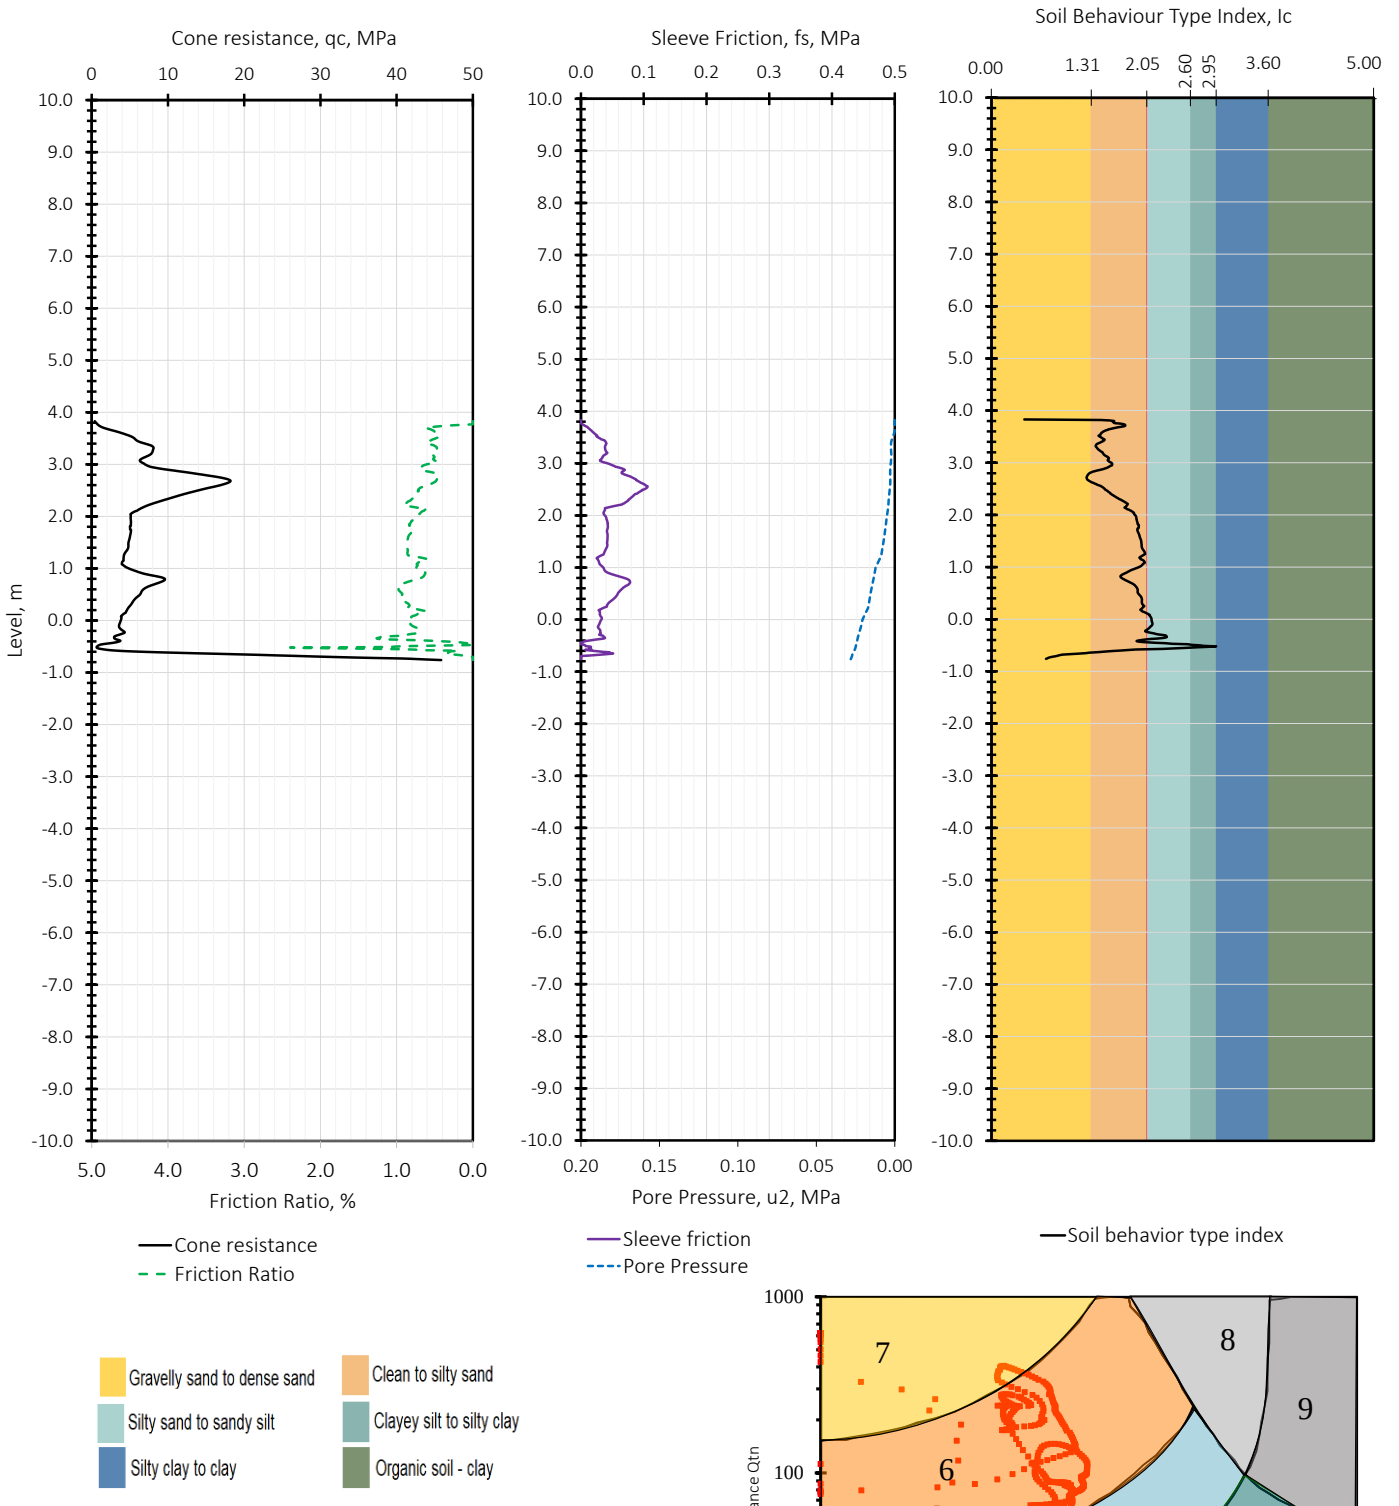


| | | |
|---|---|---|
| **Main Contractor:** | CTS GULF | |
| **Test Location:** | CPT-A1-B38-100 | |
| **Ground Elevation:** | 3.83 | |
| | **Easting** | **Northing** |
| **Coordinates:** | 420540.249 | 2927719.676 |
| **Cone ID:** | DP15-CFPTxy.71424 | |
| **Test Date** | 8-Oct-2026 | |