
Client : SAUDI GLOBAL PORTS

Project : DAMMAM LOGISTICS ZONE

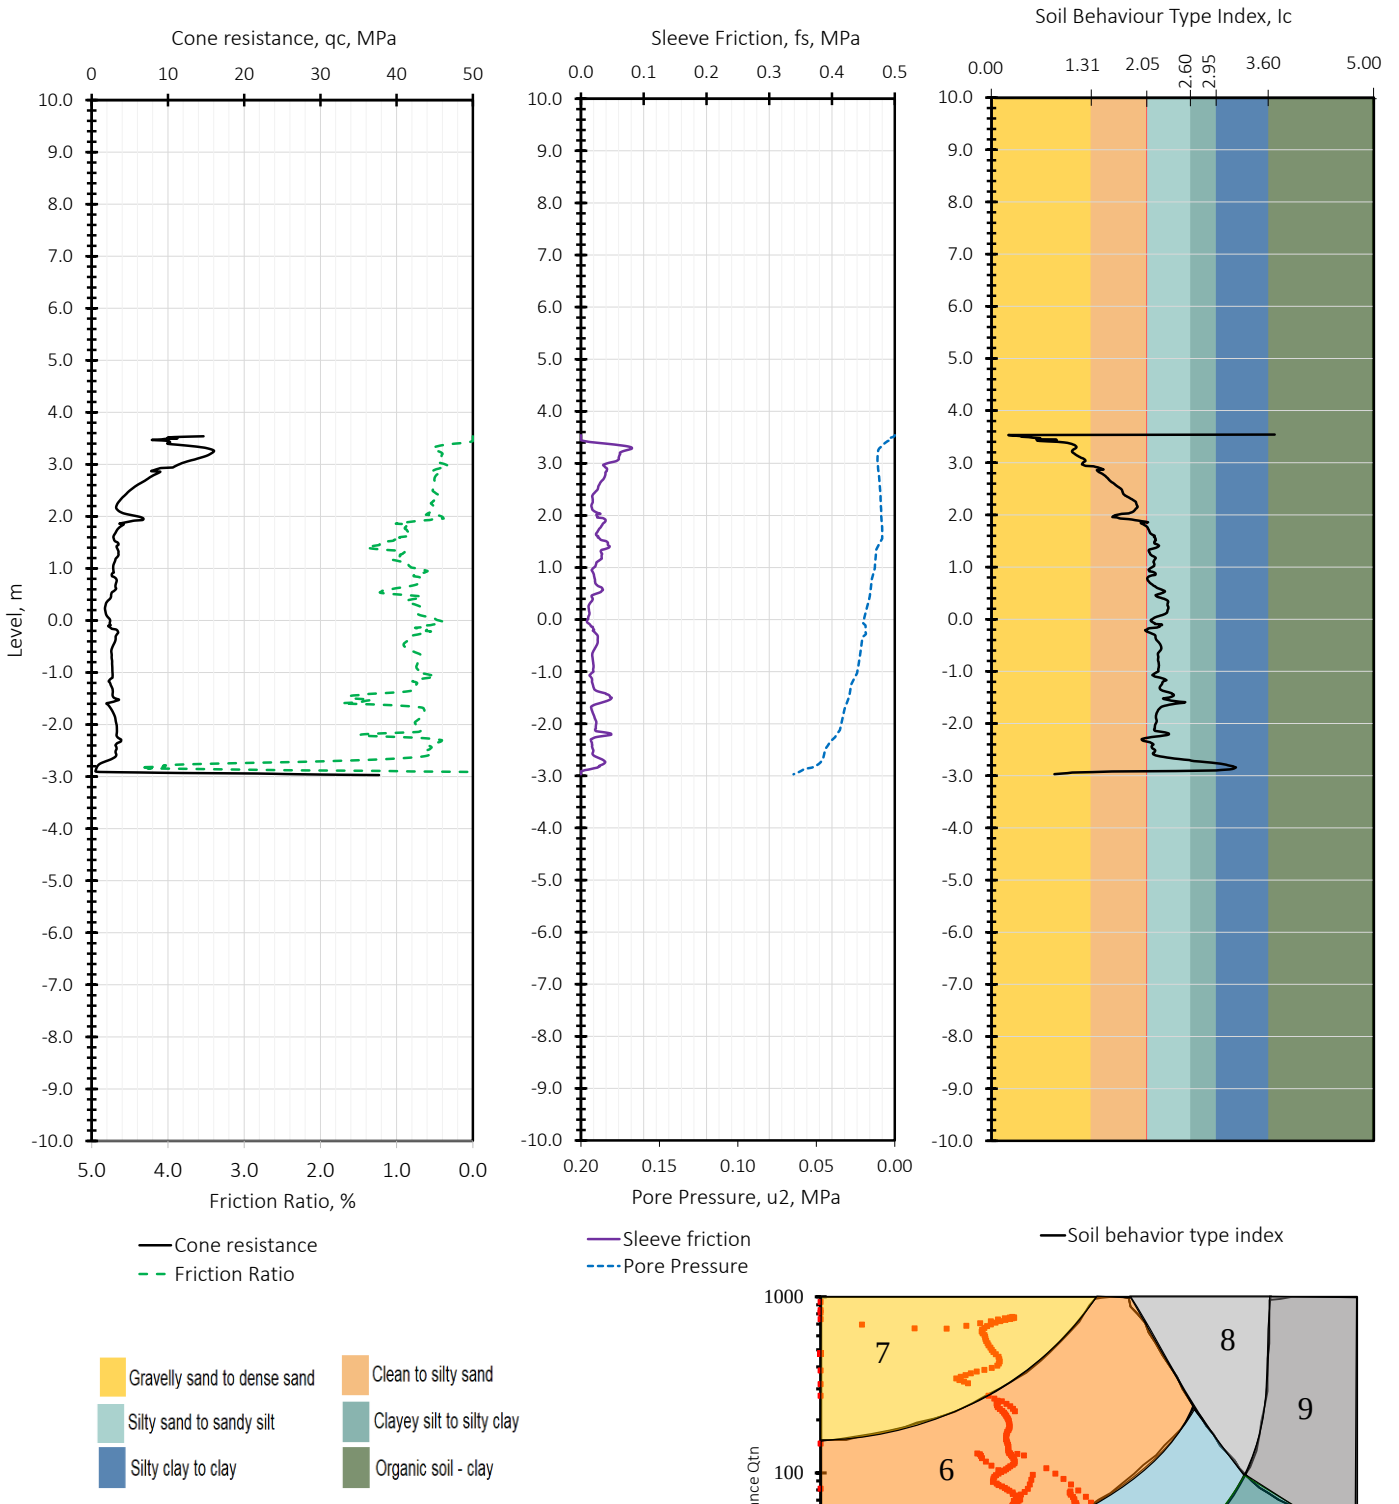

Main Contractor:	CTS GULF	
Test Location:	CPT-A1-B380-100	
Ground Elevation:	3.54	
	Easting	**Northing**
Coordinates:	421249.802	2928335.593
Cone ID:	DP15-CFPTxy.71431	
Test Date	19-Sep-2026	