
Client : SAUDI GLOBAL PORTS

Project : DAMMAM LOGISTICS ZONE

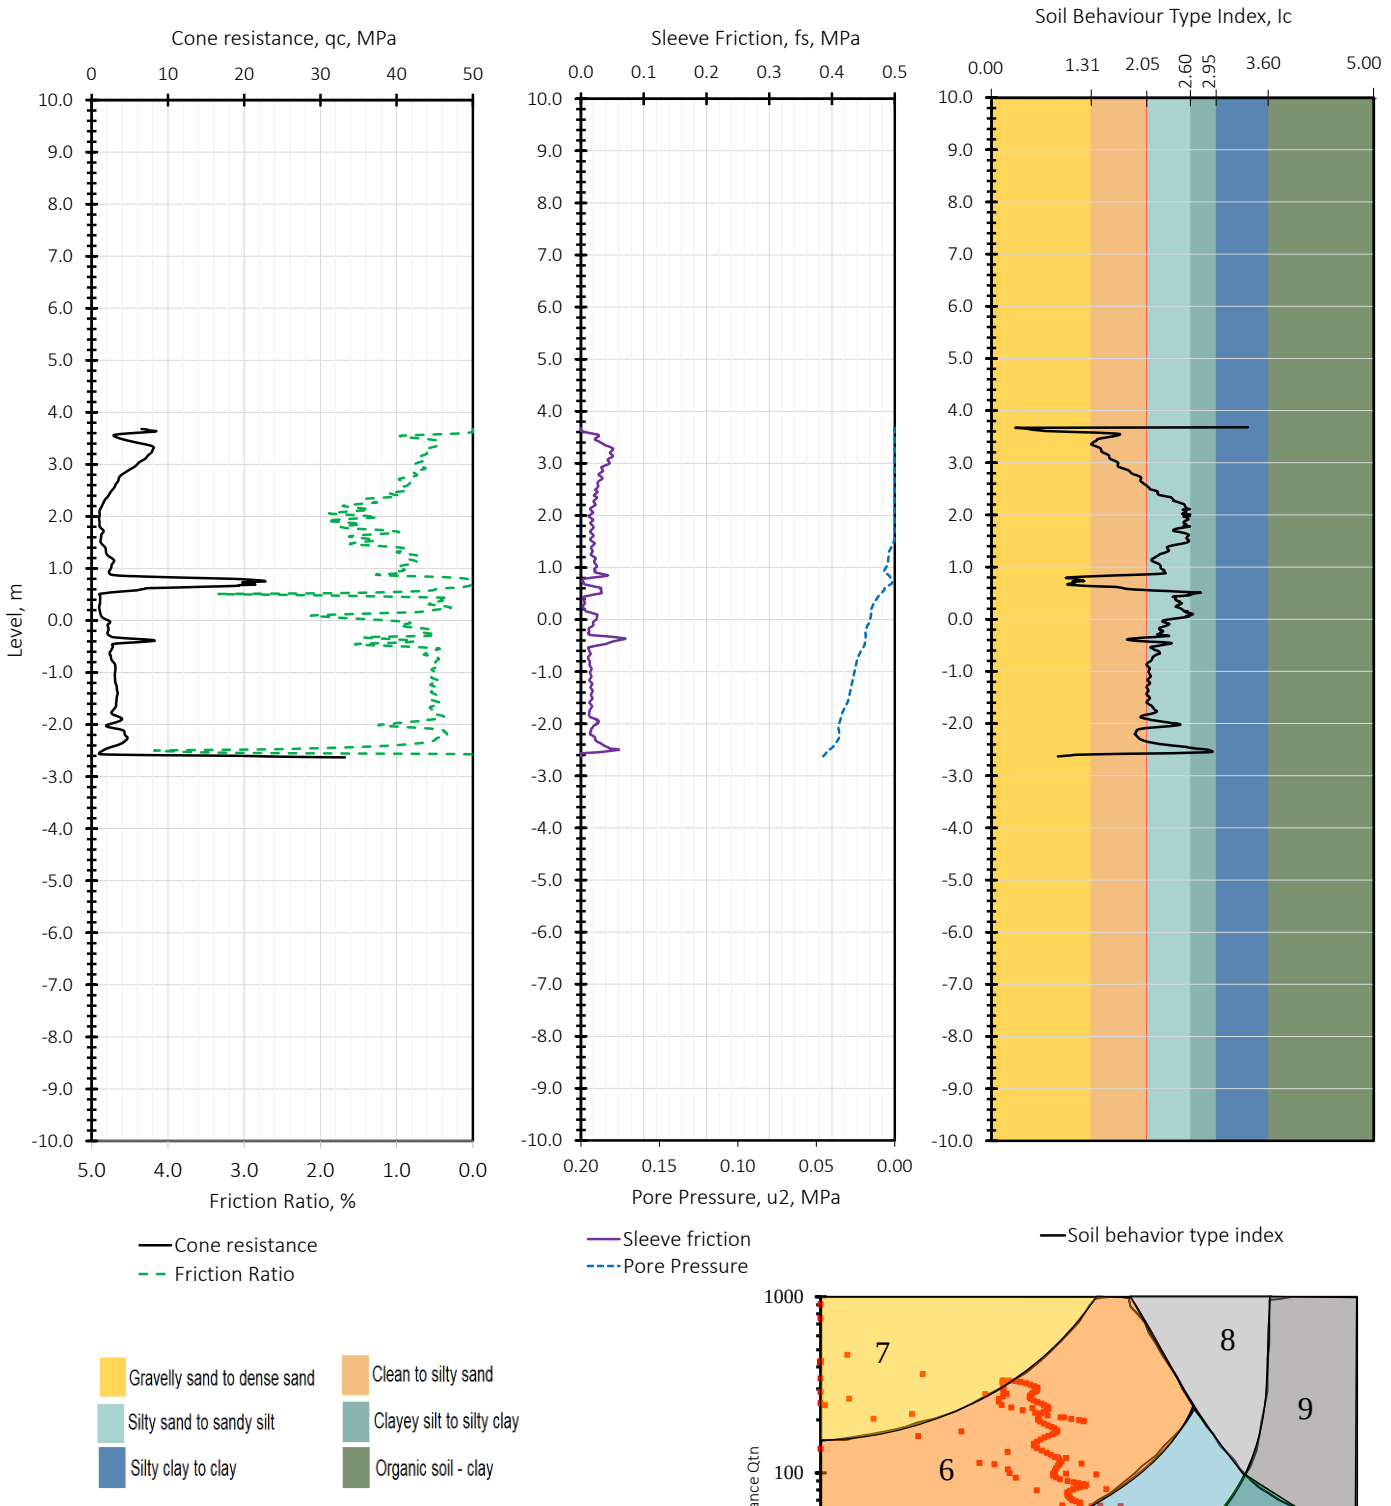

Main Contractor:	CTS GULF	
Test Location:	CPT-A1-B381-100	
Ground Elevation:	3.68	
	Easting	**Northing**
Coordinates:	421170.802	2928077.543
Cone ID:	DP15-CFPTxy.71431	
Test Date	8-Oct-2026	