

Client : SAUDI GLOBAL PORTS

Project : DAMMAM LOGISTICS ZONE

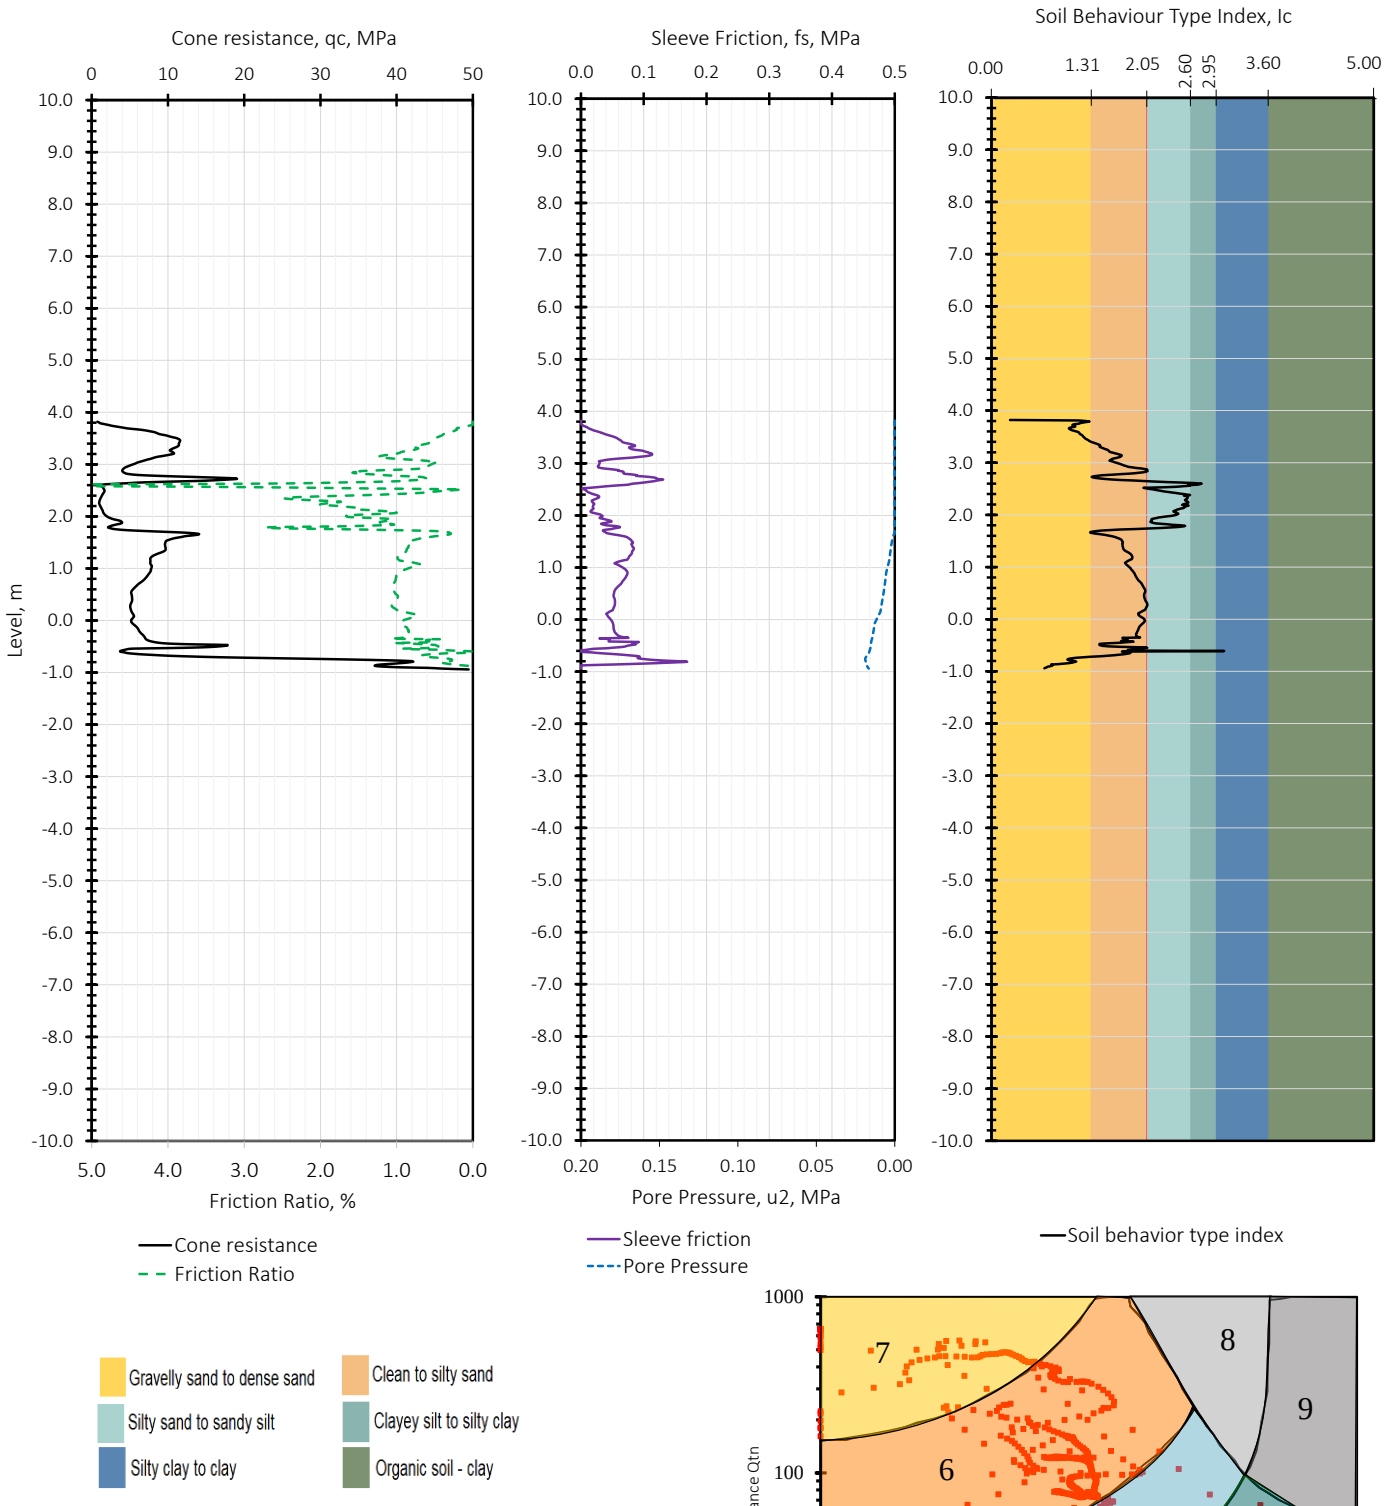

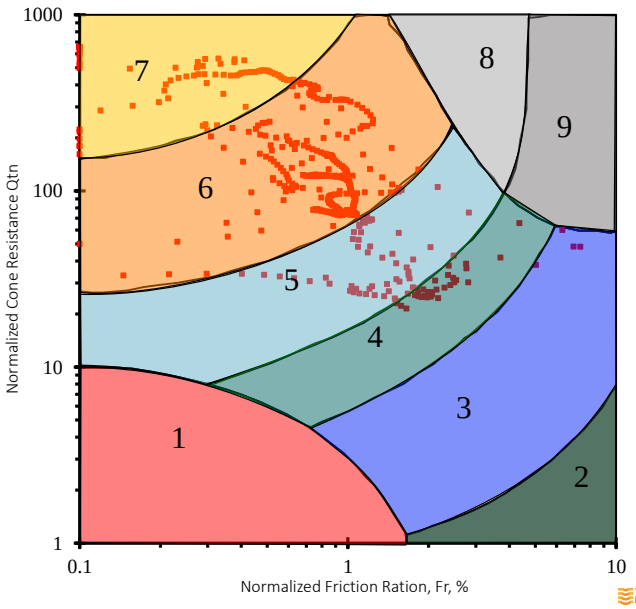

Main Contractor:	CTS GULF	
Test Location:	CPT-A1-B50-100	
Ground Elevation:	3.82	
	Easting	**Northing**
Coordinates:	420556.942	2927688.51
Cone ID:	DP15-CFPTxy.71424	
Test Date	8-Oct-2026	