

Client : SAUDI GLOBAL PORTS

Project : DAMMAM LOGISTICS ZONE

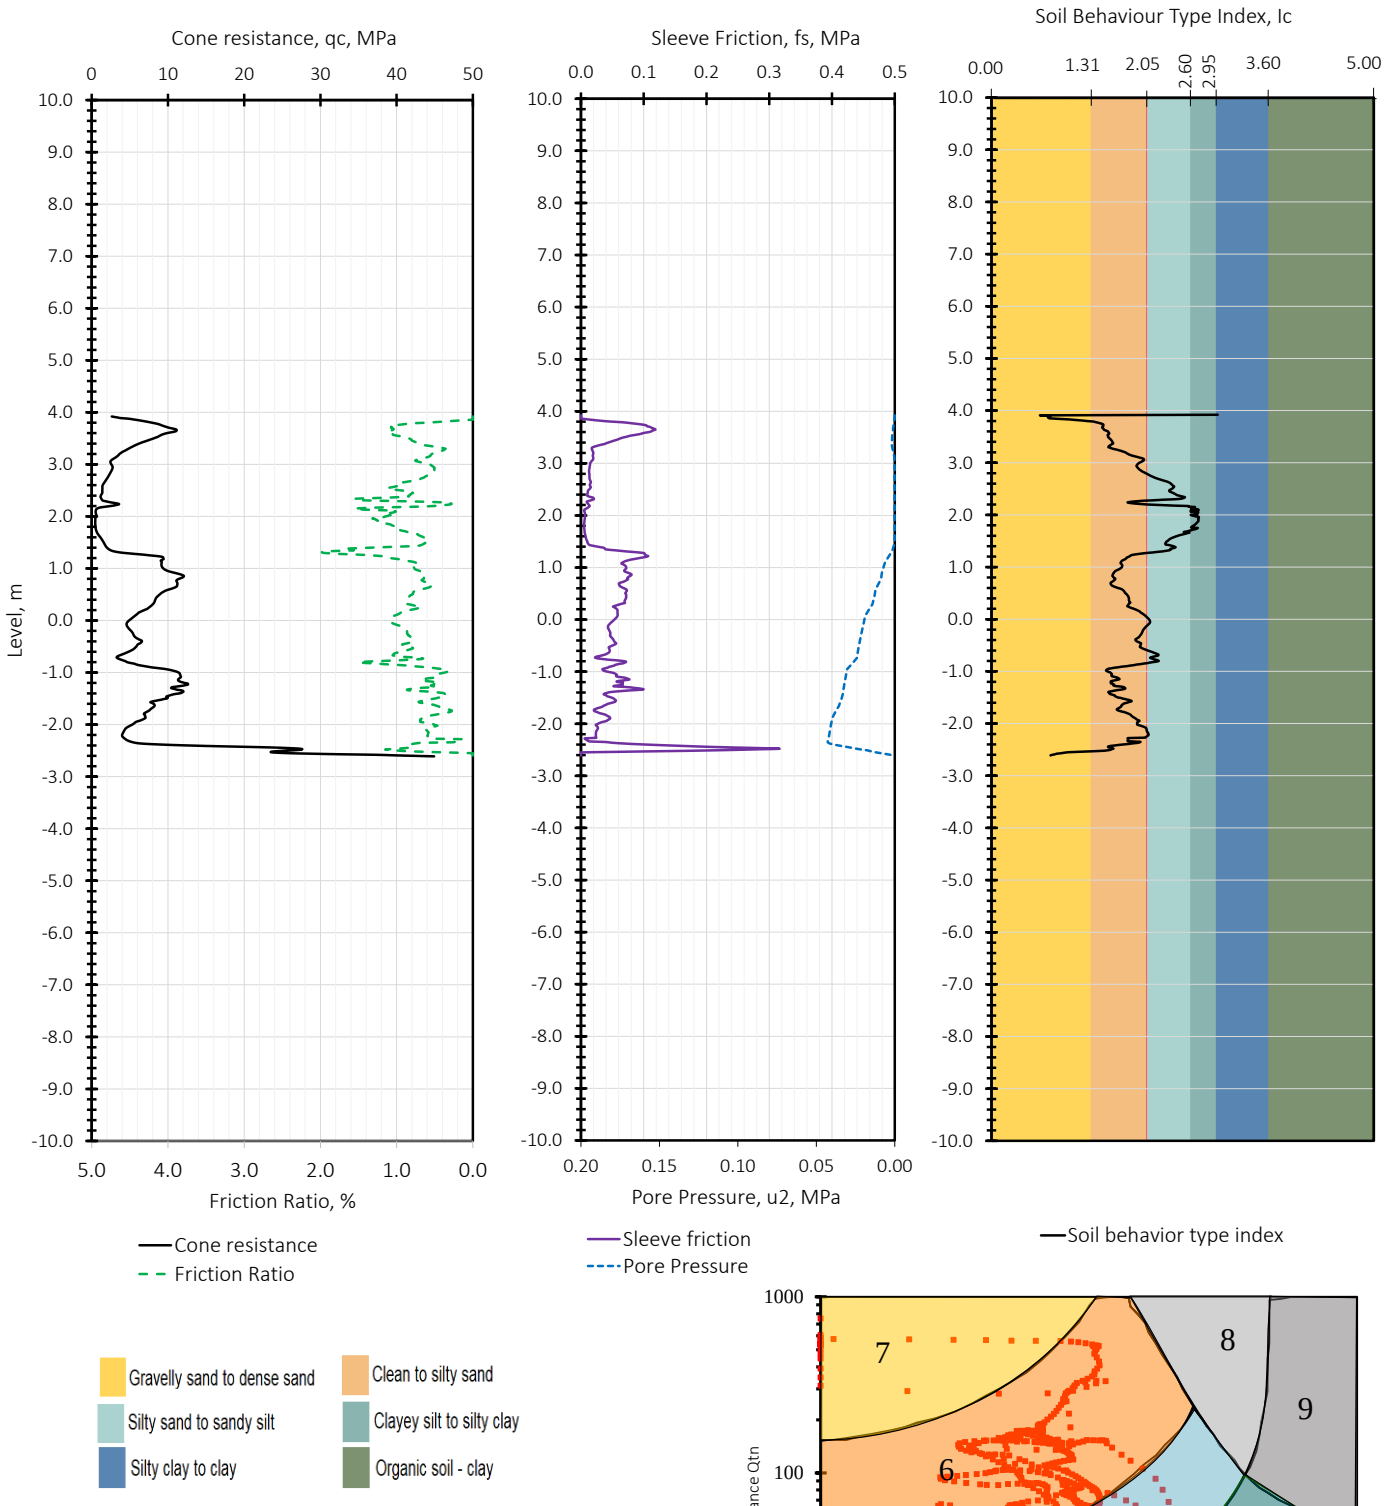

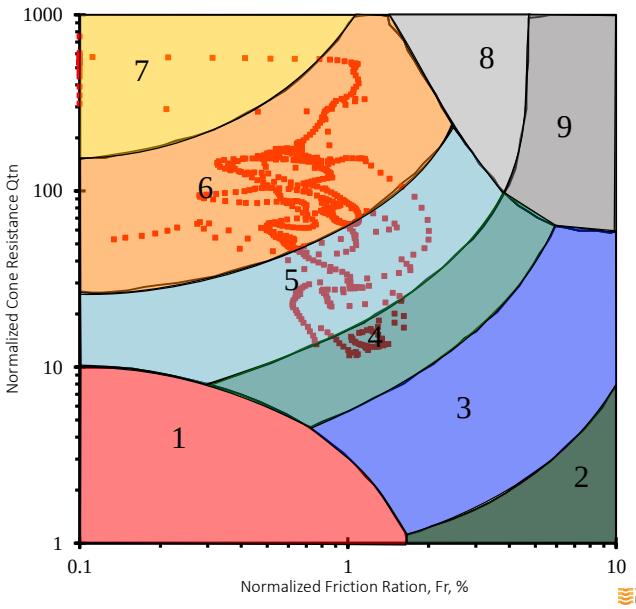

Main Contractor:	CTS GULF	
Test Location:	CPT-A1-B51-100	
Ground Elevation:	3.92	
	Easting	**Northing**
Coordinates:	420564.179	2927712.439
Cone ID:	DP15-CFPTxy.71424	
Test Date	8-Oct-2026	