
Client : SAUDI GLOBAL PORTS

Project : DAMMAM LOGISTICS ZONE

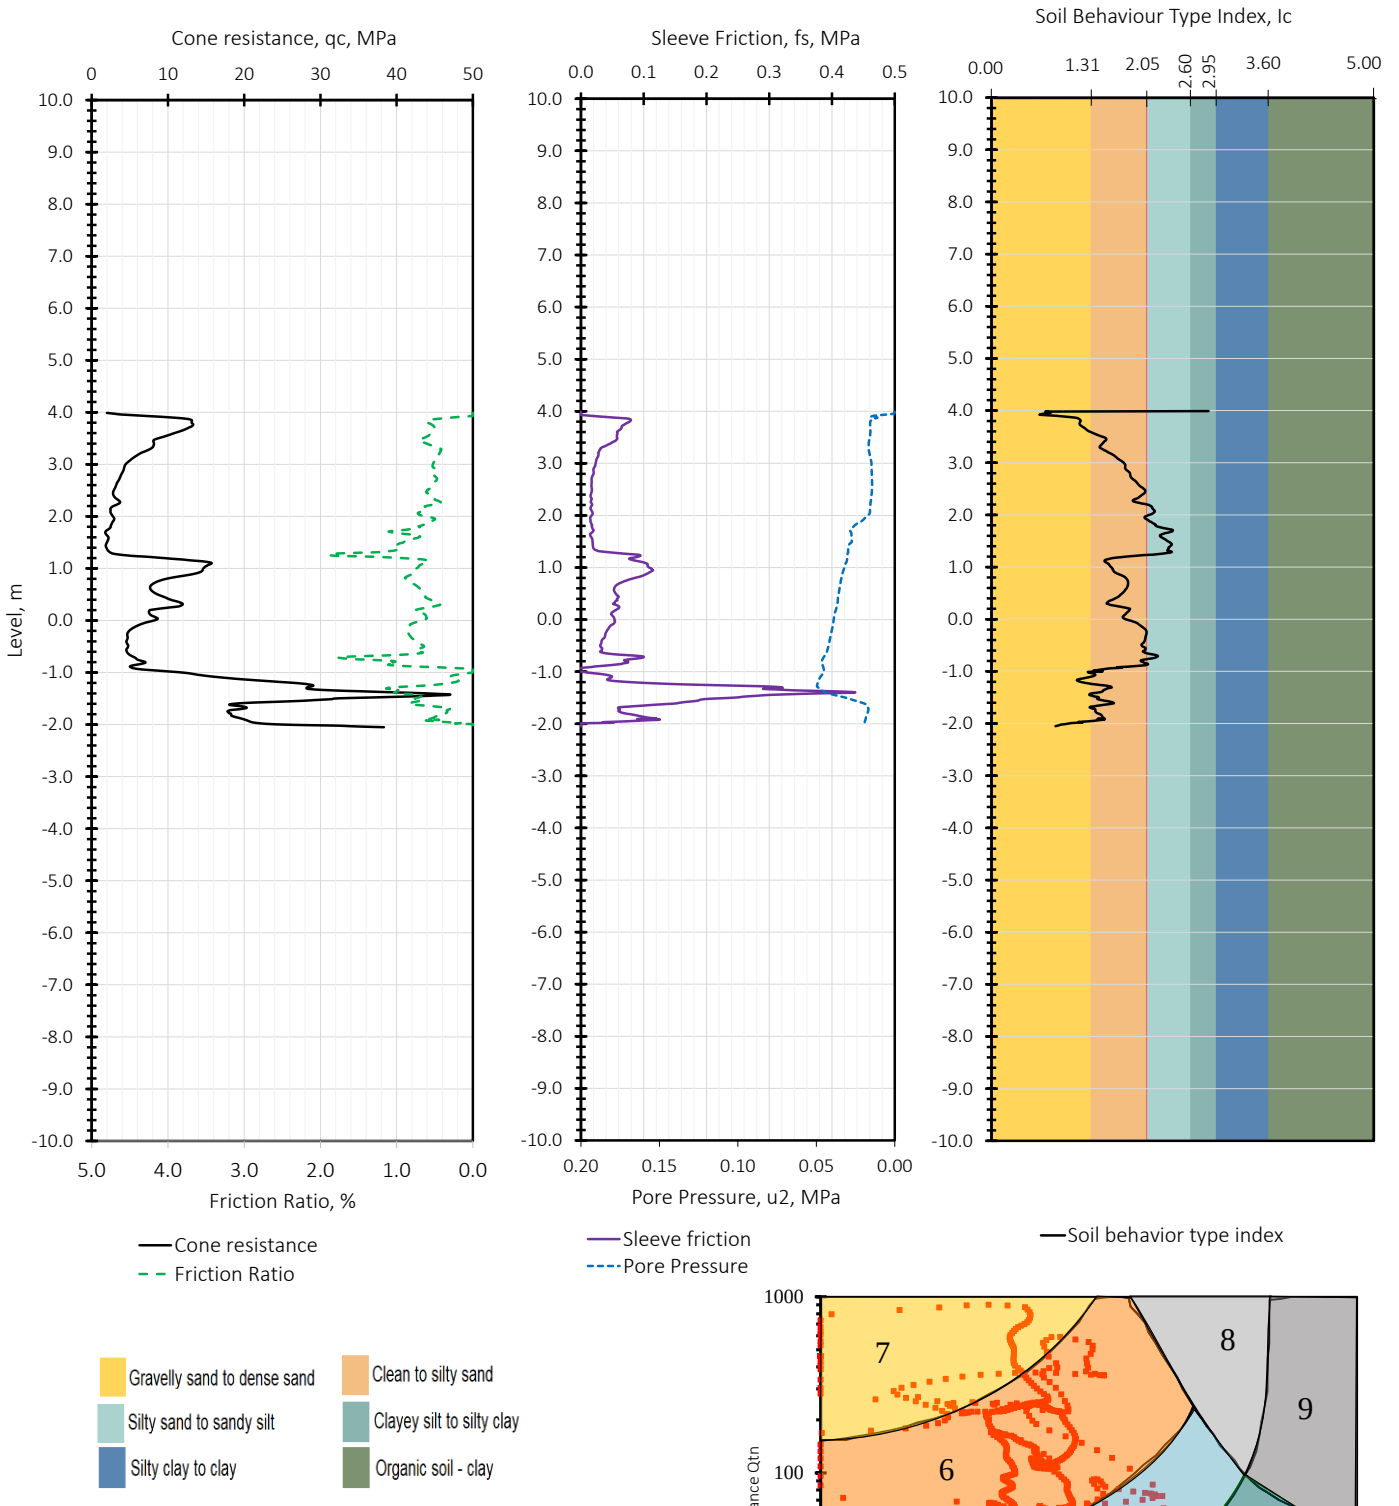

Main Contractor:	CTS GULF	
Test Location:	CPT-A1-B52-100	
Ground Elevation:	3.99	
	Easting	**Northing**
Coordinates:	420571.416	2927736.369
Cone ID:	DP15-CFPTxy.71424	
Test Date	8-Oct-2026	