
Client : SAUDI GLOBAL PORTS

Project : DAMMAM LOGISTICS ZONE

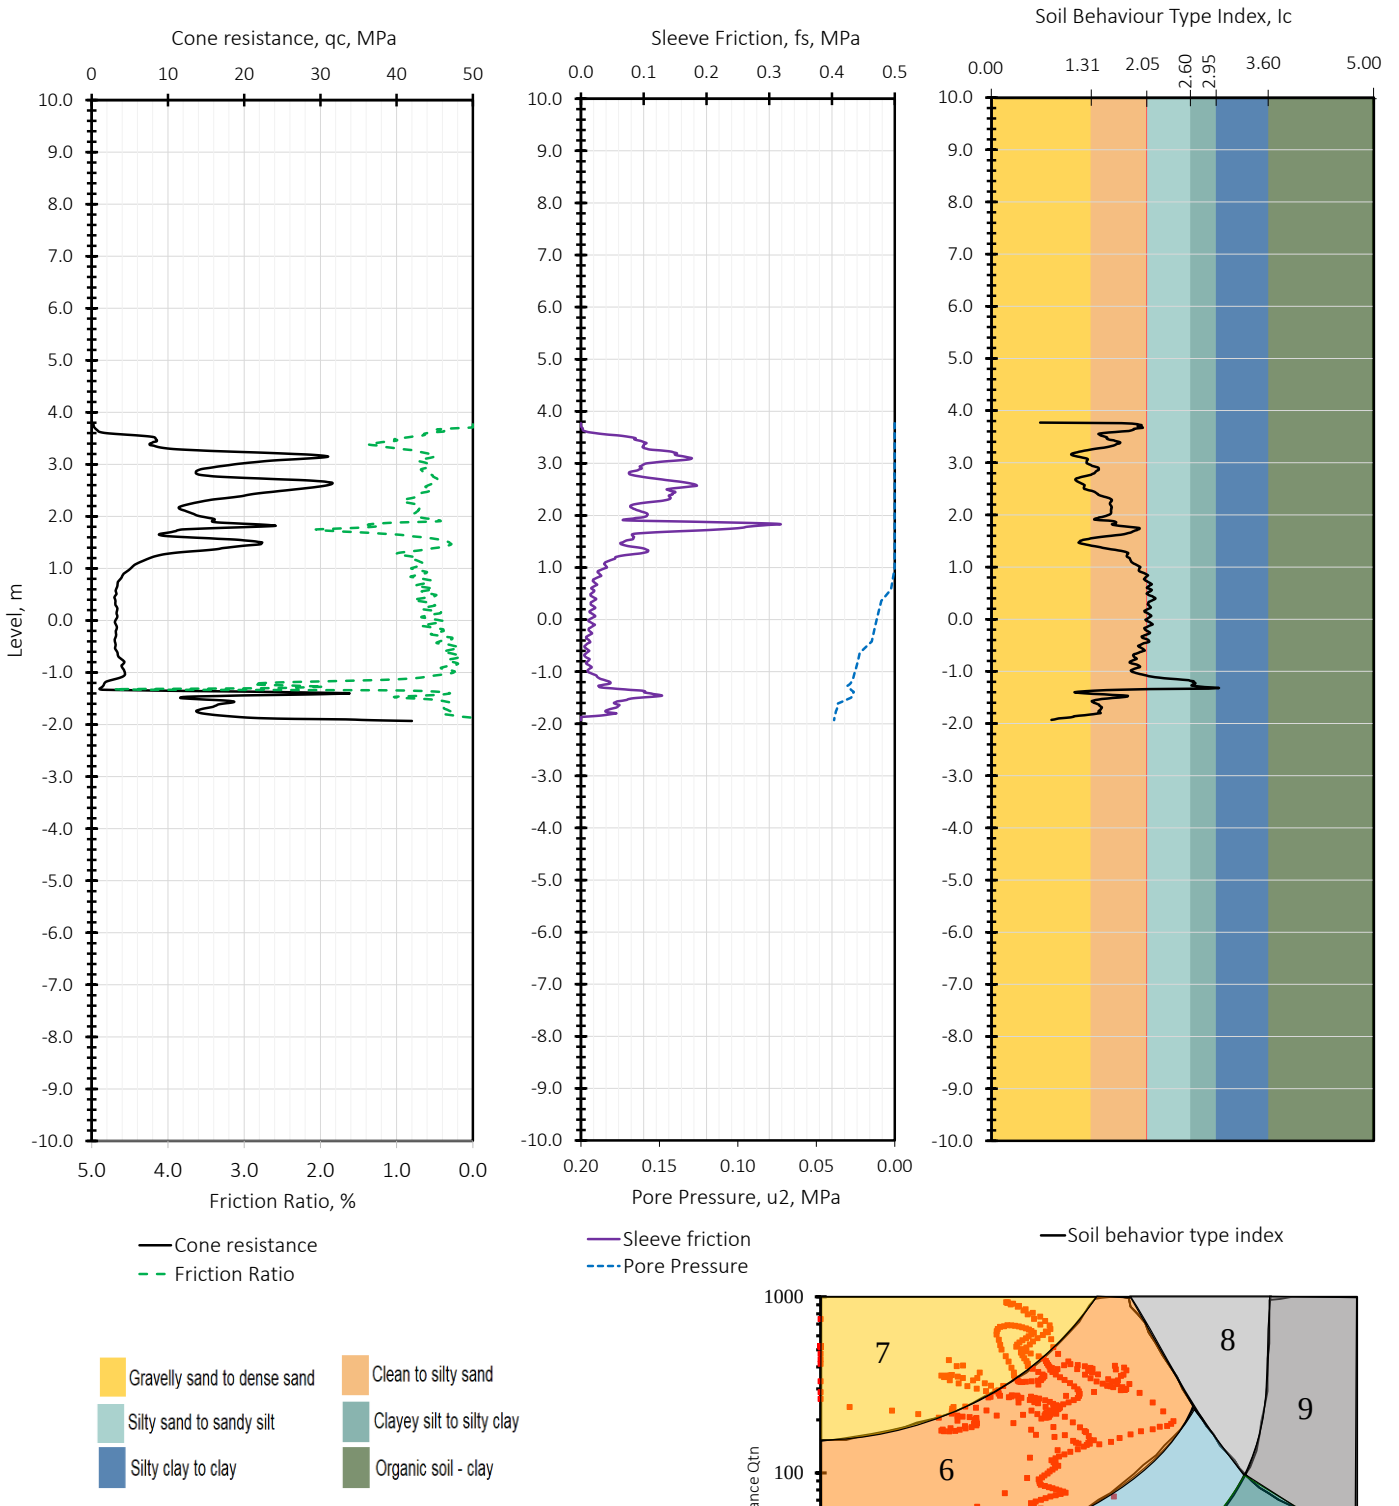

Main Contractor:	CTS GULF	
Test Location:	CPT-A1-B58-100-1	
Ground Elevation:	3.77	
	Easting	**Northing**
Coordinates:	420614.837	2927879.947
Cone ID:	DP15-CFPTxy.71431	
Test Date	8-Oct-2026	