

Client : SAUDI GLOBAL PORTS

Project : DAMMAM LOGISTICS ZONE

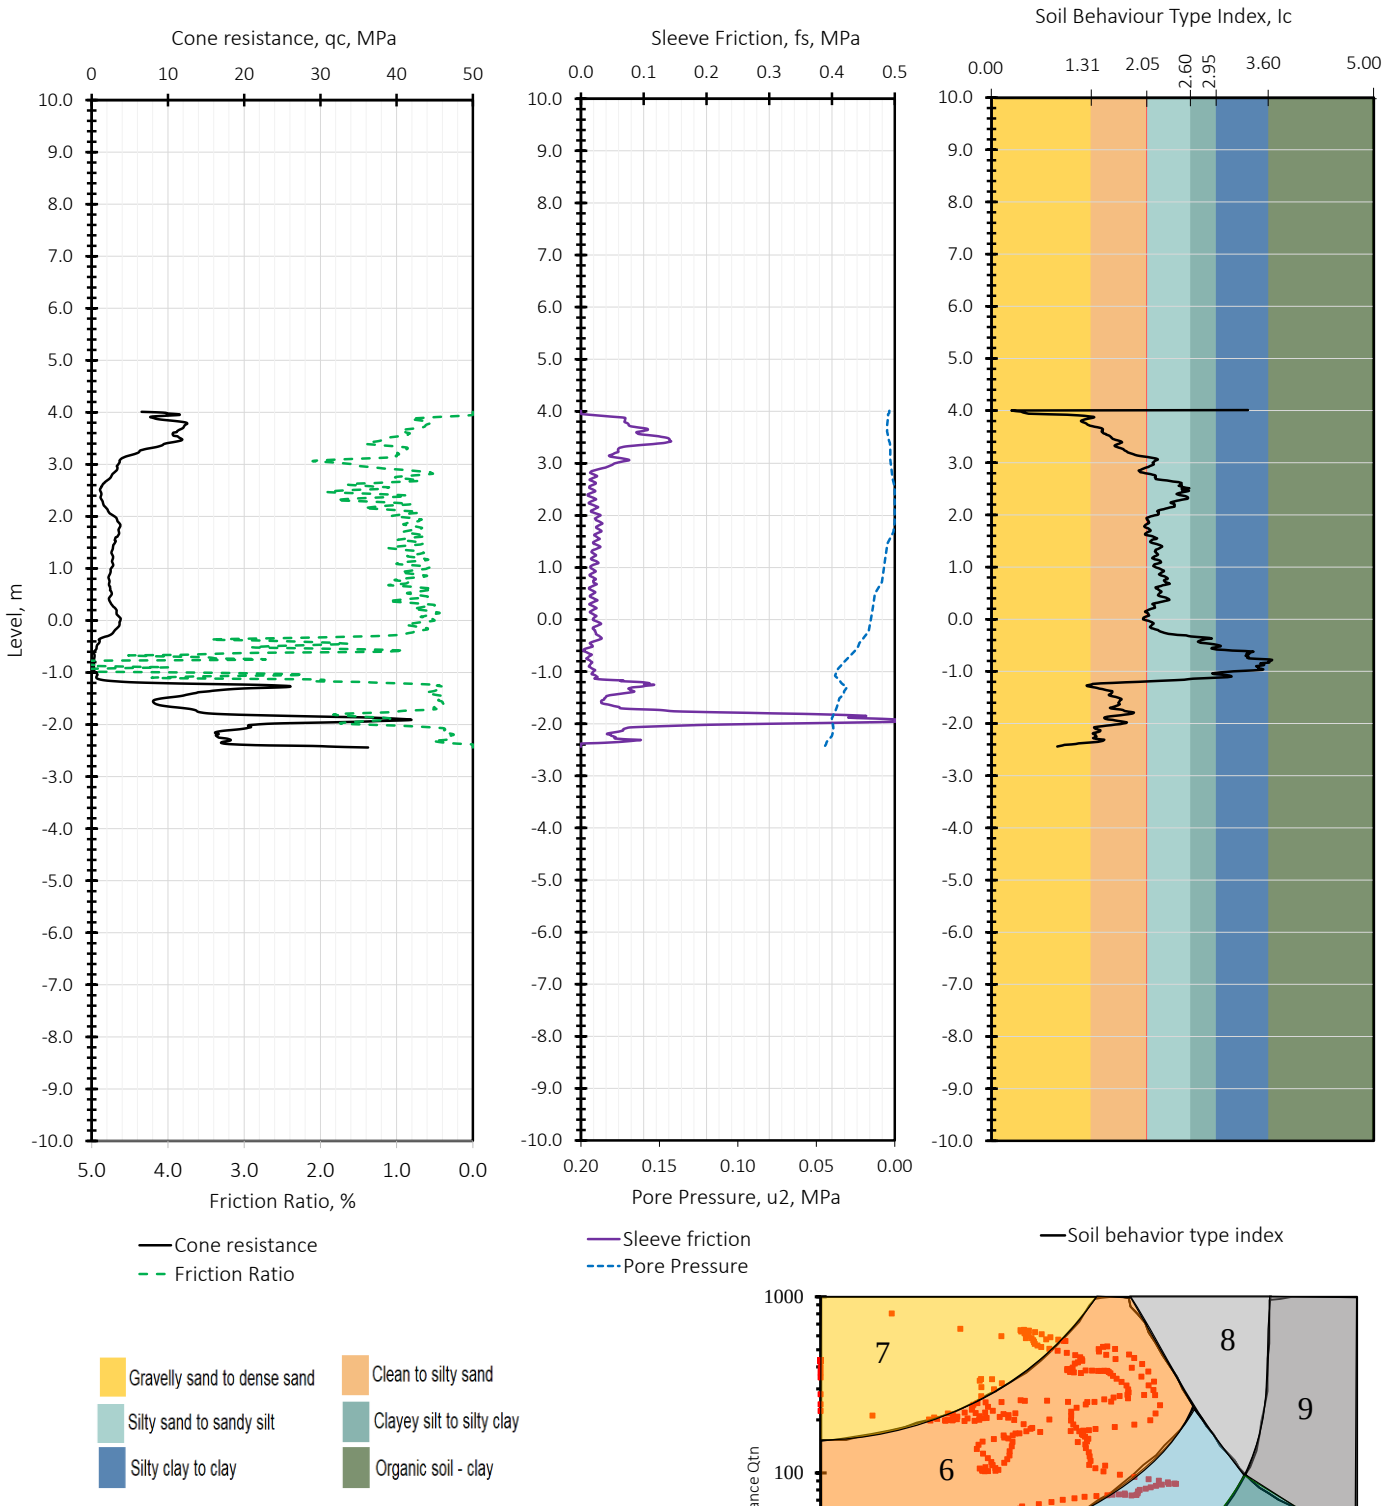

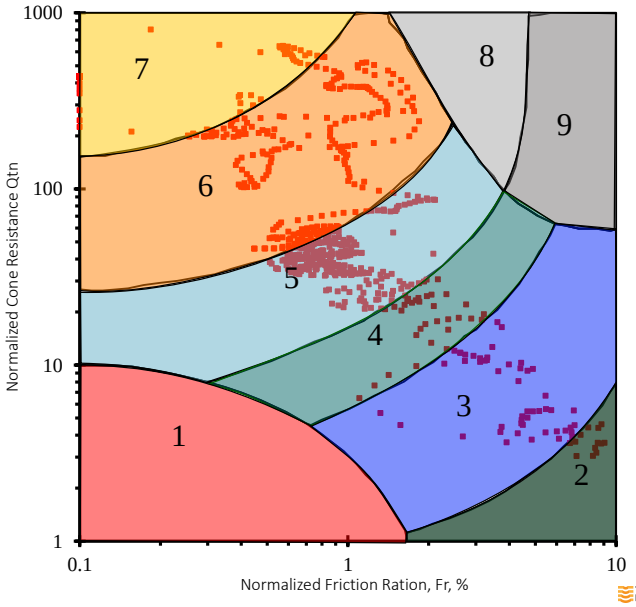

Main Contractor:	CTS GULF	
Test Location:	CPT-A1-B66-100	
Ground Elevation:	4.01	
	Easting	**Northing**
Coordinates:	420992.694	2927661.202
Cone ID:	DP15-CFPTxy.71431	
Test Date	10-Oct-2026	