
Client : SAUDI GLOBAL PORTS

Project : DAMMAM LOGISTICS ZONE

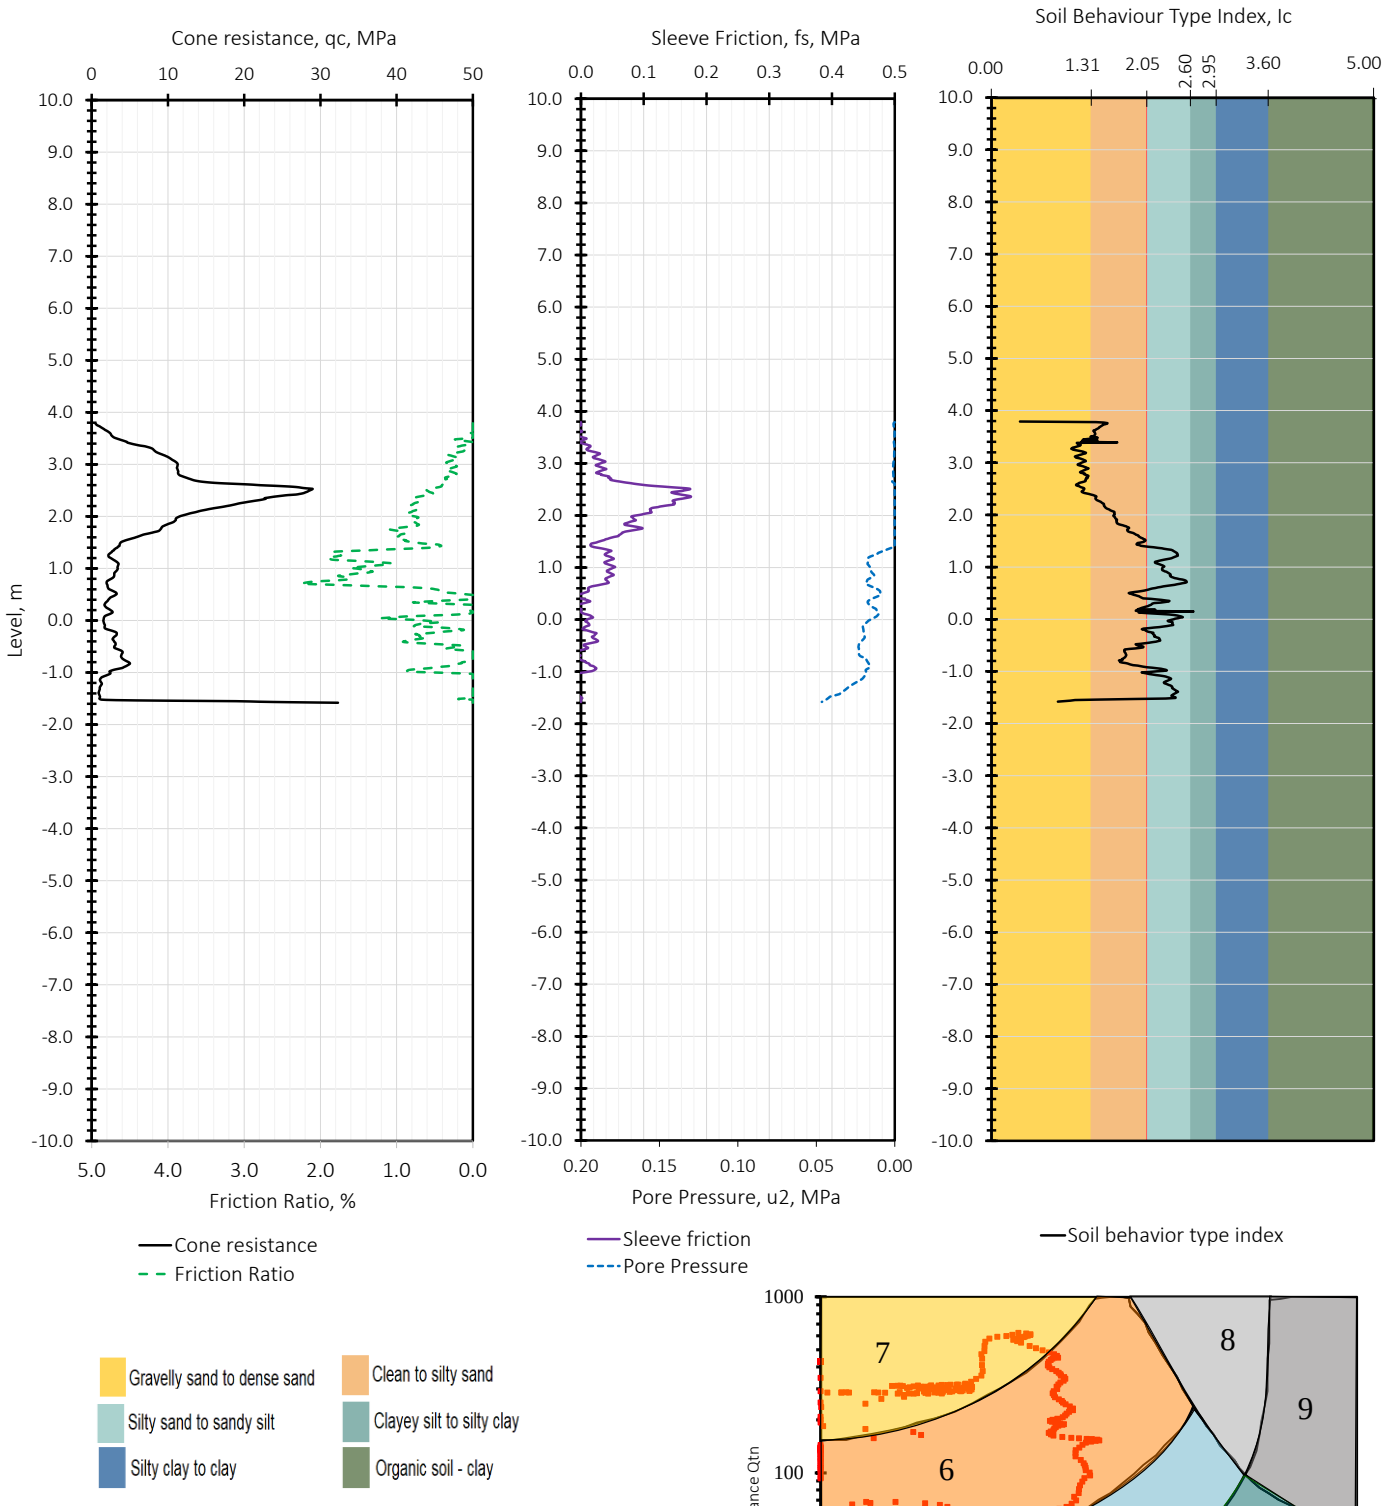

Main Contractor:	CTS GULF	
Test Location:	CPT-A1-B70-100	
Ground Elevation:	3.79	
	Easting	**Northing**
Coordinates:	420638.767	2927872.71
Cone ID:	DP15-CFPTxy.71431	
Test Date	8-Oct-2026	