

Client : SAUDI GLOBAL PORTS

Project : DAMMAM LOGISTICS ZONE

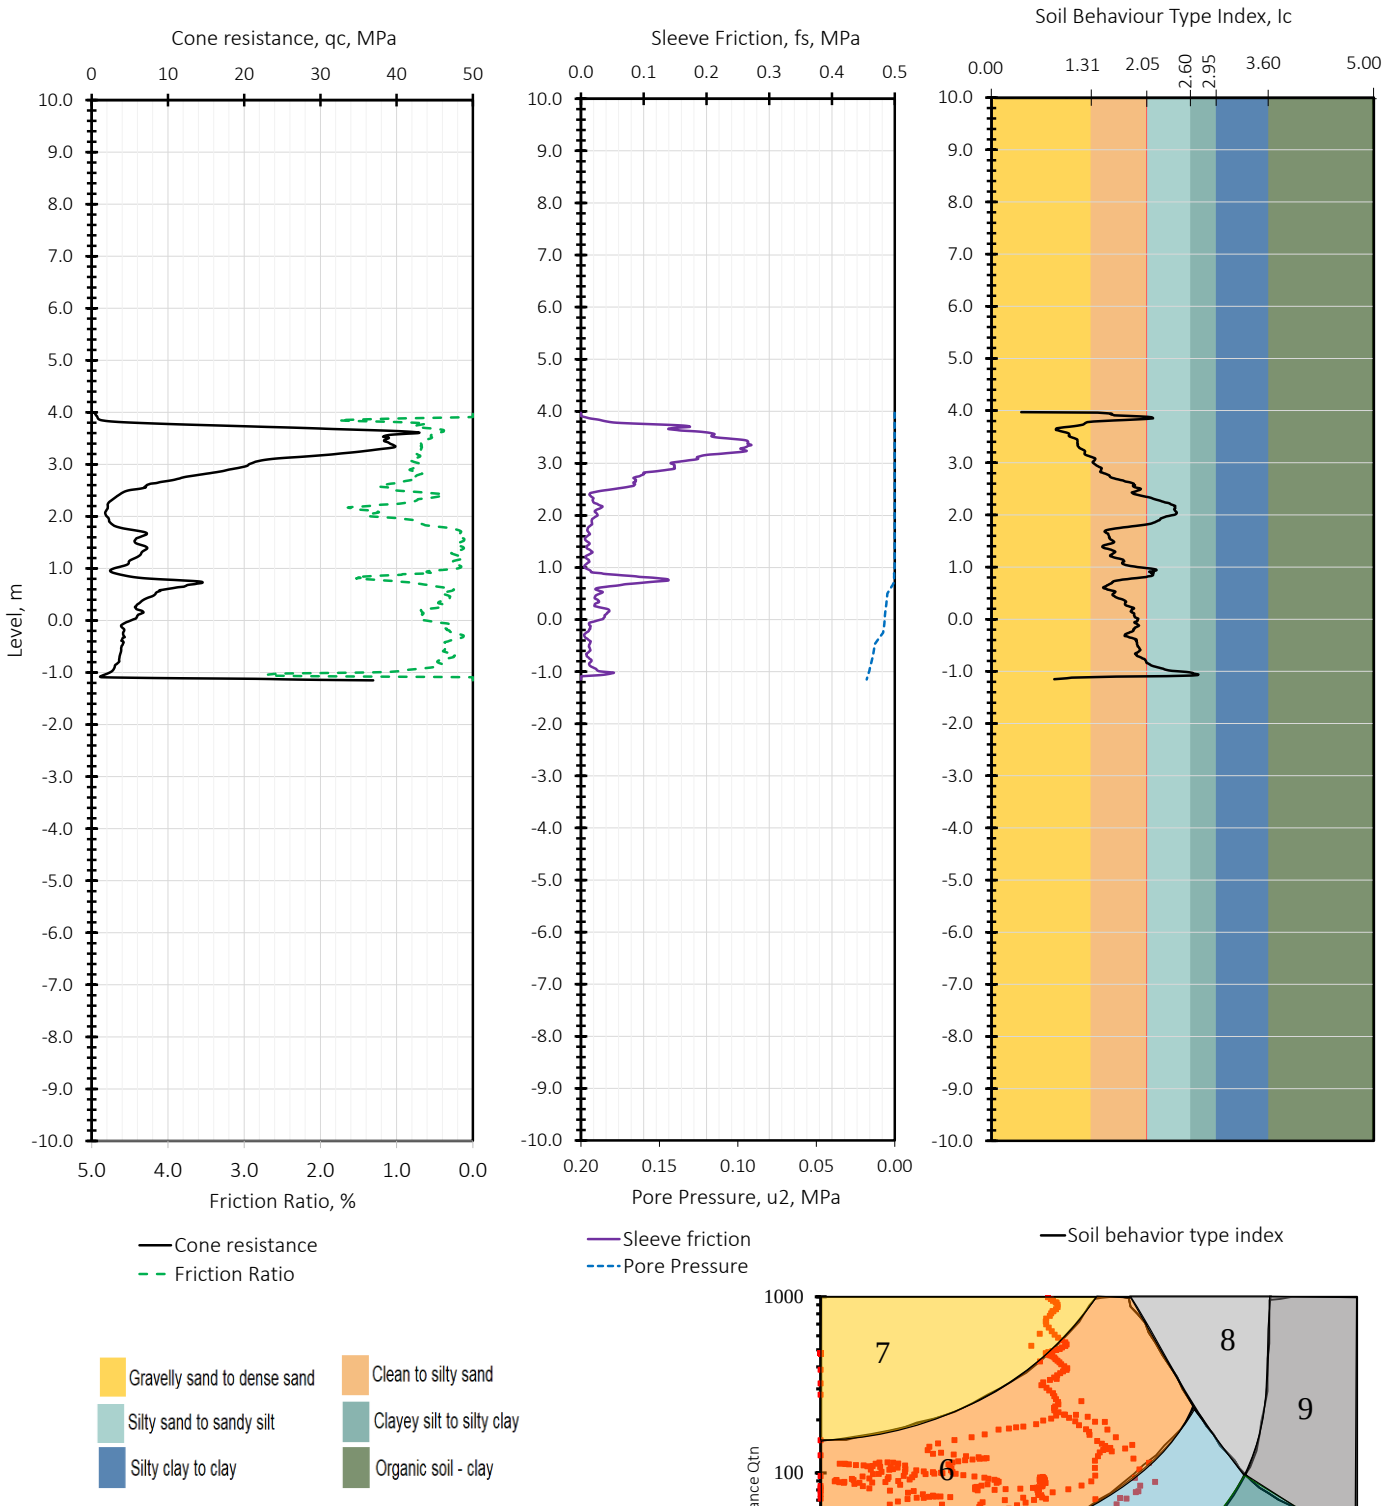

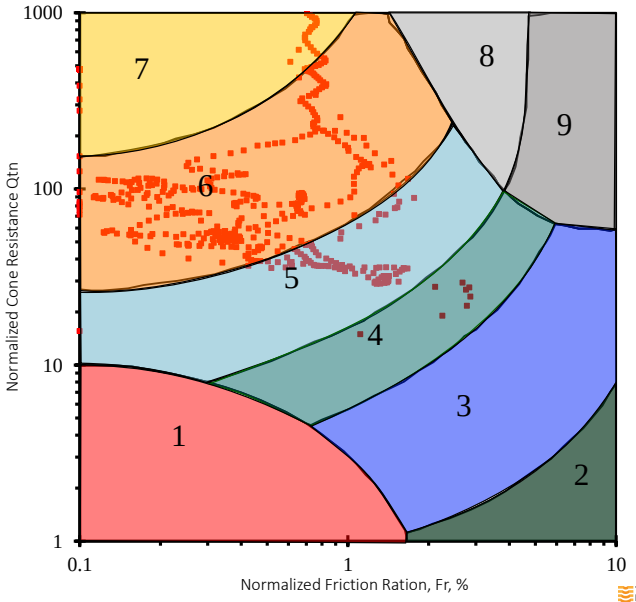

Main Contractor:	CTS GULF	
Test Location:	CPT-A1-B72-100	
Ground Elevation:	3.97	
	Easting	**Northing**
Coordinates:	420550.082	2927909.409
Cone ID:	DP15-CFPTxy.71431	
Test Date	10-Oct-2026	