
Client : SAUDI GLOBAL PORTS

Project : DAMMAM LOGISTICS ZONE

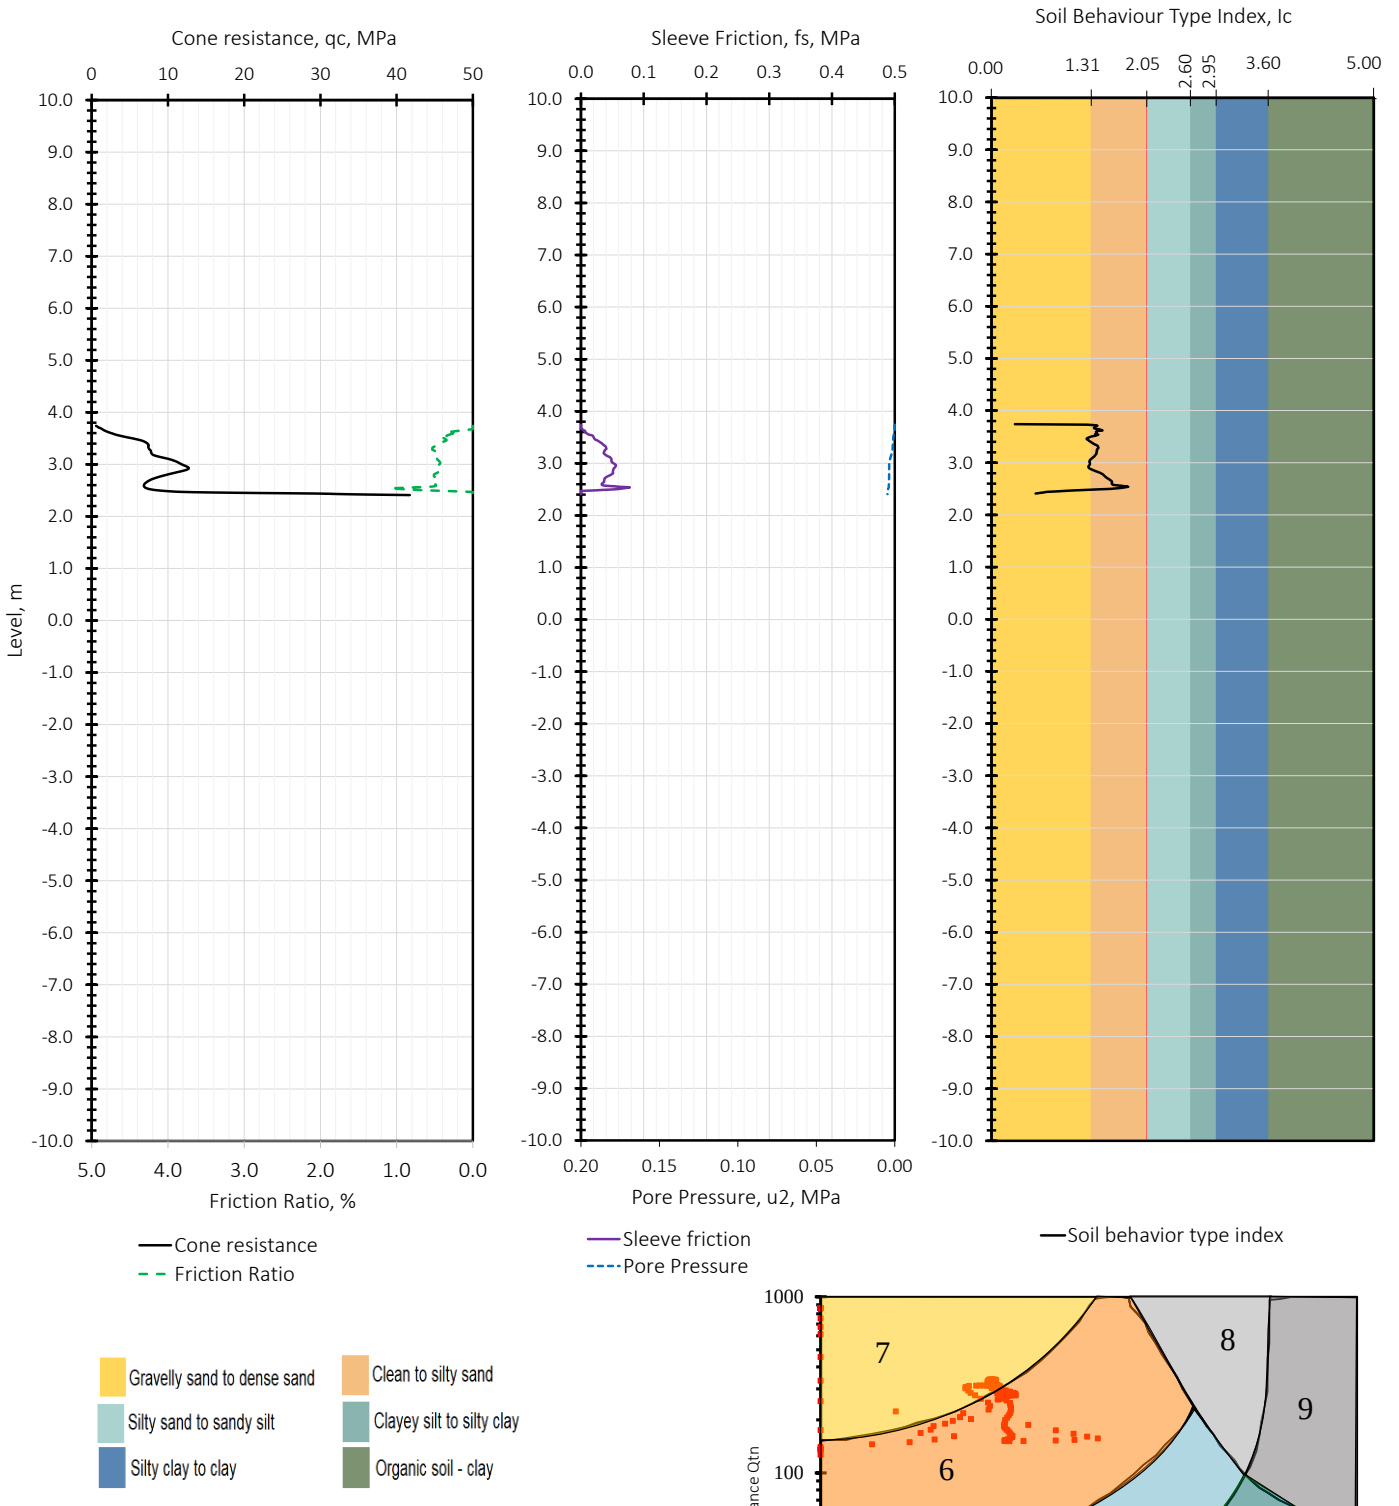

Main Contractor:	CTS GULF	
Test Location:	CPT-A1-B84-100	
Ground Elevation:	3.74	
	Easting	**Northing**
Coordinates:	420669.933	2927889.403
Cone ID:	DP15-CFPTxy.71431	
Test Date	7-Oct-2026	