
Client : SAUDI GLOBAL PORTS

Project : DAMMAM LOGISTICS ZONE

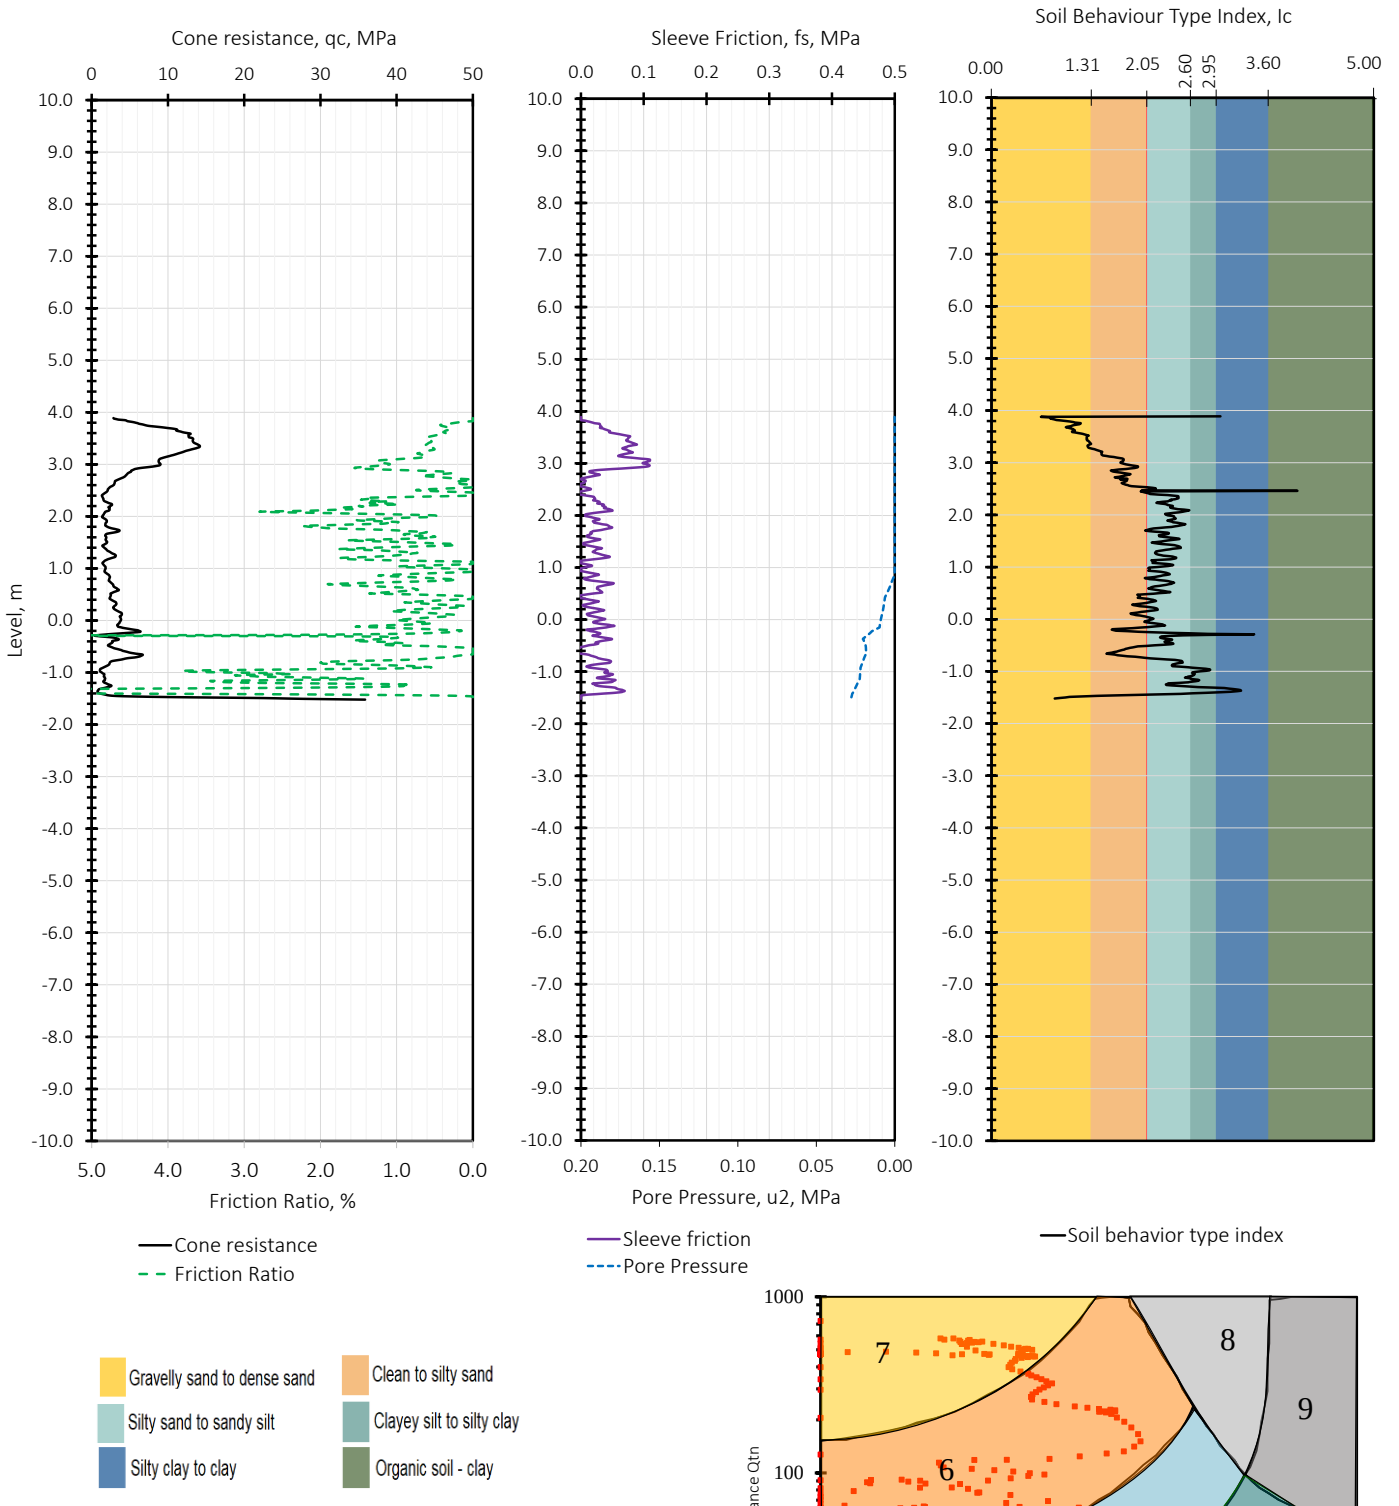

Main Contractor:	CTS GULF	
Test Location:	CPT-A1-B87-100	
Ground Elevation:	3.89	
	Easting	**Northing**
Coordinates:	420628.731	2927666.799
Cone ID:	DP15-CFPTxy.71431	
Test Date	11-Oct-2026	