
Client : SAUDI GLOBAL PORTS

Project : DAMMAM LOGISTICS ZONE

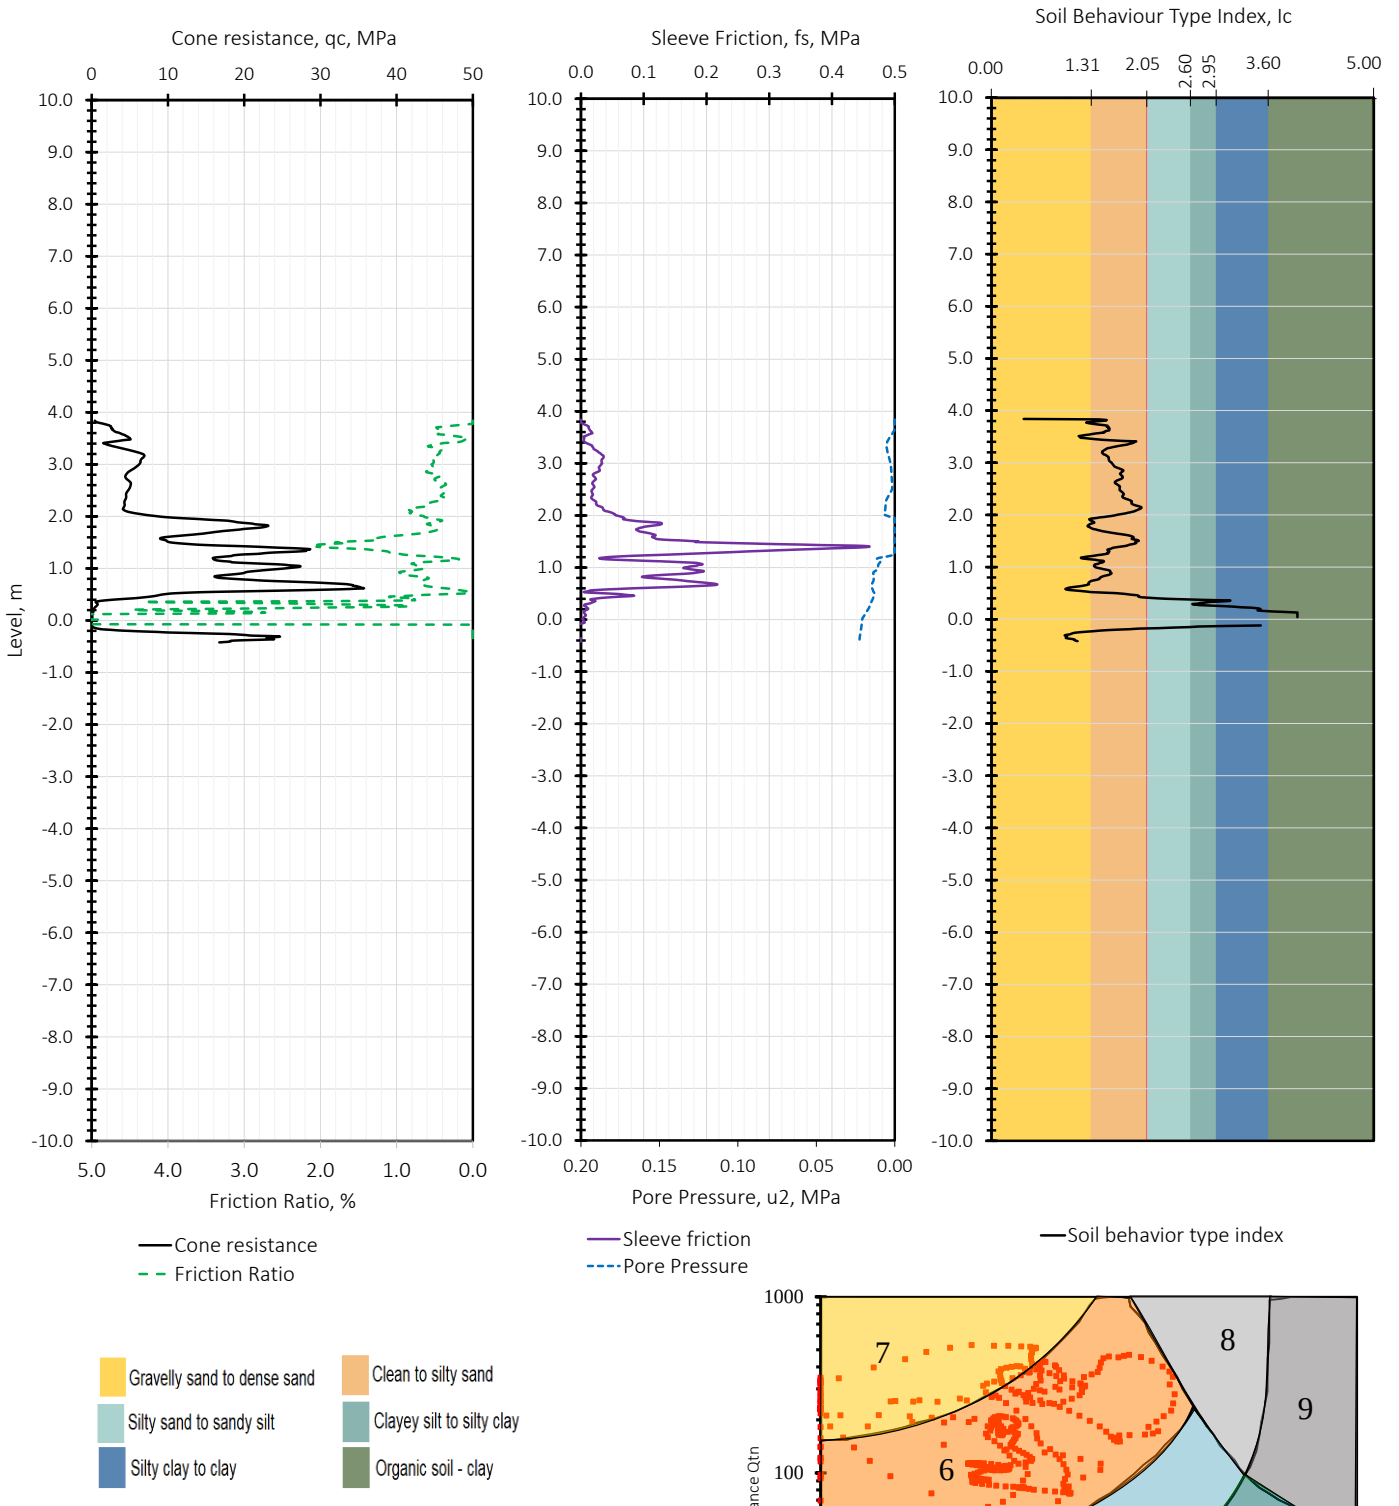

Main Contractor:	CTS GULF	
Test Location:	CPT-A1-B93-100-1	
Ground Elevation:	3.84	
	Easting	**Northing**
Coordinates:	420672.152	2927810.377
Cone ID:	DP15-CFPTxy.71431	
Test Date	7-Oct-2026	