

Client : SAUDI GLOBAL PORTS

Project : DAMMAM LOGISTICS ZONE

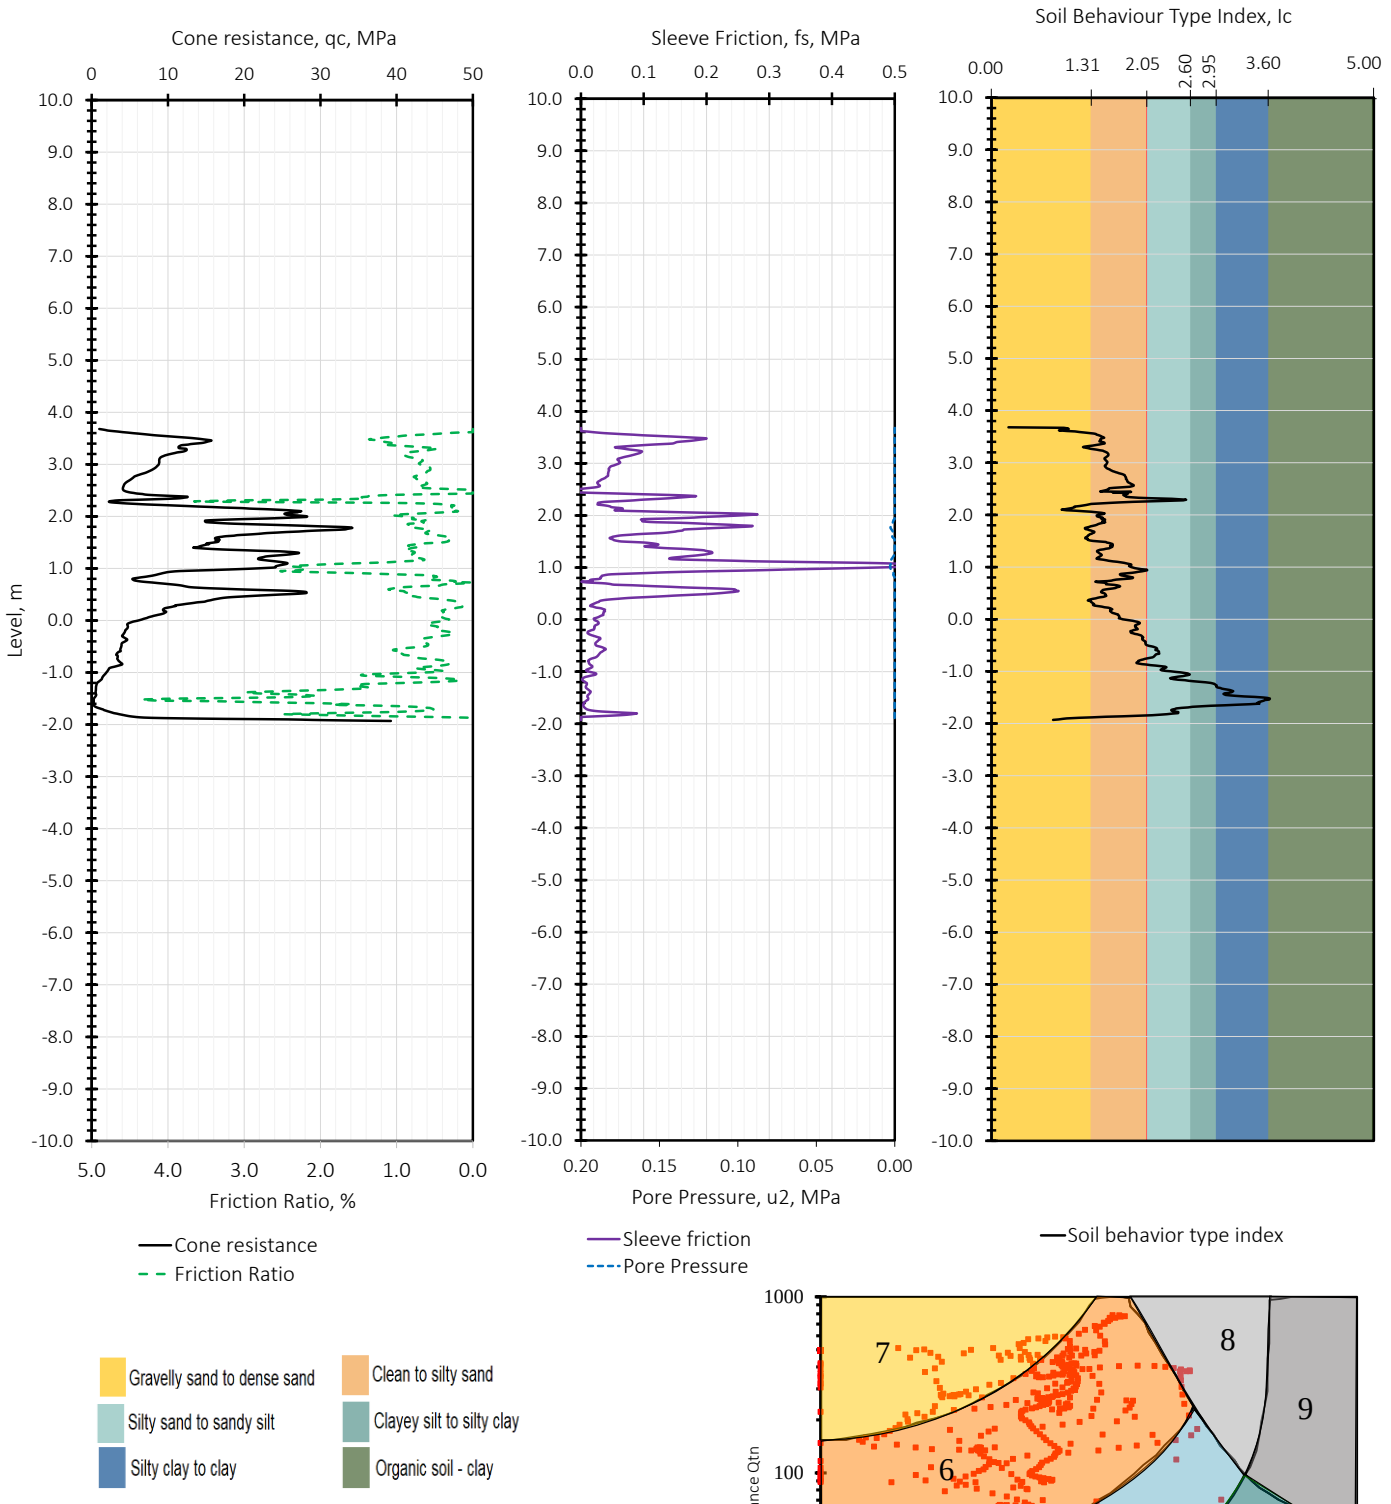

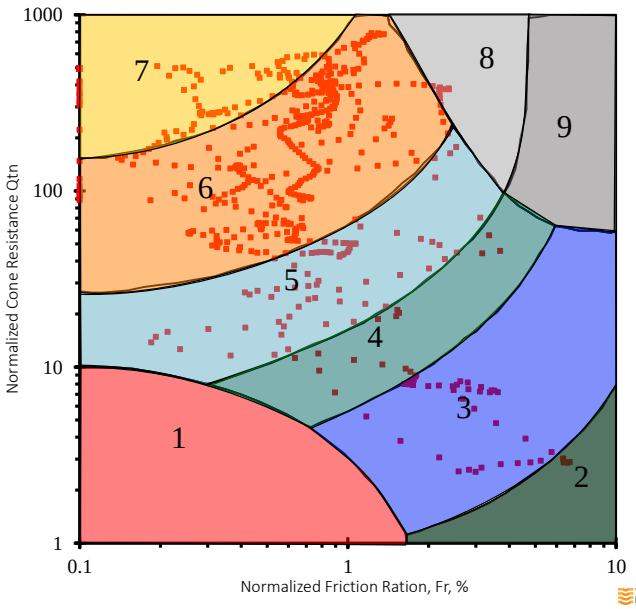

Main Contractor:	CTS GULF	
Test Location:	CPT-A1-B94-100	
Ground Elevation:	3.68	
	Easting	**Northing**
Coordinates:	420679.389	2927834.307
Cone ID:	DP15-CFPTxy.71431	
Test Date	7-Oct-2026	