
Client : SAUDI GLOBAL PORTS

Project : DAMMAM LOGISTICS ZONE

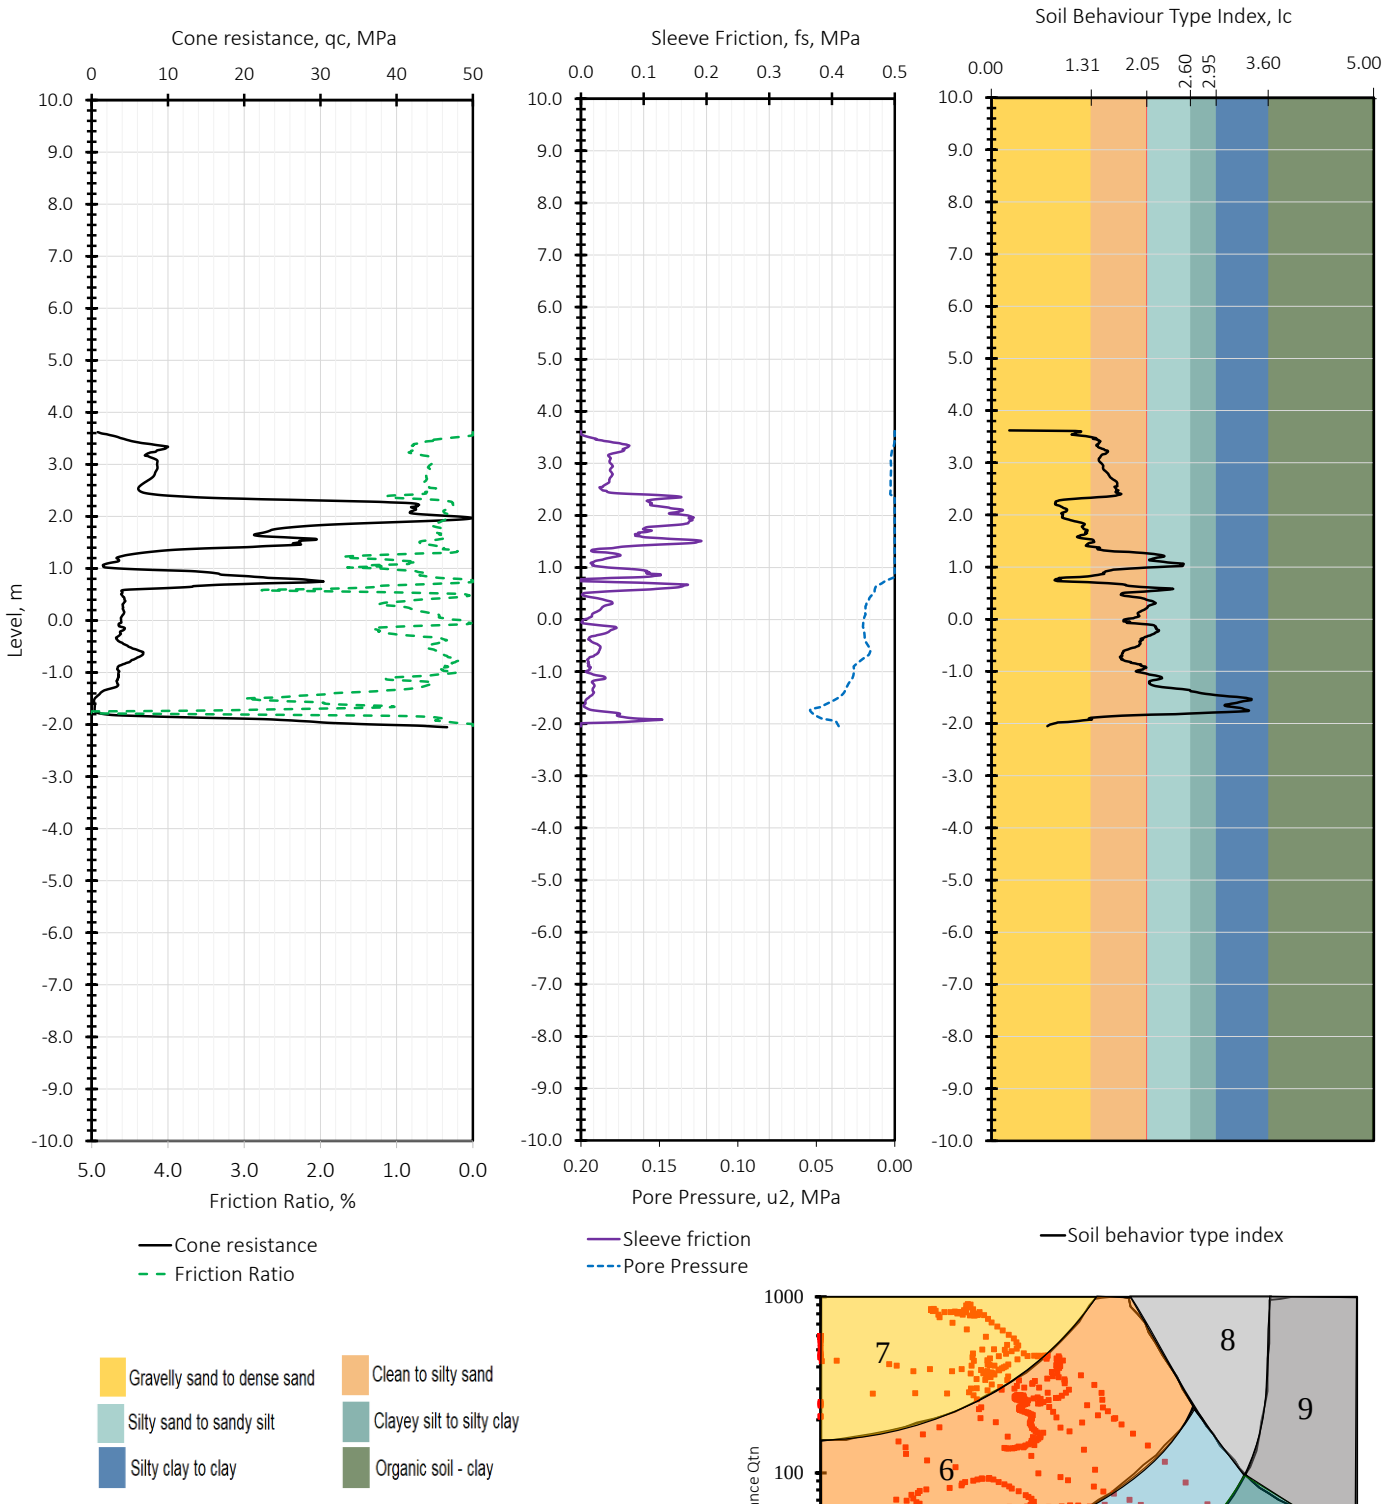

Main Contractor:	CTS GULF	
Test Location:	CPT-A1-B95-100-2	
Ground Elevation:	3.62	
	Easting	**Northing**
Coordinates:	420686.626	2927858.236
Cone ID:	DP15-CFPTxy.71431	
Test Date	7-Oct-2026	