

Client : SAUDI GLOBAL PORTS

Project : DAMMAM LOGISTICS ZONE

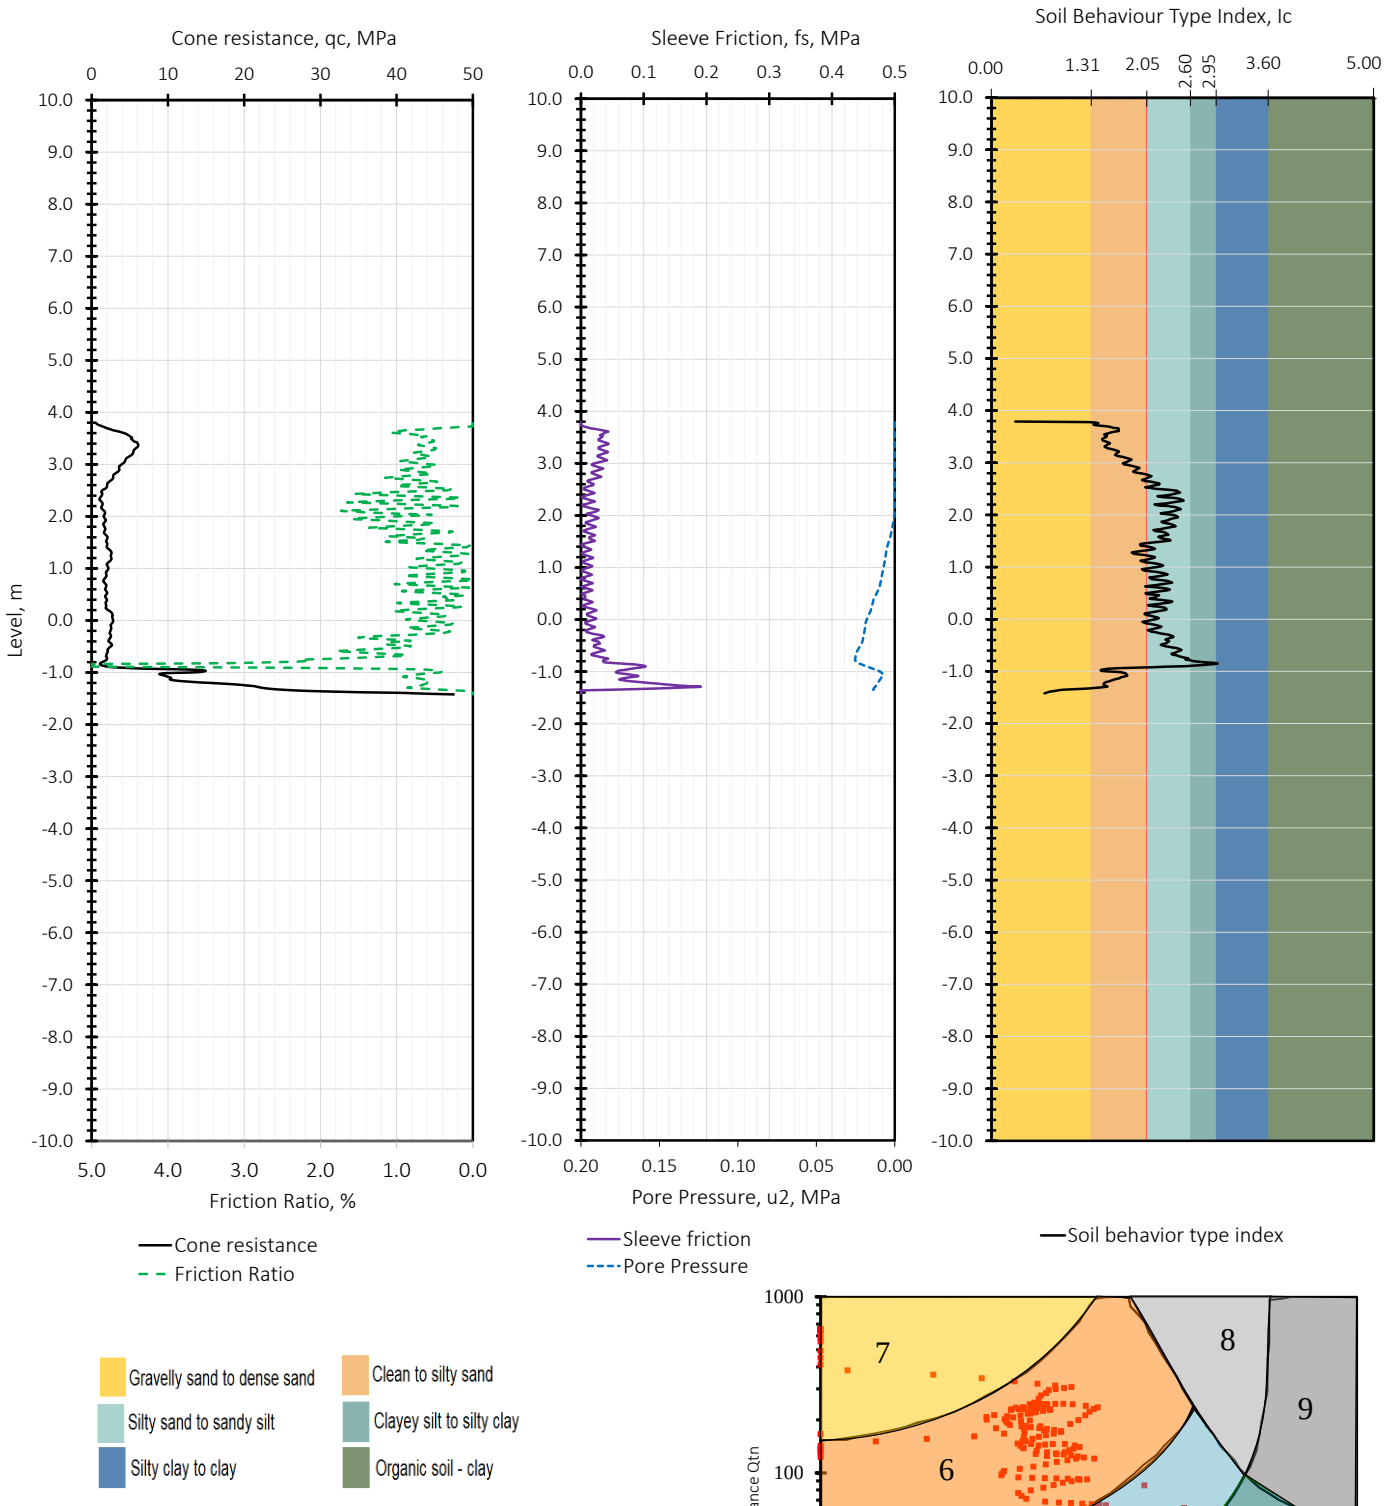

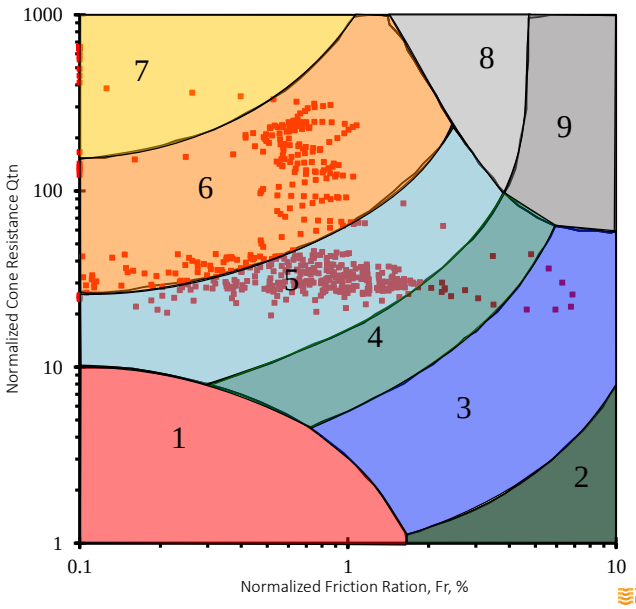

Main Contractor:	CTS GULF	
Test Location:	CPT-A1-B99-100	
Ground Elevation:	3.79	
	Easting	**Northing**
Coordinates:	420645.424	2927635.633
Cone ID:	DP15-CFPTxy.71431	
Test Date	12-Oct-2026	