

Client : SAUDI GLOBAL PORTS

Project : DAMMAM LOGISTICS ZONE

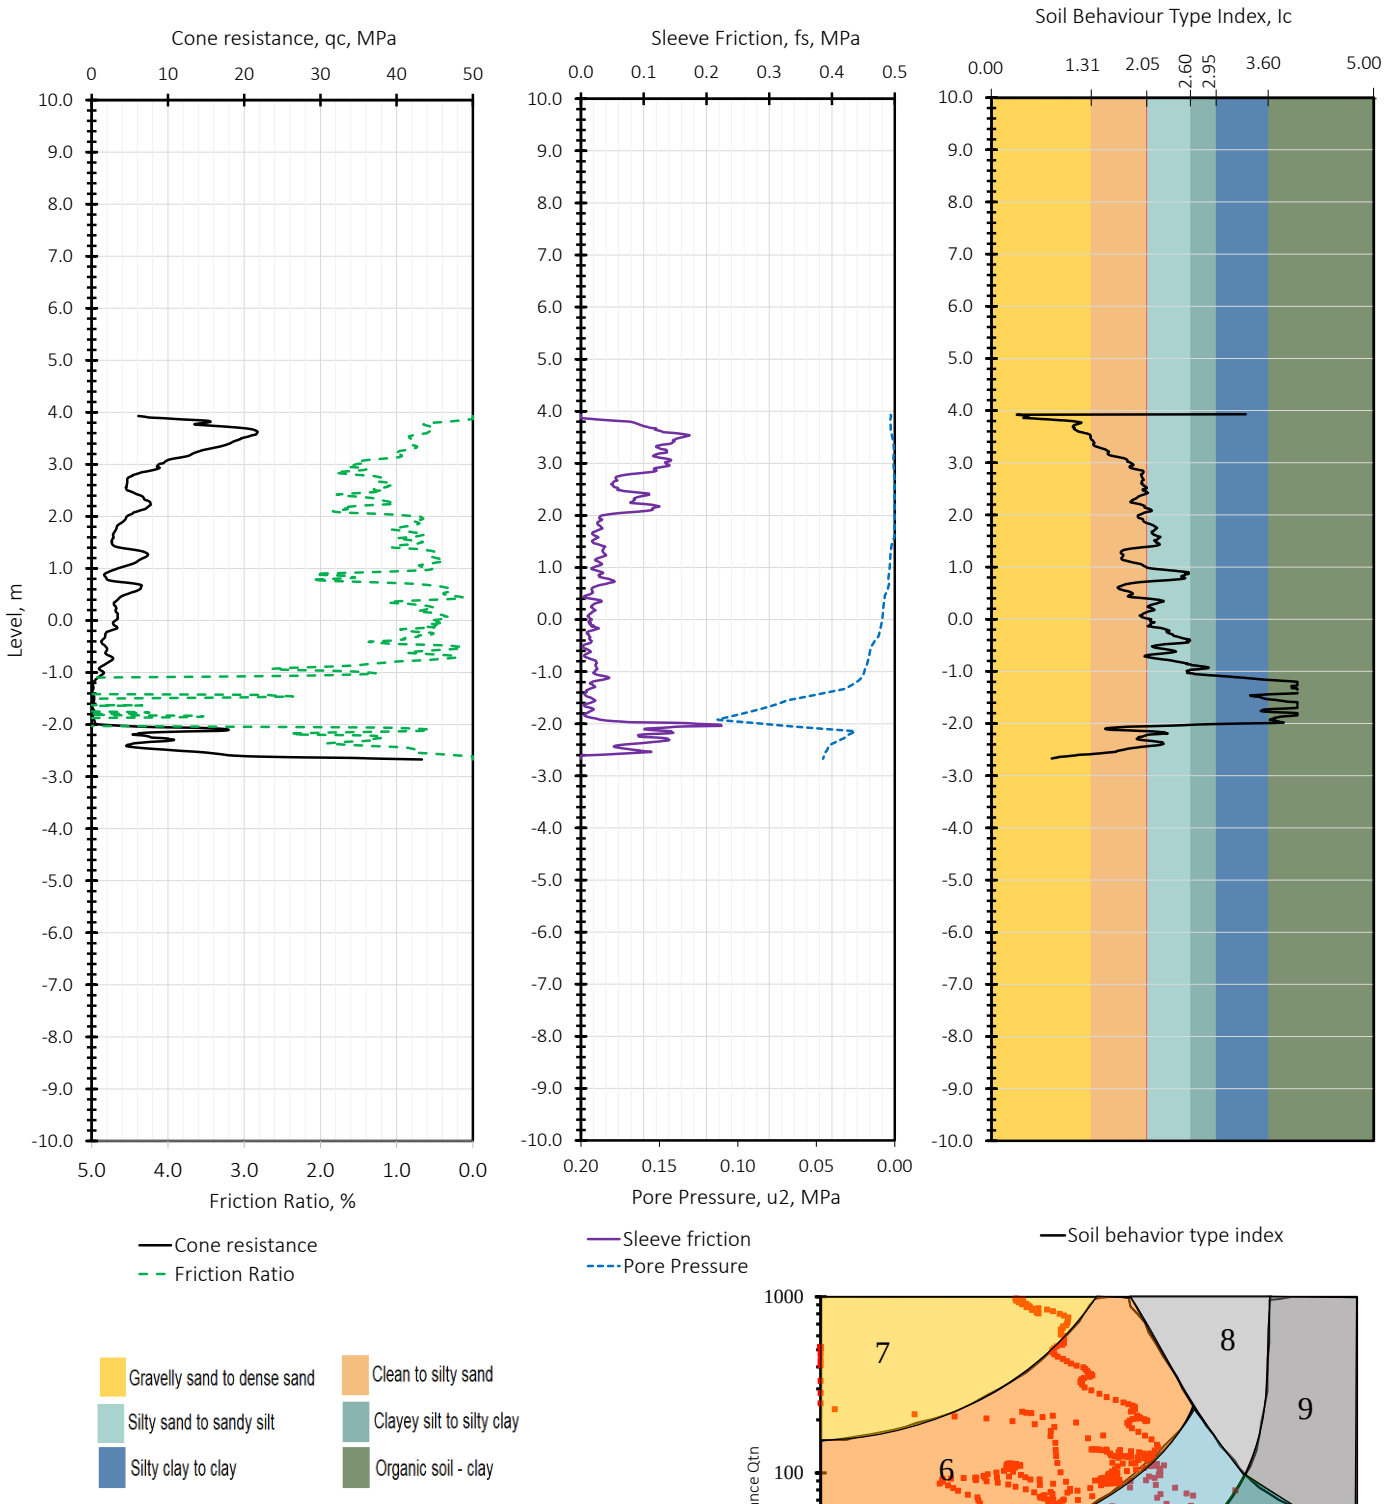

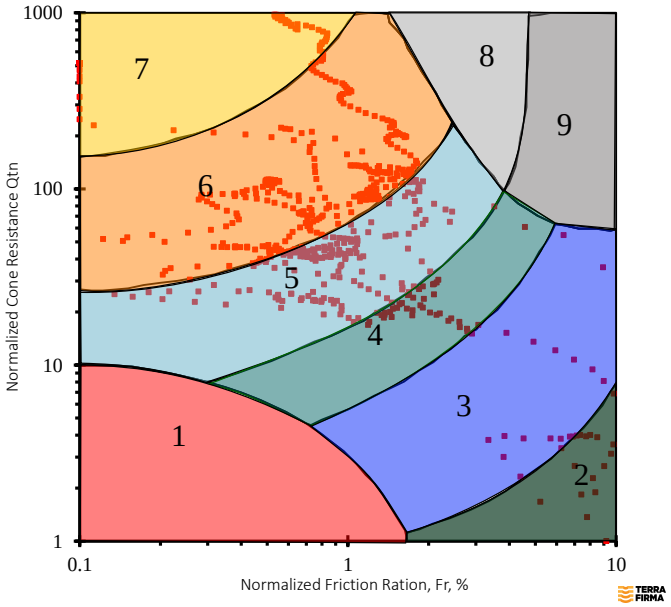

Main Contractor:	CTS GULF	
Test Location:	CPT-A2-B109-100	
Ground Elevation:	3.93	
	Easting	**Northing**
Coordinates:	421071.72	2927663.421
Cone ID:	DP15-CFPTxy.71431	
Test Date	13-Oct-2026	