
Client : SAUDI GLOBAL PORTS

Project : DAMMAM LOGISTICS ZONE

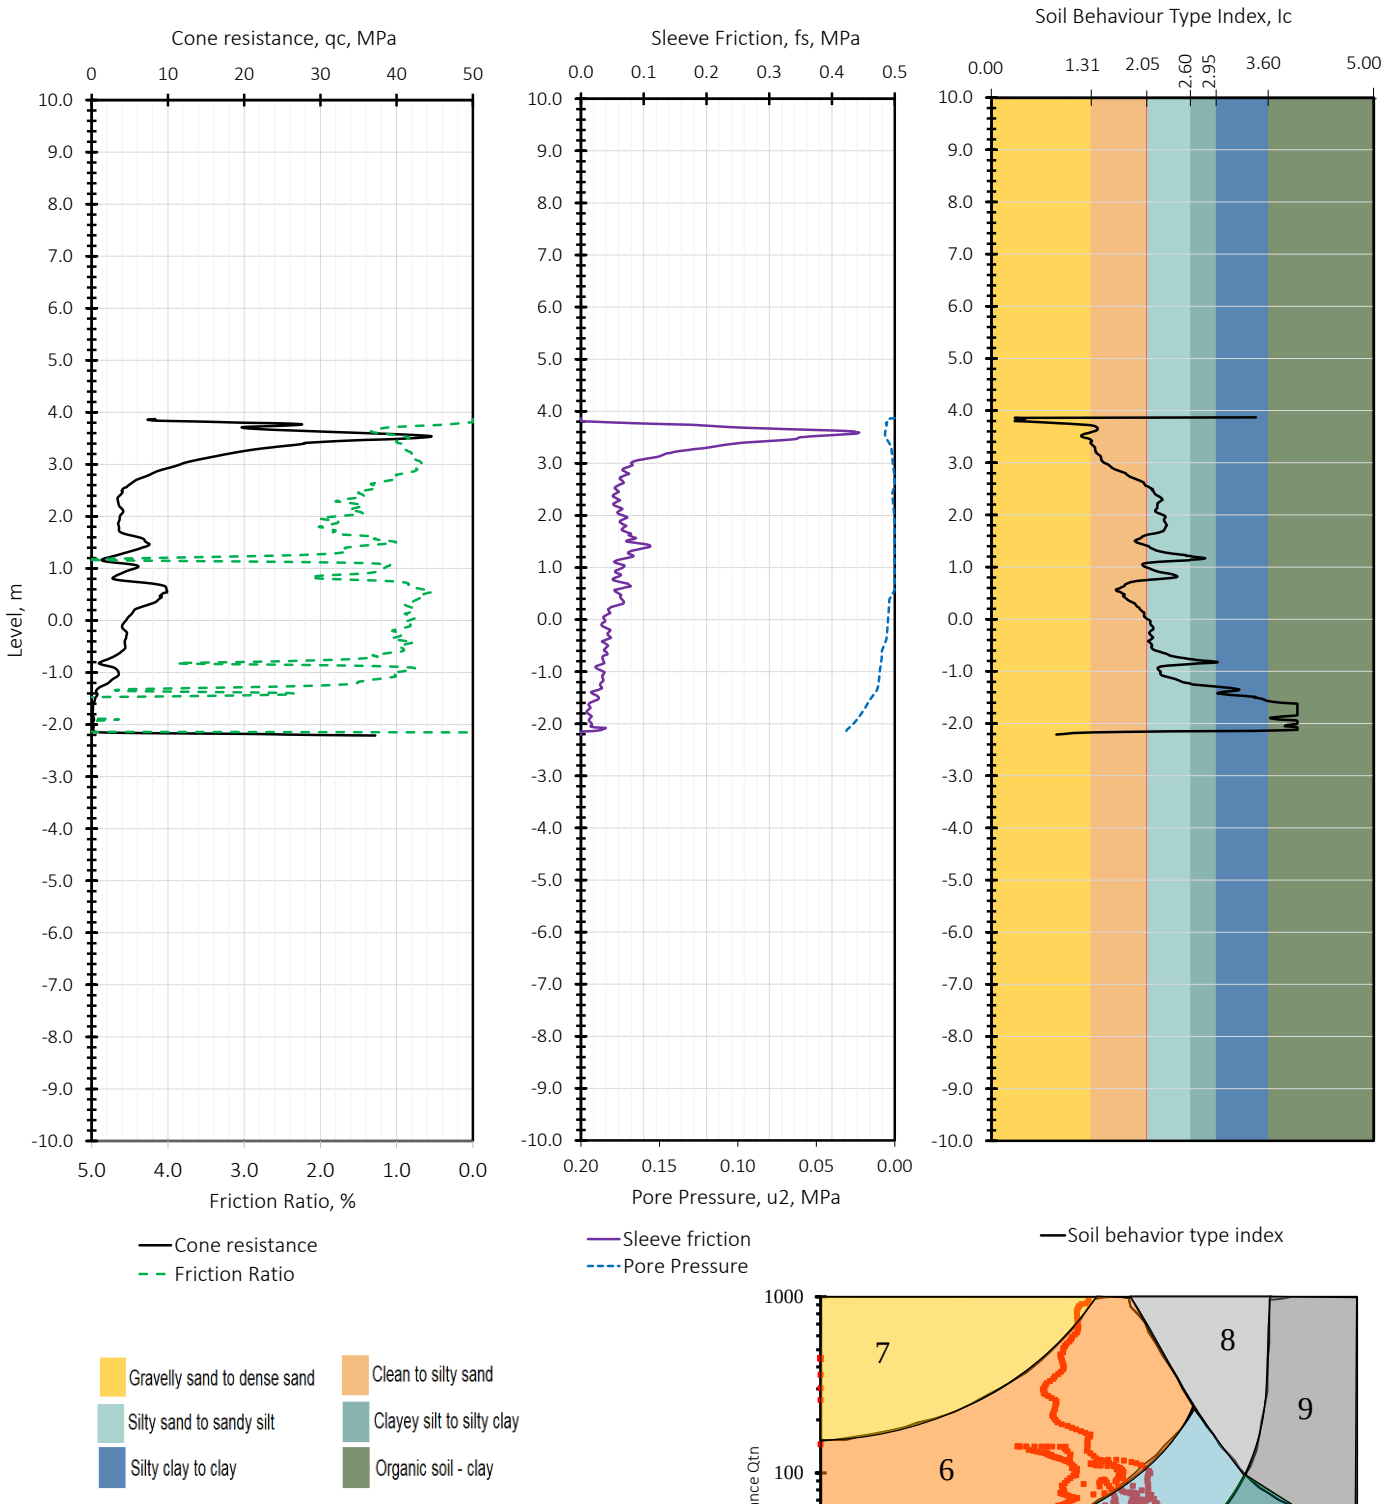

Main Contractor:	CTS GULF	
Test Location:	CPT-A2-B111-100	
Ground Elevation:	3.87	
	Easting	**Northing**
Coordinates:	421086.193	2927711.281
Cone ID:	DP15-CFPTxy.71431	
Test Date	13-Oct-2026	