
Client : SAUDI GLOBAL PORTS

Project : DAMMAM LOGISTICS ZONE

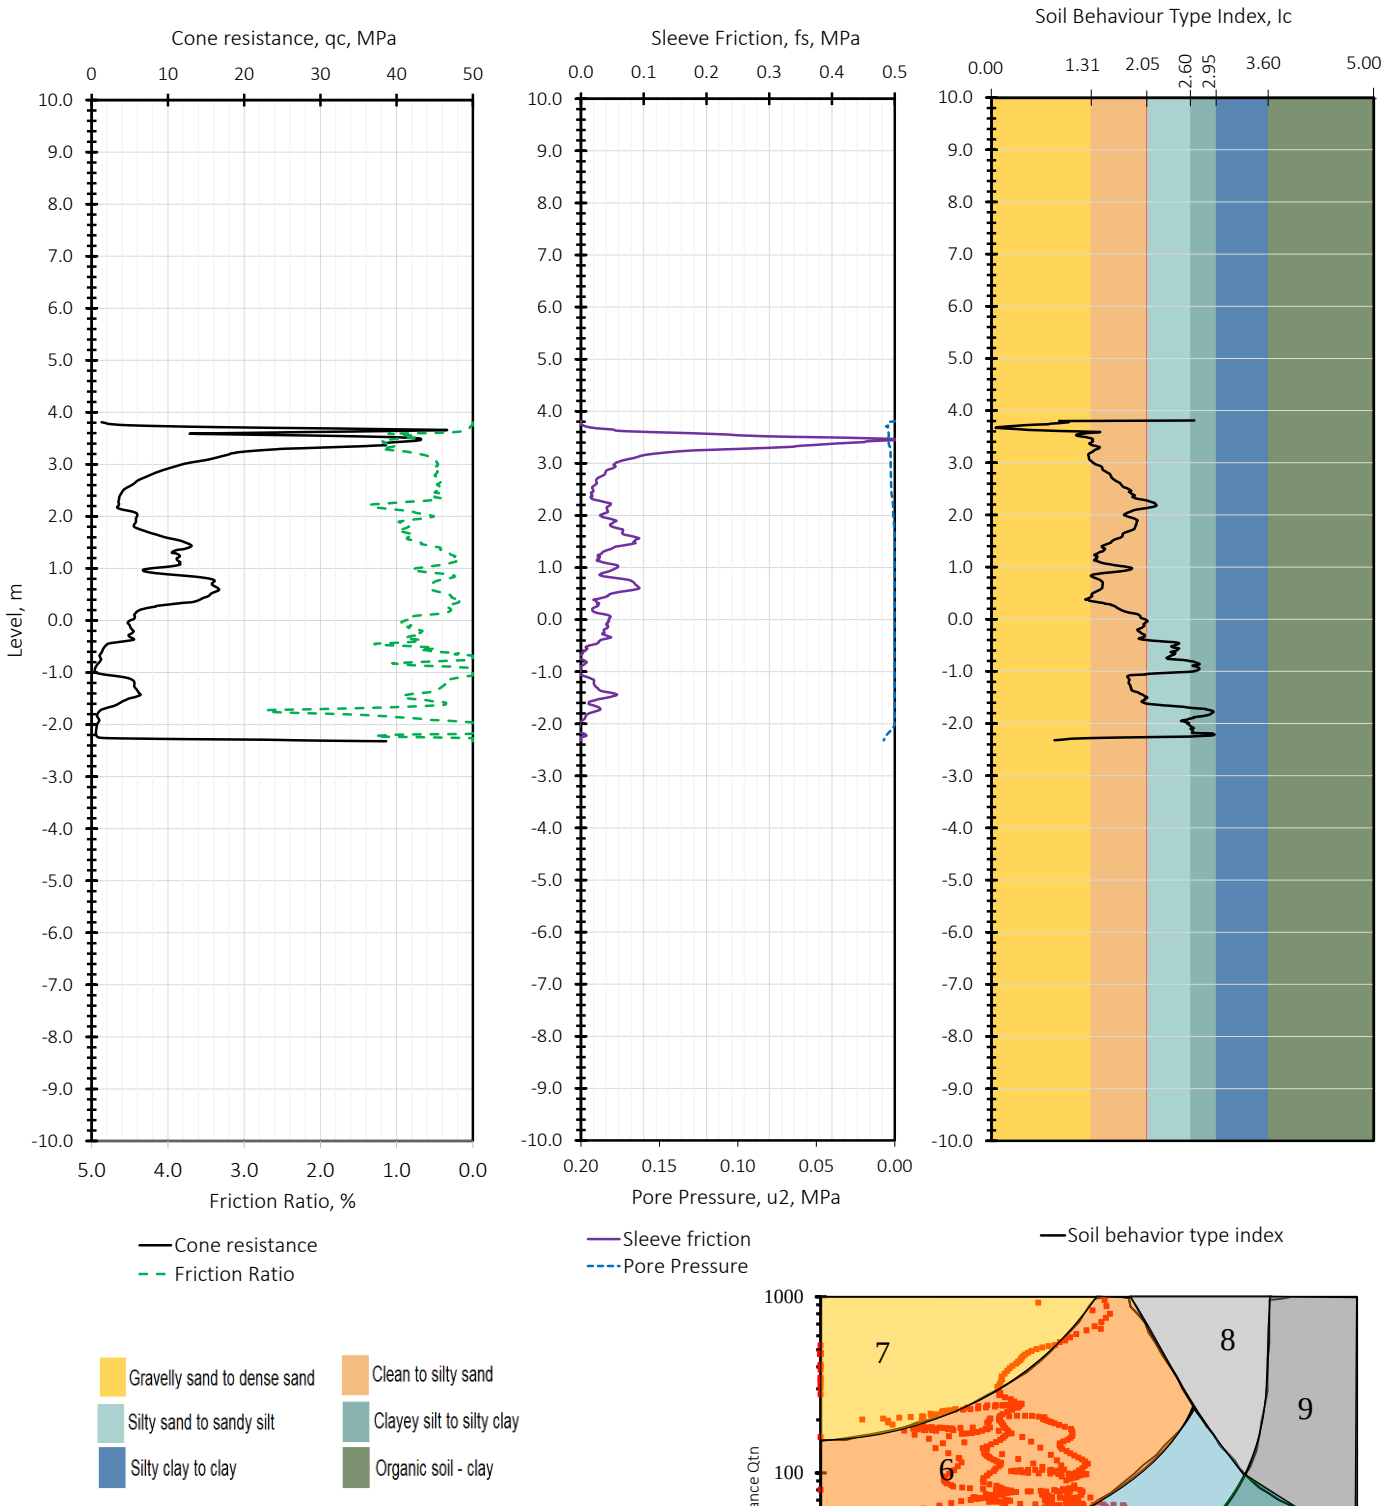

Main Contractor:	CTS GULF	
Test Location:	CPT-A2-B124-100	
Ground Elevation:	3.81	
	Easting	**Northing**
Coordinates:	421102.886	2927680.114
Cone ID:	DP15-CFPTxy.71431	
Test Date	13-Oct-2026	