

Client : SAUDI GLOBAL PORTS

Project : DAMMAM LOGISTICS ZONE

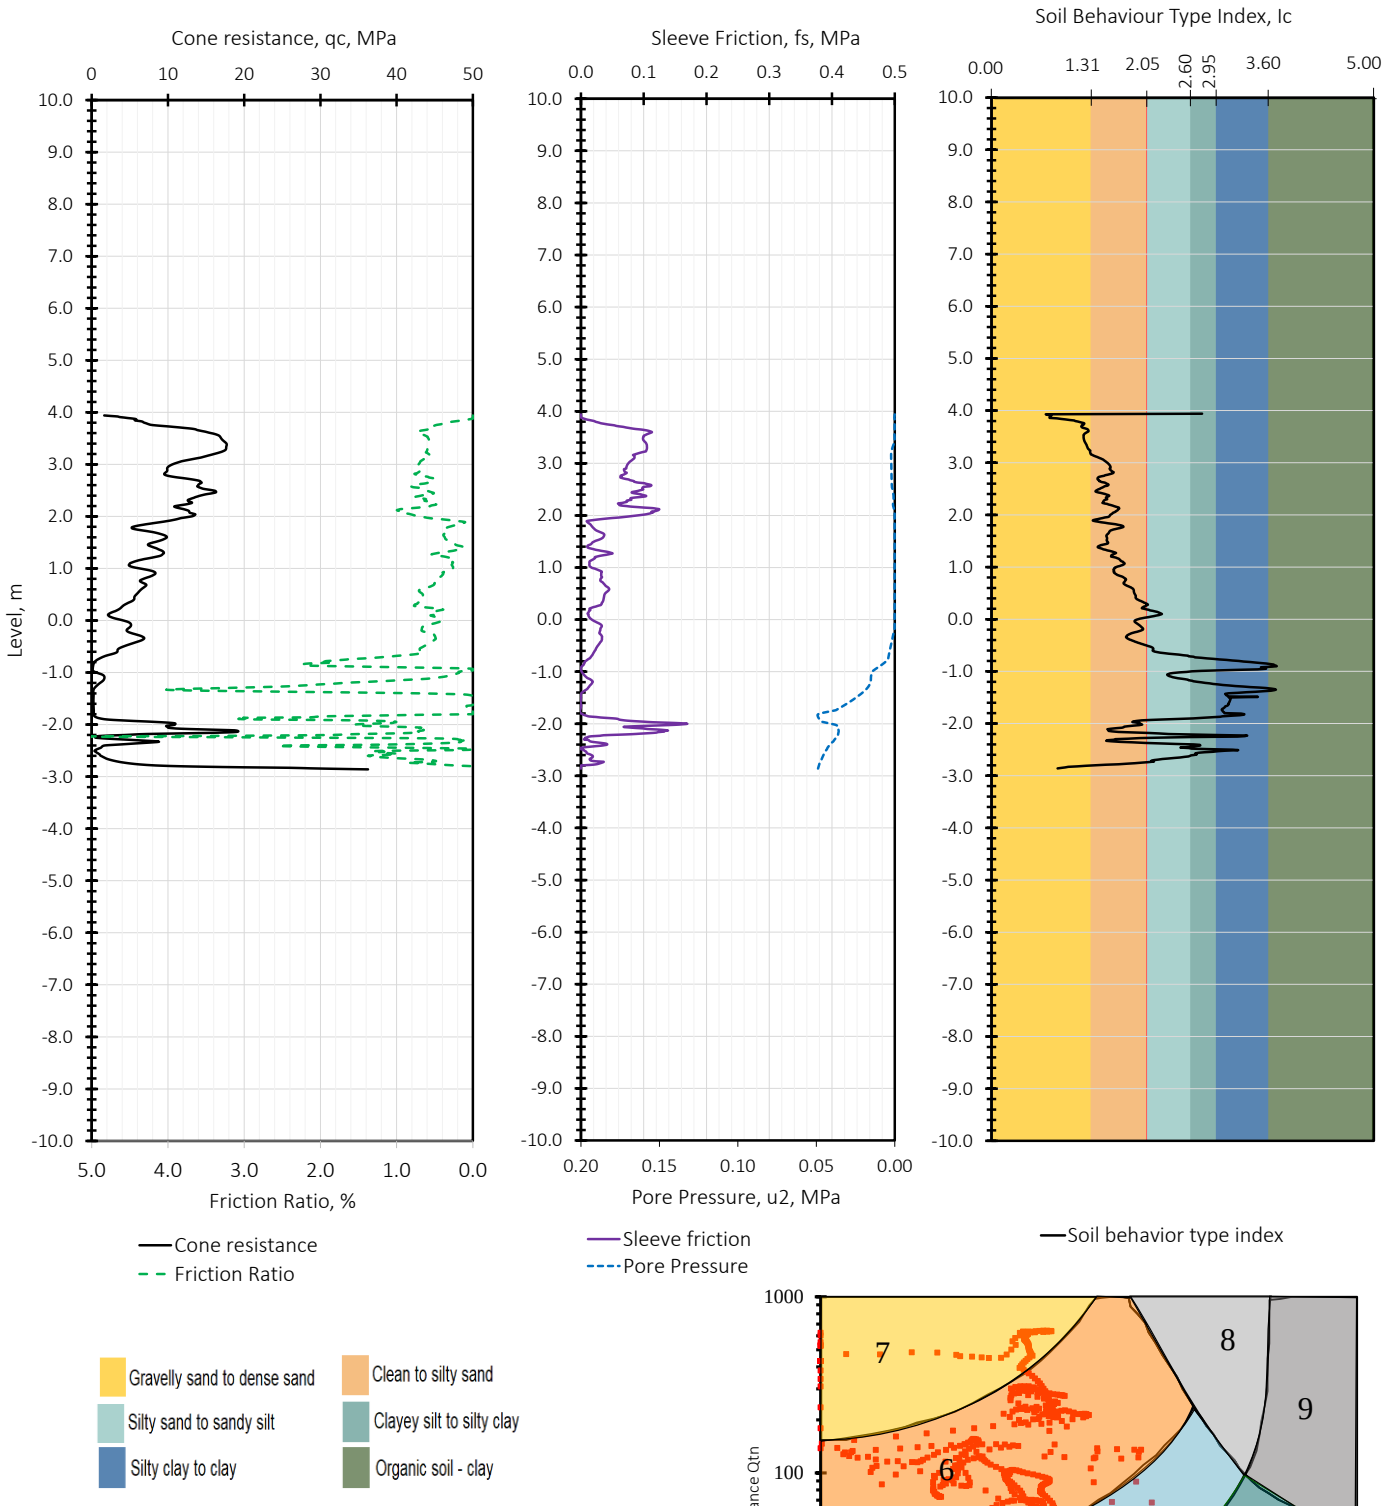

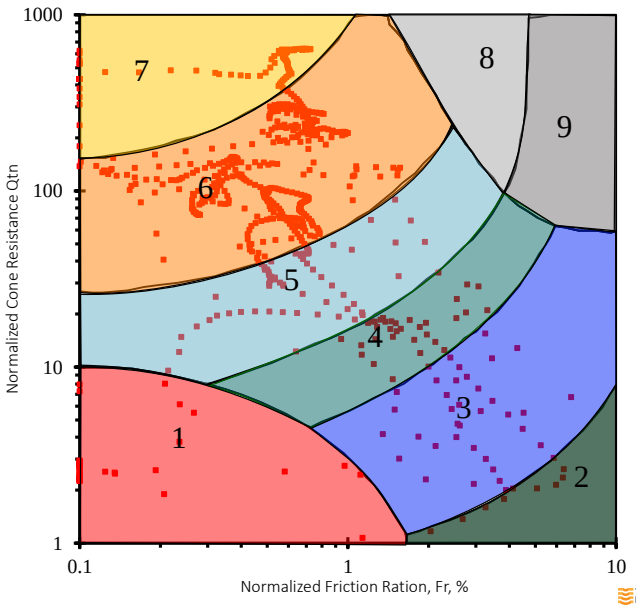

Main Contractor:	CTS GULF	
Test Location:	CPT-A2-B135-100	
Ground Elevation:	3.94	
	Easting	**Northing**
Coordinates:	421105.105	2927601.088
Cone ID:	DP15-CFPTxy.71424	
Test Date	14-Oct-2026	