
Client : SAUDI GLOBAL PORTS

Project : DAMMAM LOGISTICS ZONE

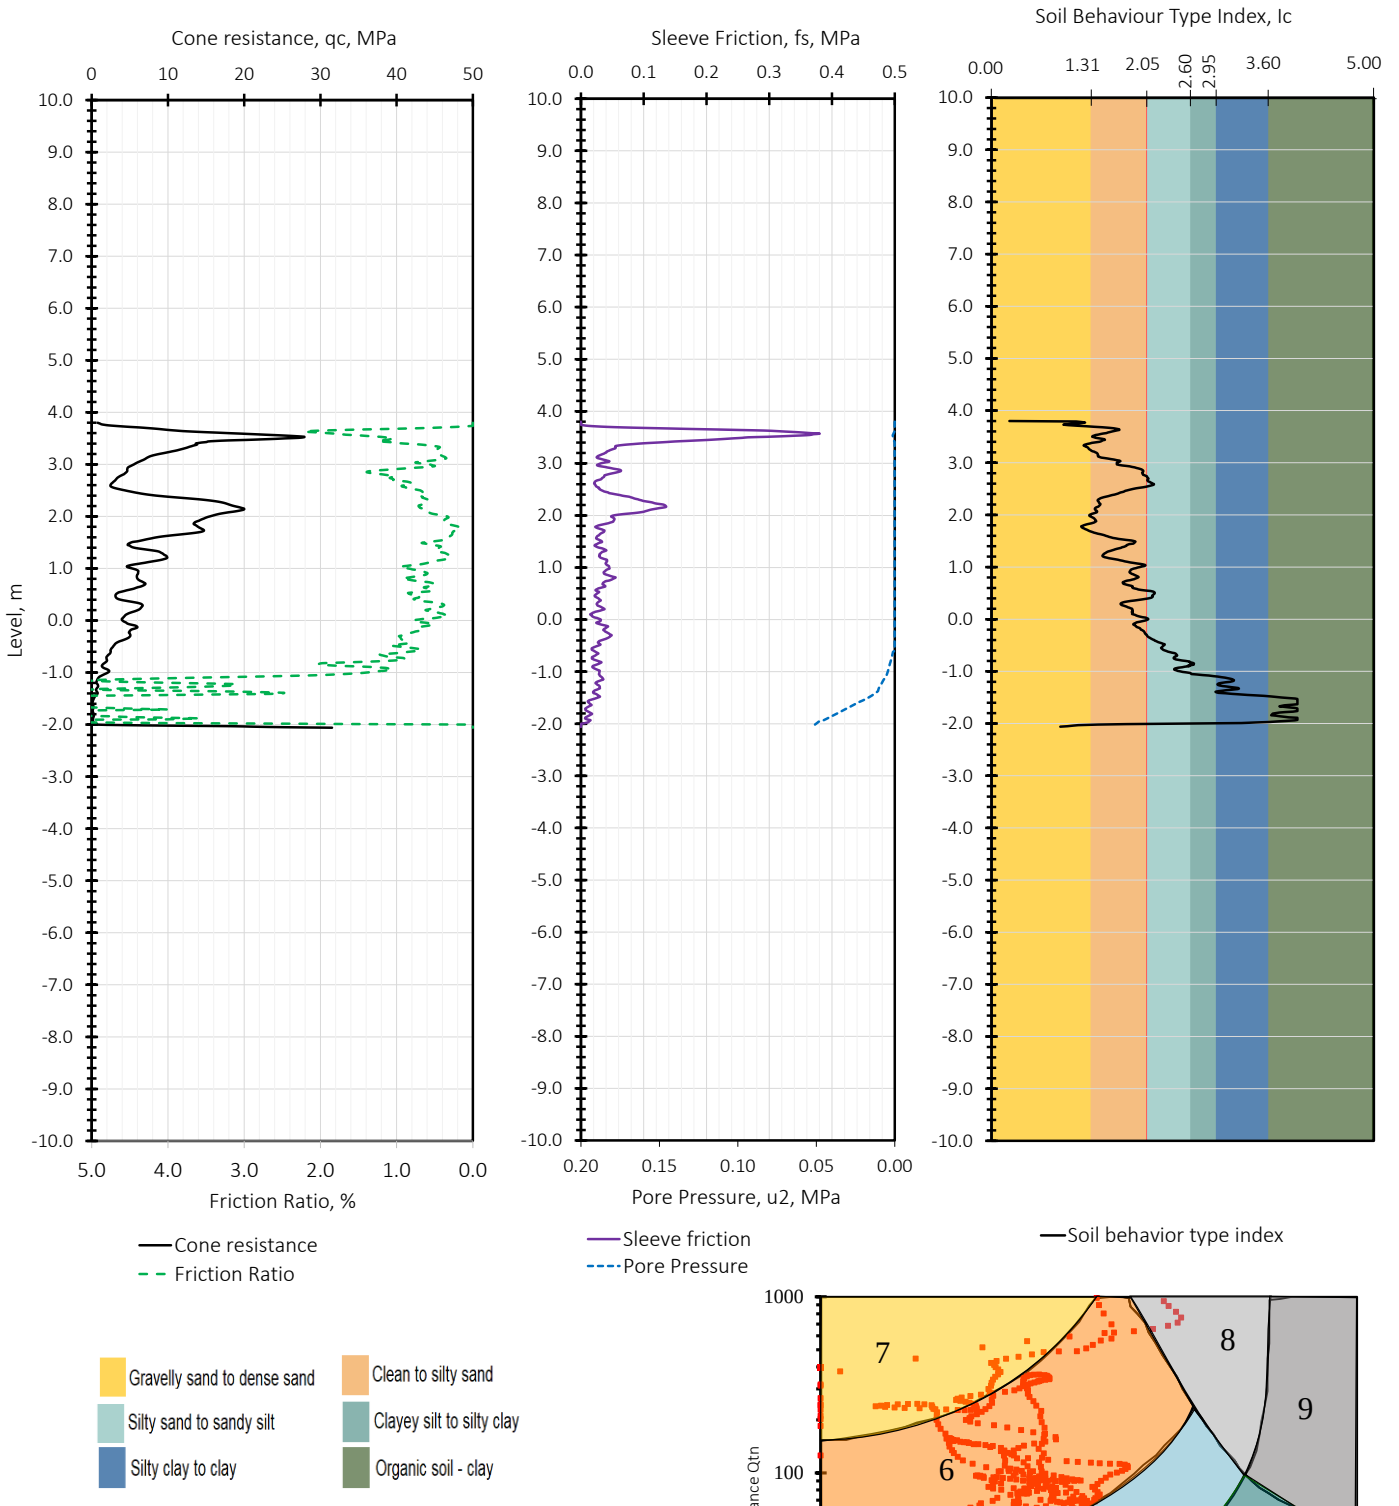

Main Contractor:	CTS GULF	
Test Location:	CPT-A2-B150-100	
Ground Elevation:	3.8	
	Easting	**Northing**
Coordinates:	421136.272	2927617.781
Cone ID:	DP15-CFPTxy.71431	
Test Date	14-Oct-2026	