

Client : SAUDI GLOBAL PORTS

Project : DAMMAM LOGISTICS ZONE

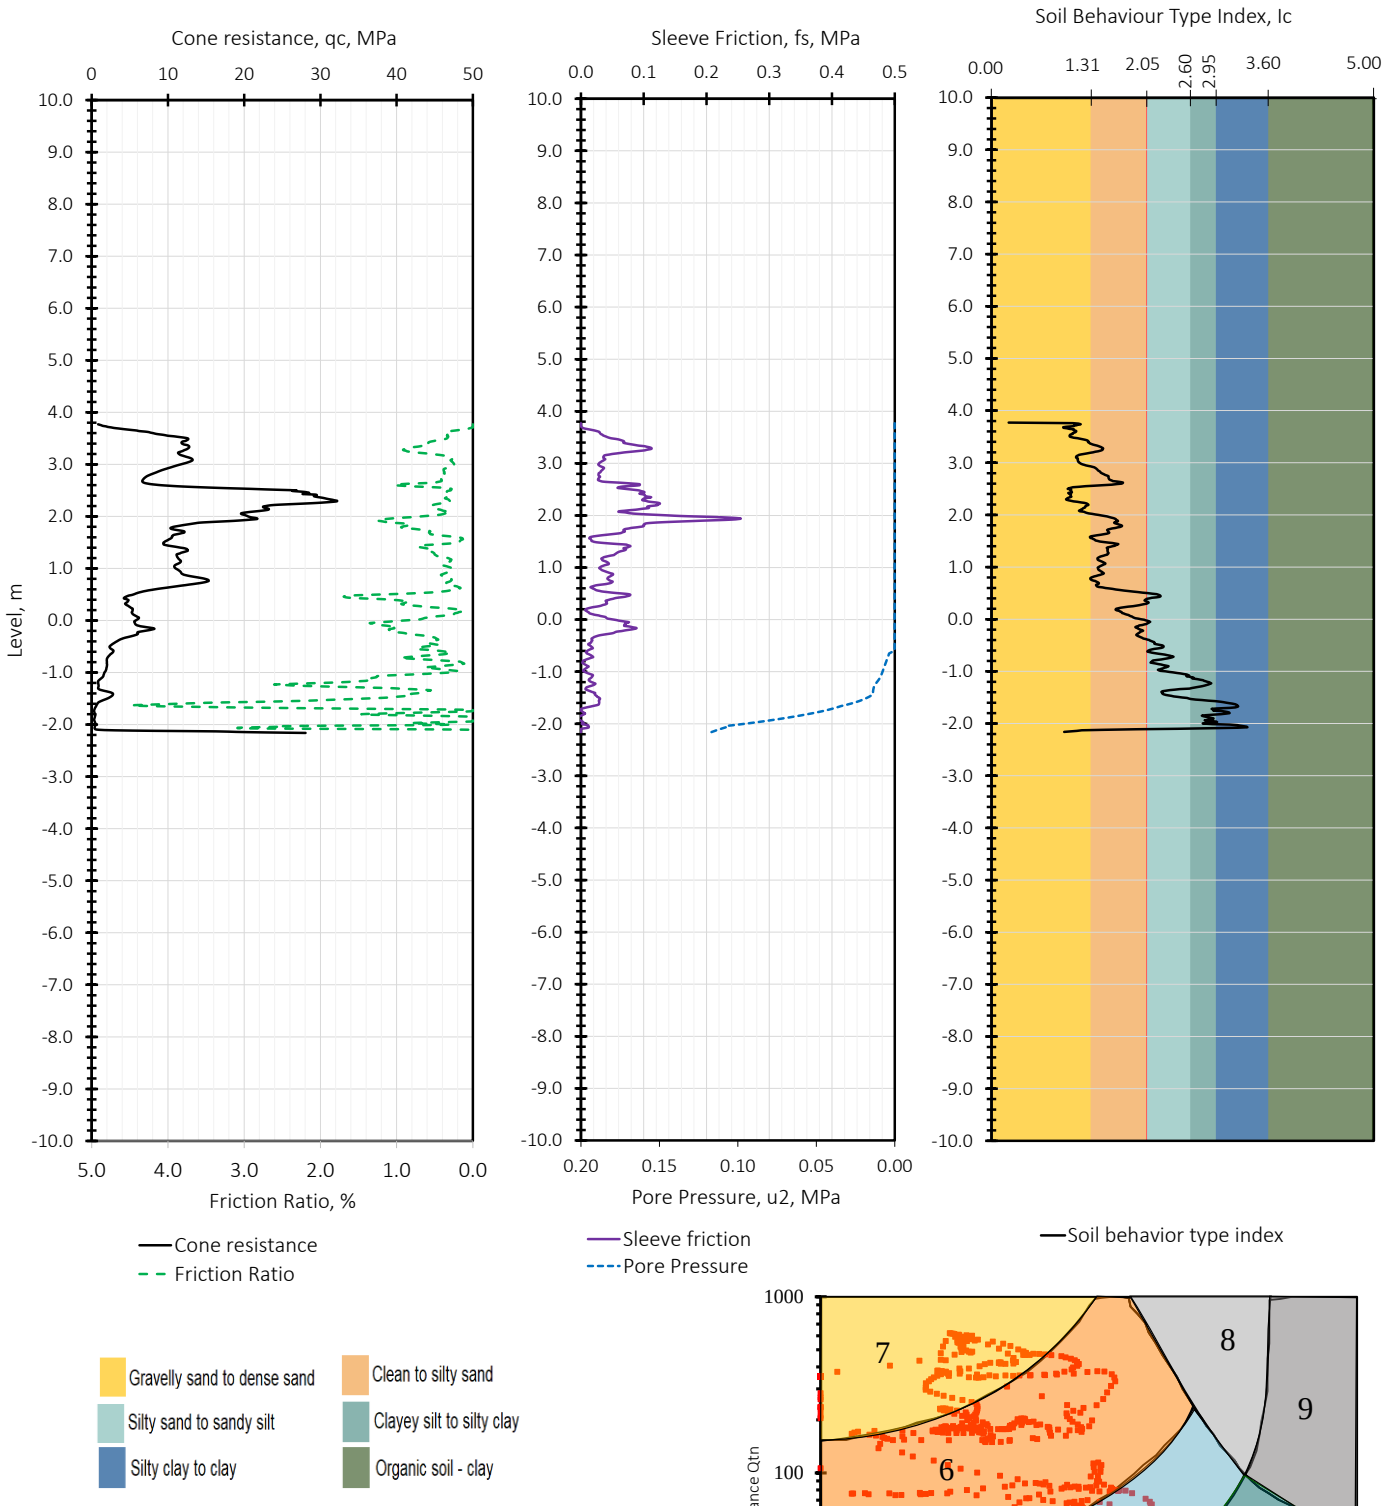

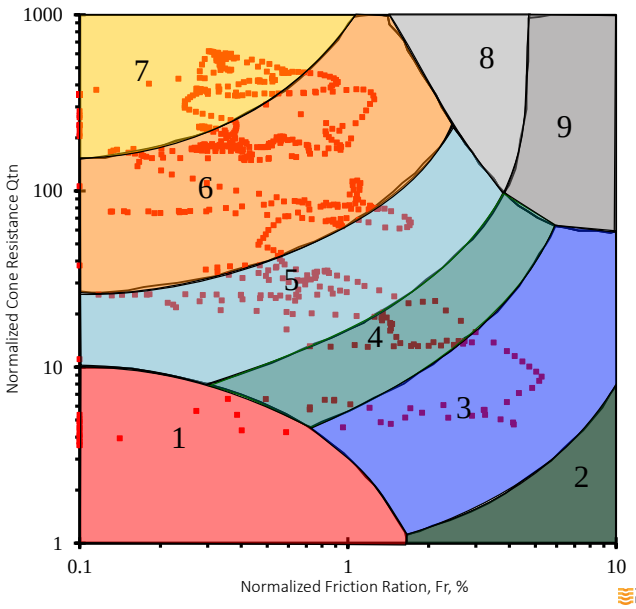

Main Contractor:	CTS GULF	
Test Location:	CPT-A2-B151-100	
Ground Elevation:	3.77	
	Easting	**Northing**
Coordinates:	421143.508	2927641.711
Cone ID:	DP15-CFPTxy.71431	
Test Date	14-Oct-2026	