

Client : SAUDI GLOBAL PORTS

Project : DAMMAM LOGISTICS ZONE

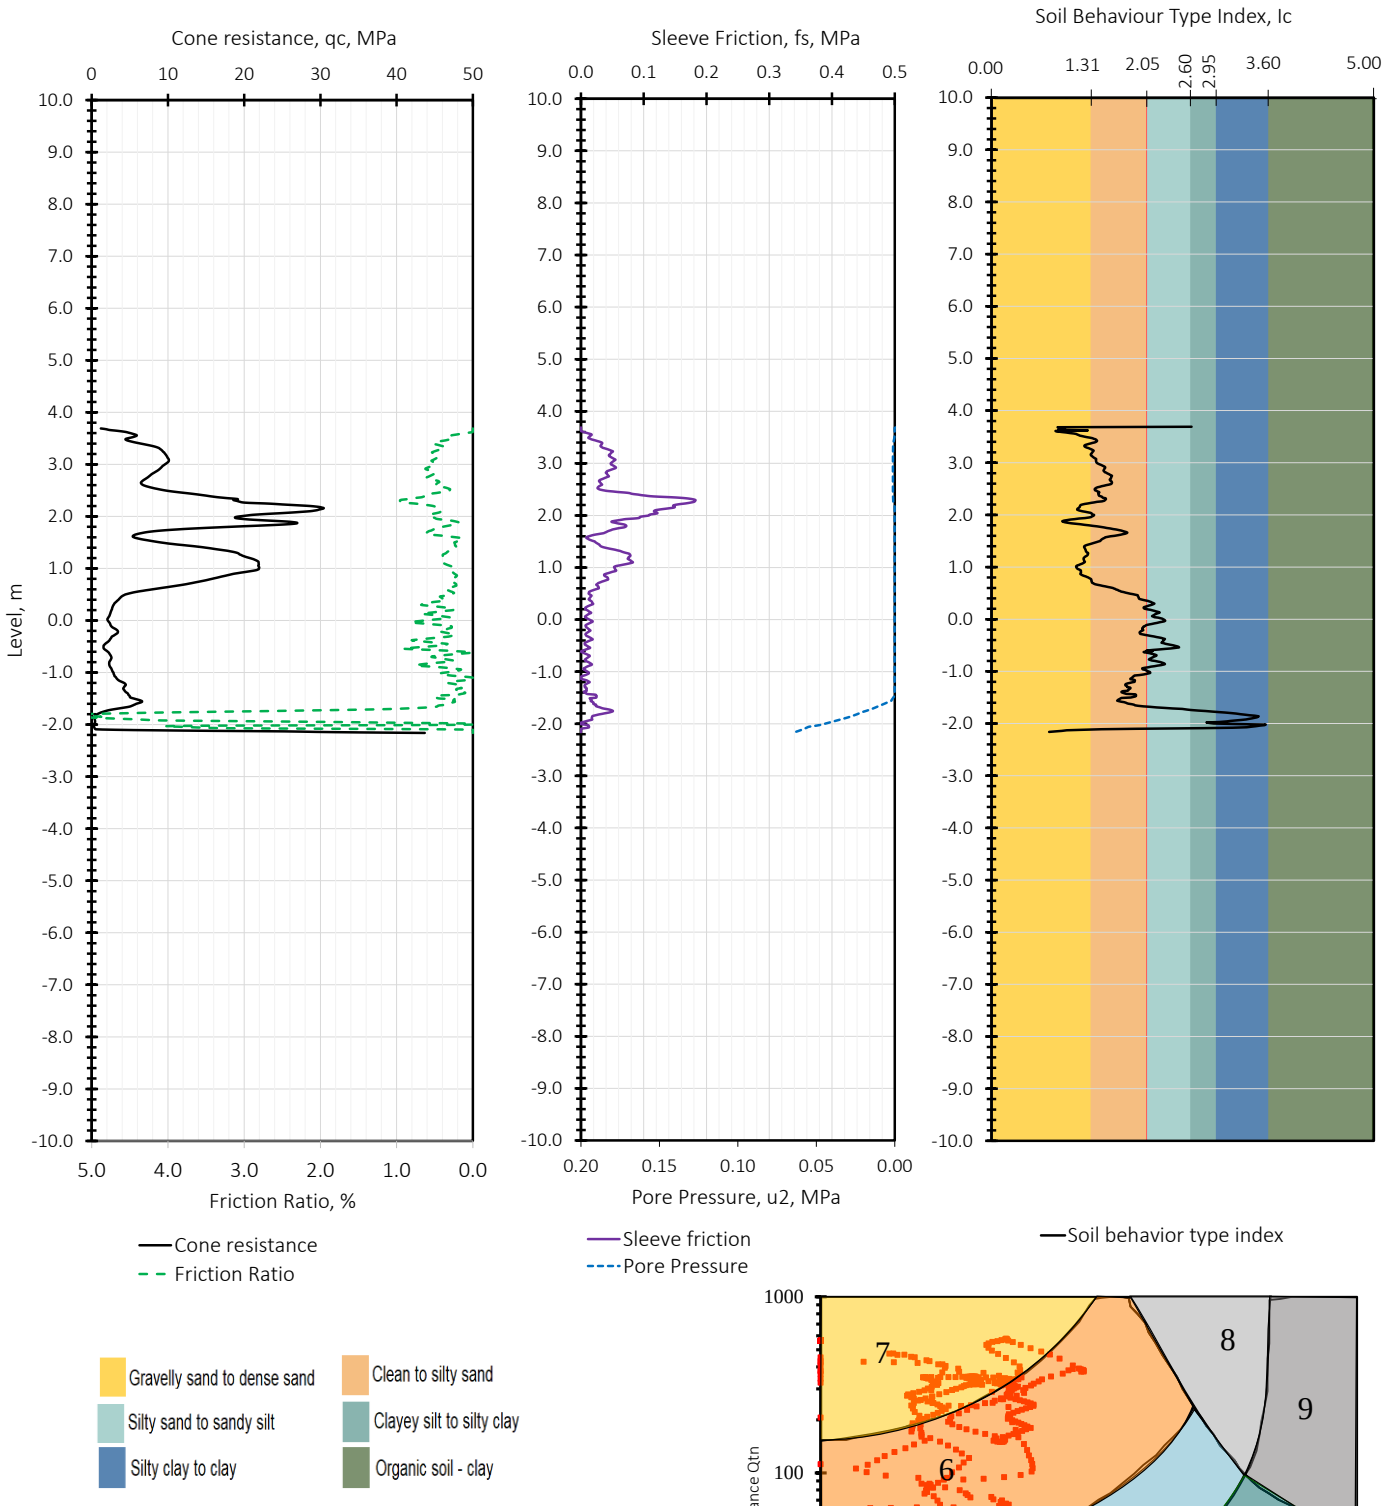

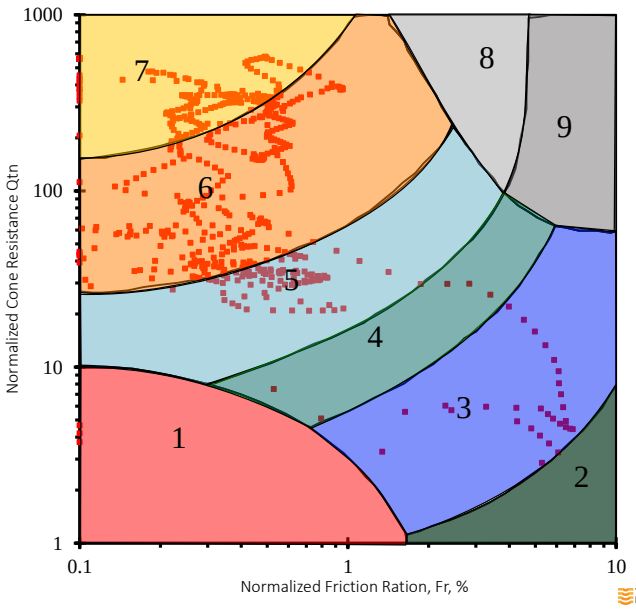

Main Contractor:	CTS GULF	
Test Location:	CPT-A2-B152-100	
Ground Elevation:	3.69	
	Easting	**Northing**
Coordinates:	421150.745	2927665.641
Cone ID:	DP15-CFPTxy.71431	
Test Date	14-Oct-2026	