

Client : SAUDI GLOBAL PORTS

Project : DAMMAM LOGISTICS ZONE

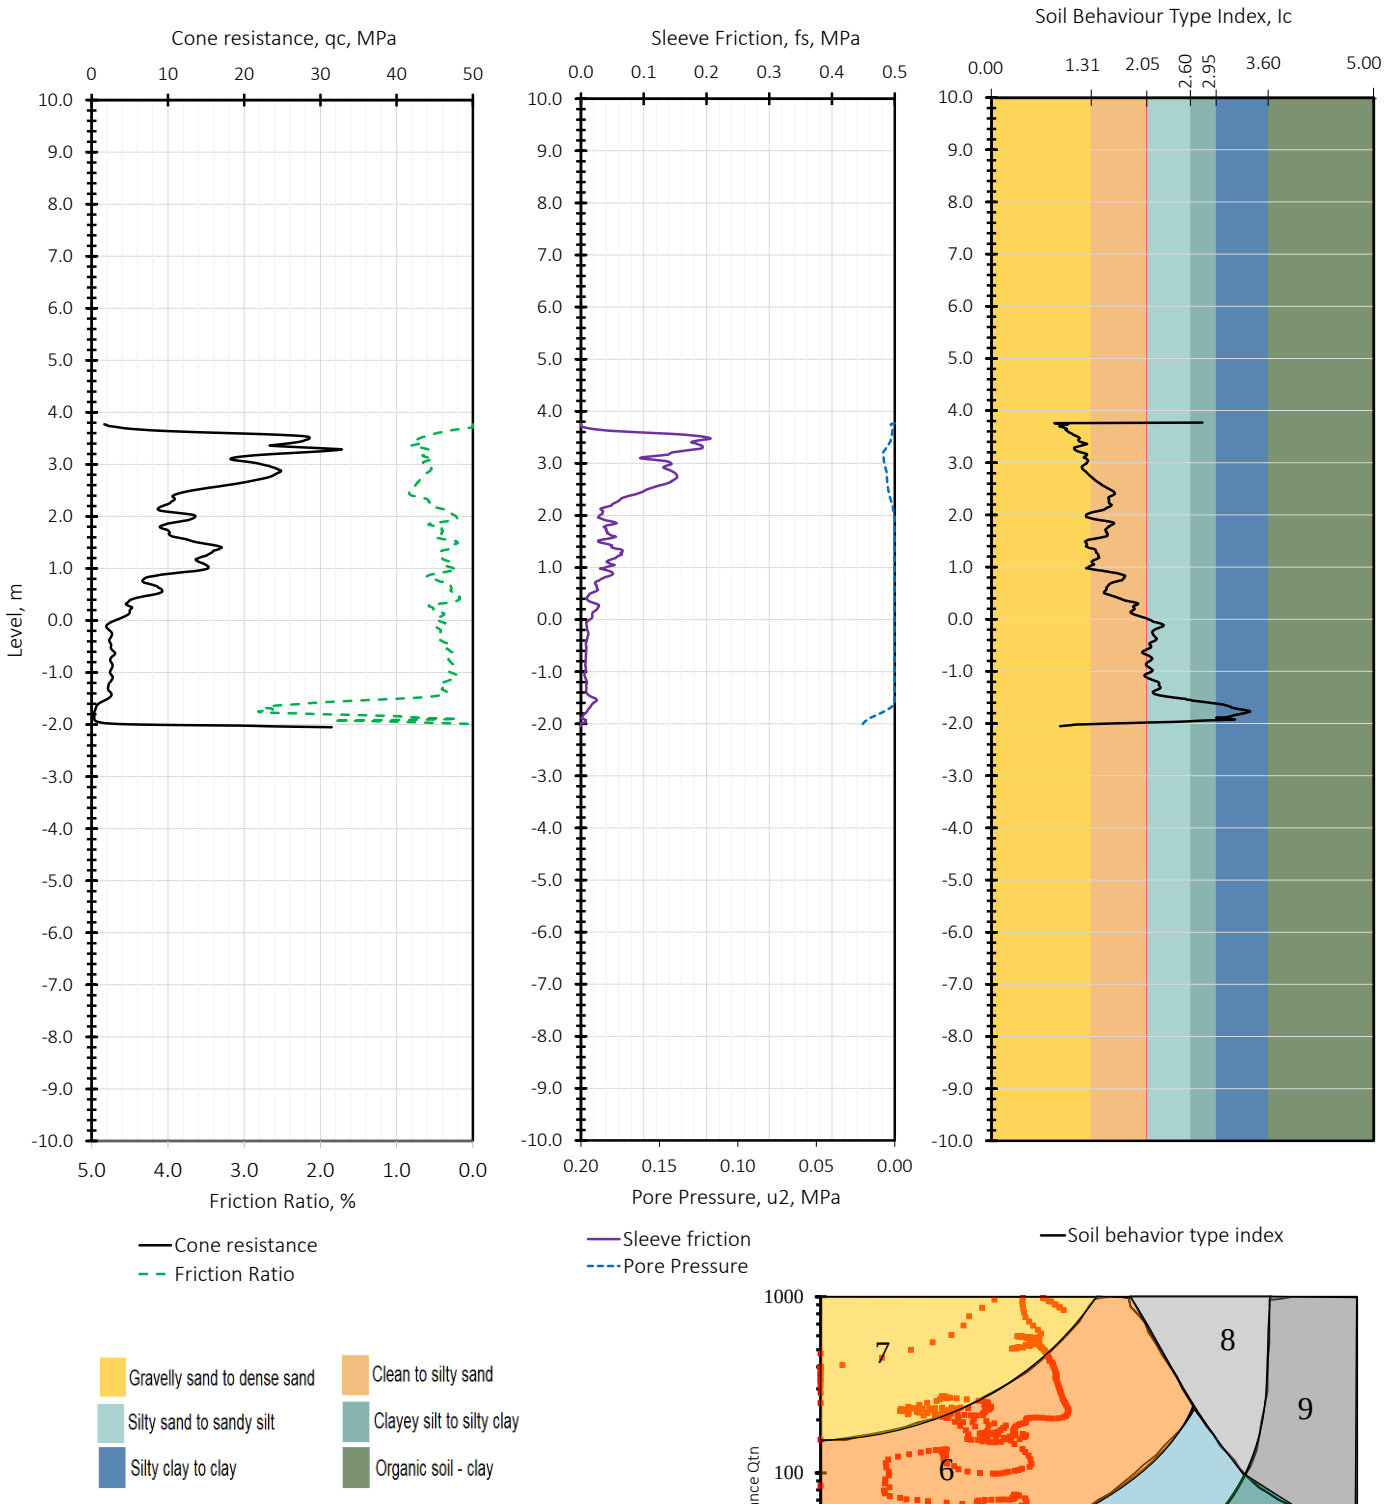

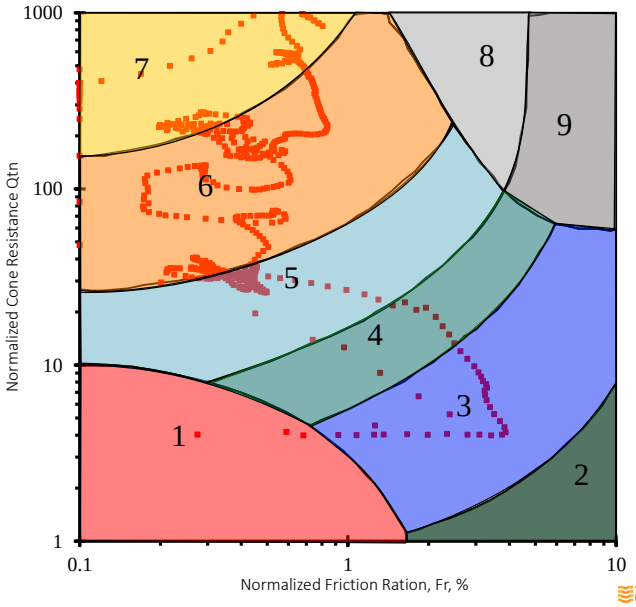

Main Contractor:	CTS GULF	
Test Location:	CPT-A2-B162-100	
Ground Elevation:	3.77	
	Easting	**Northing**
Coordinates:	42145.728	2927562.685
Cone ID:	DP15-CFPTxy.71424	
Test Date	14-Oct-2026	