

Client : SAUDI GLOBAL PORTS

Project : DAMMAM LOGISTICS ZONE

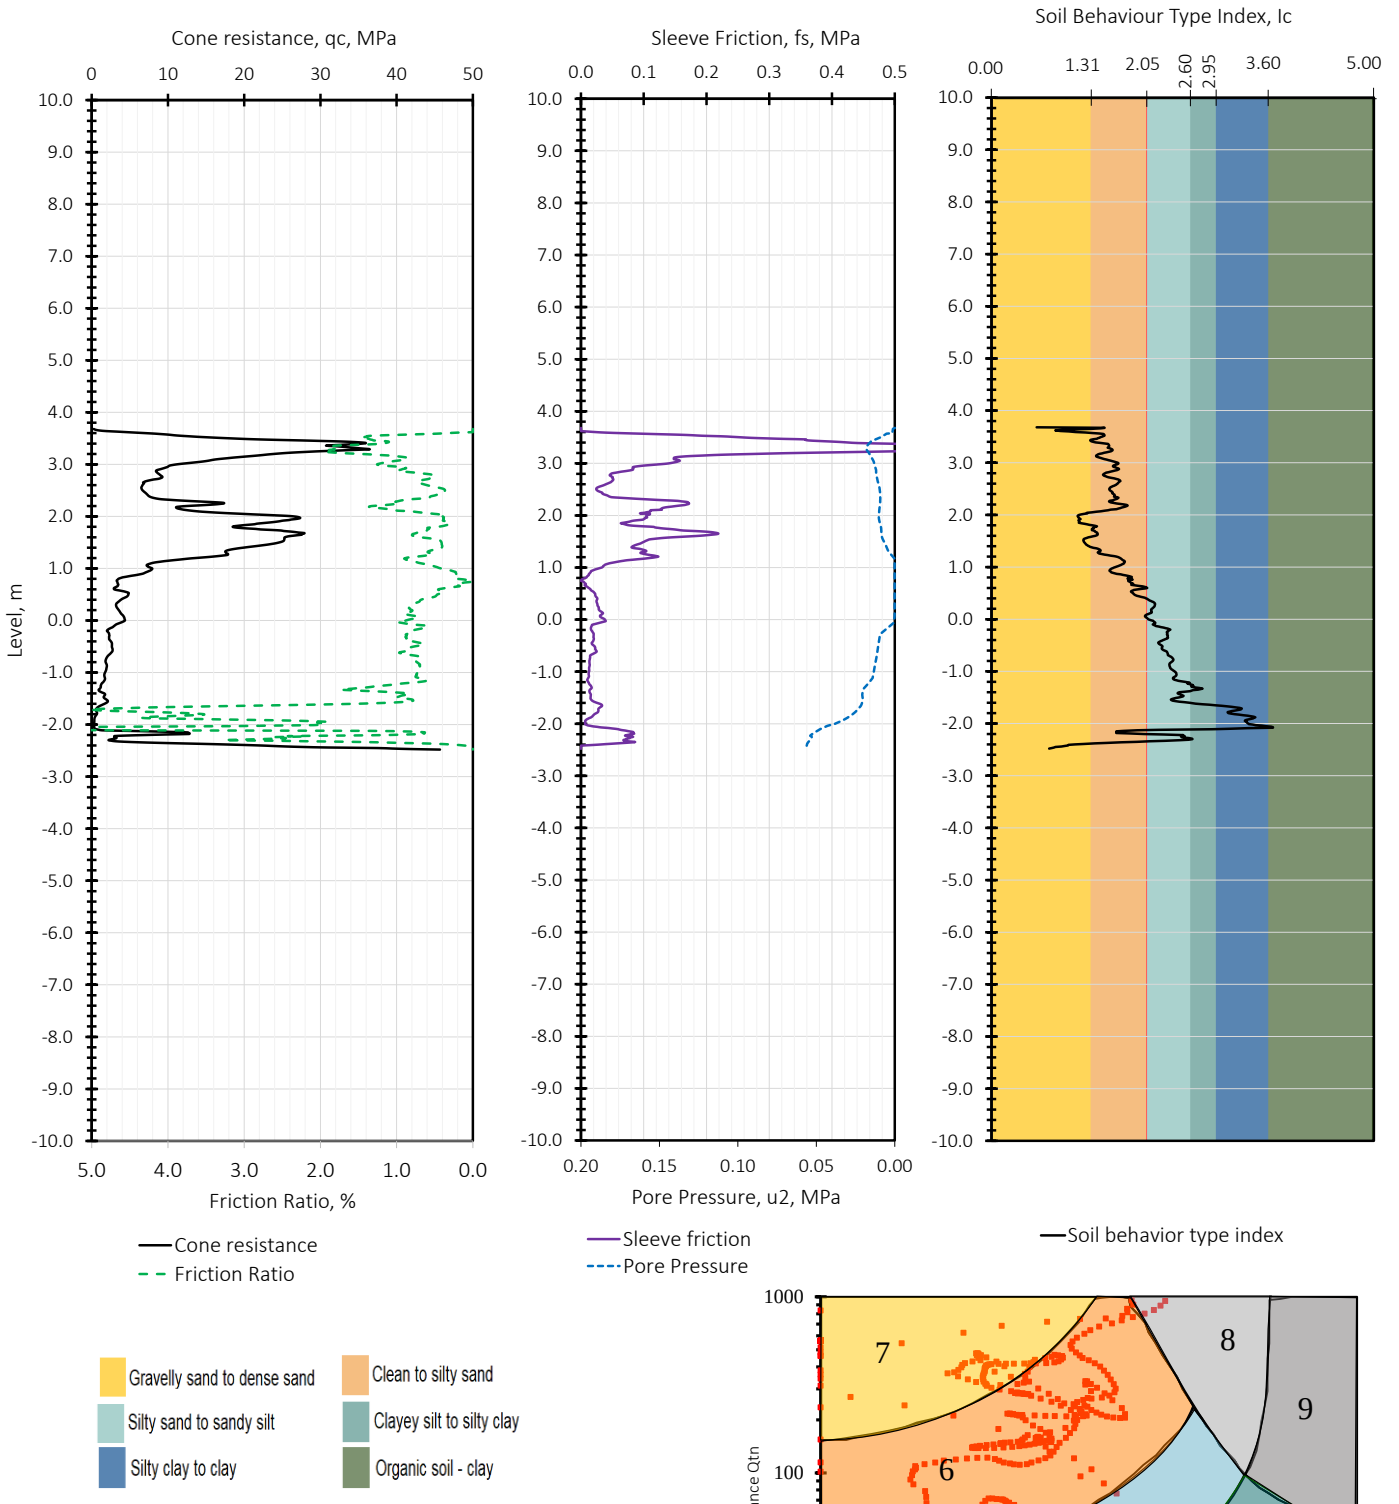

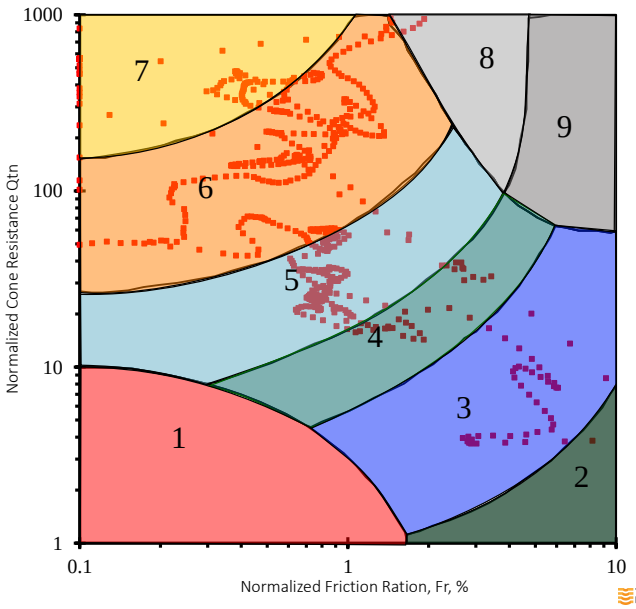

Main Contractor:	CTS GULF	
Test Location:	CPT-A2-B166-100	
Ground Elevation:	3.68	
	Easting	**Northing**
Coordinates:	421174.675	2927658.404
Cone ID:	DP15-CFPTxy.71424	
Test Date	14-Oct-2026	