

Client : SAUDI GLOBAL PORTS

Project : DAMMAM LOGISTICS ZONE

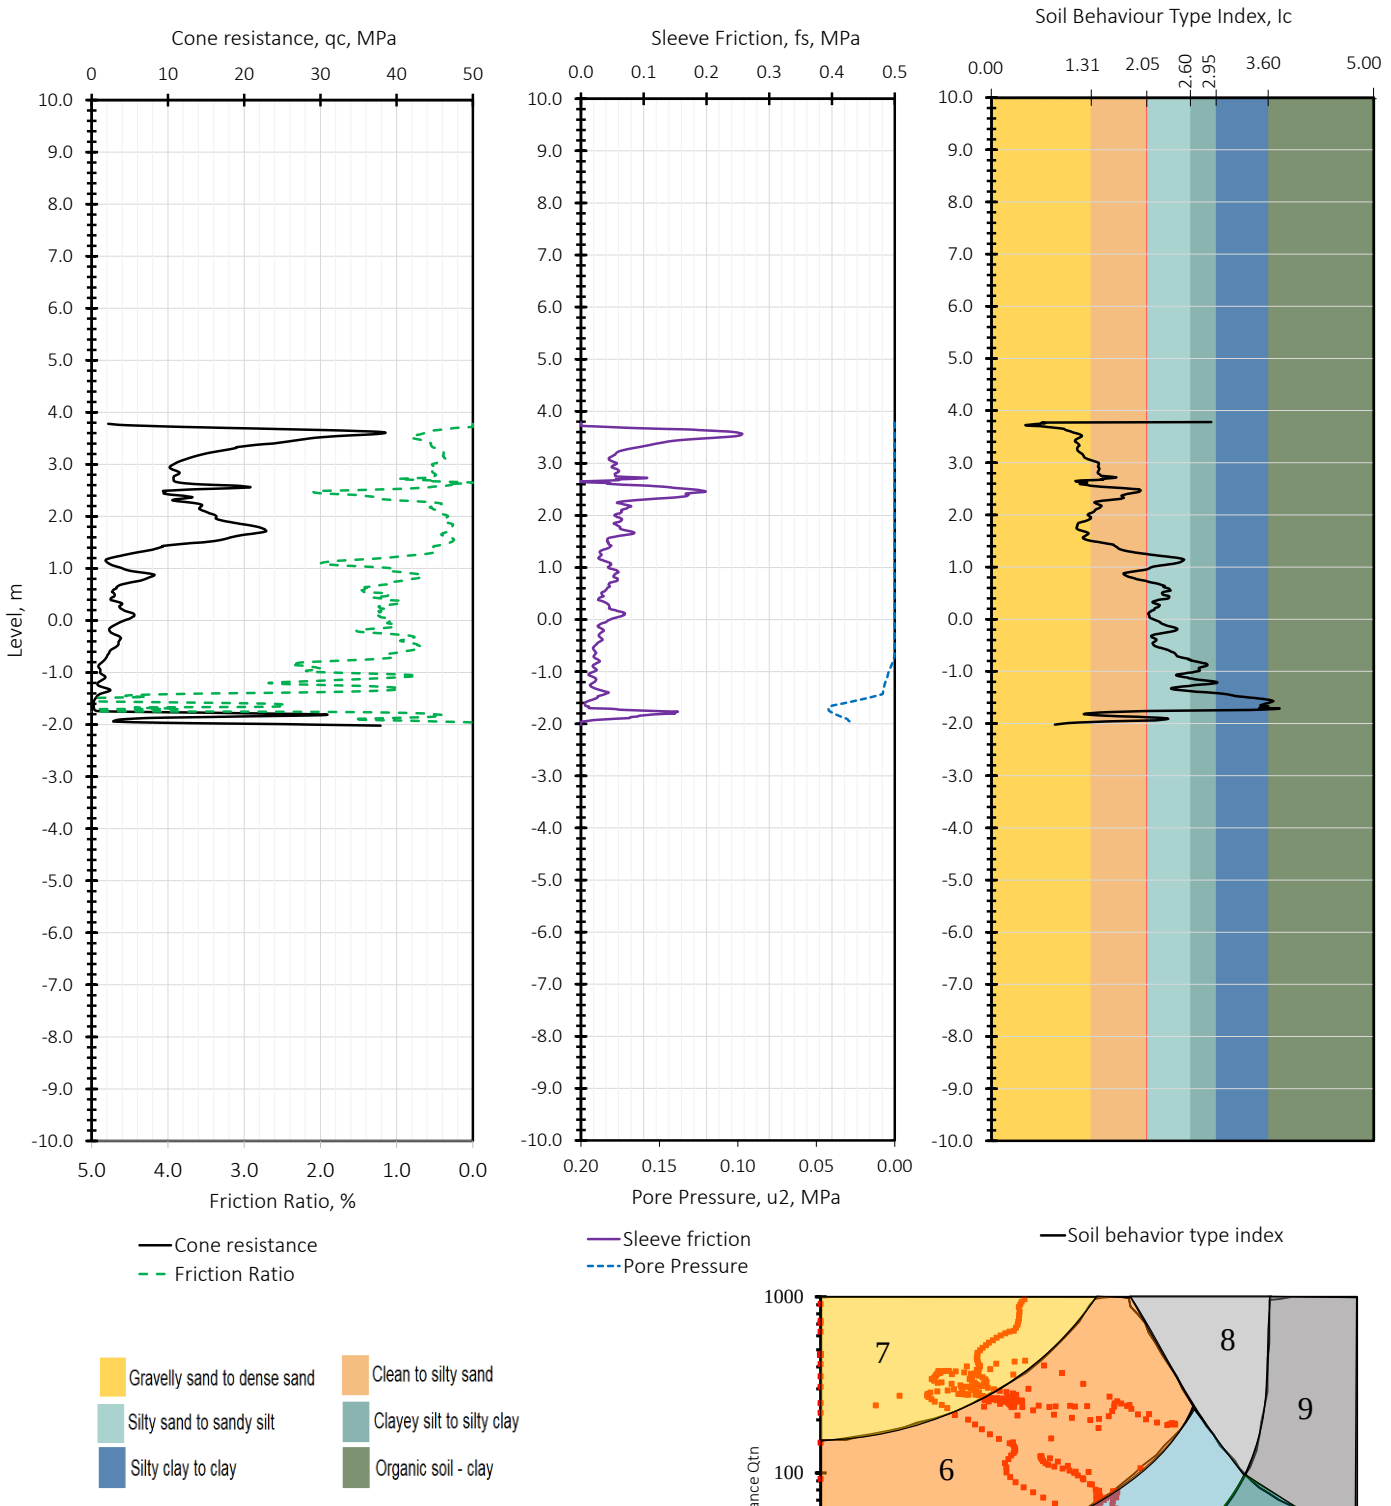

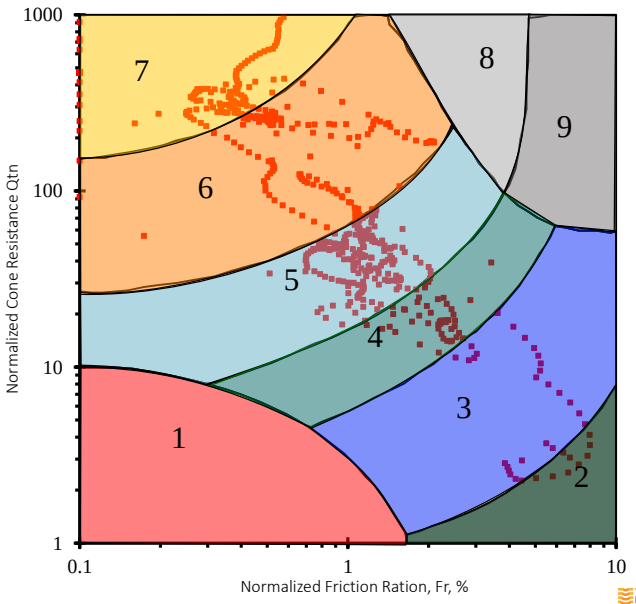

Main Contractor:	CTS GULF	
Test Location:	CPT-A2-B176-100-2	
Ground Elevation:	3.78	
	Easting	**Northing**
Coordinates:	421169.657	2927555.448
Cone ID:	DP15-CFPTxy.71431	
Test Date	14-Oct-2026	