
Client : SAUDI GLOBAL PORTS

Project : DAMMAM LOGISTICS ZONE

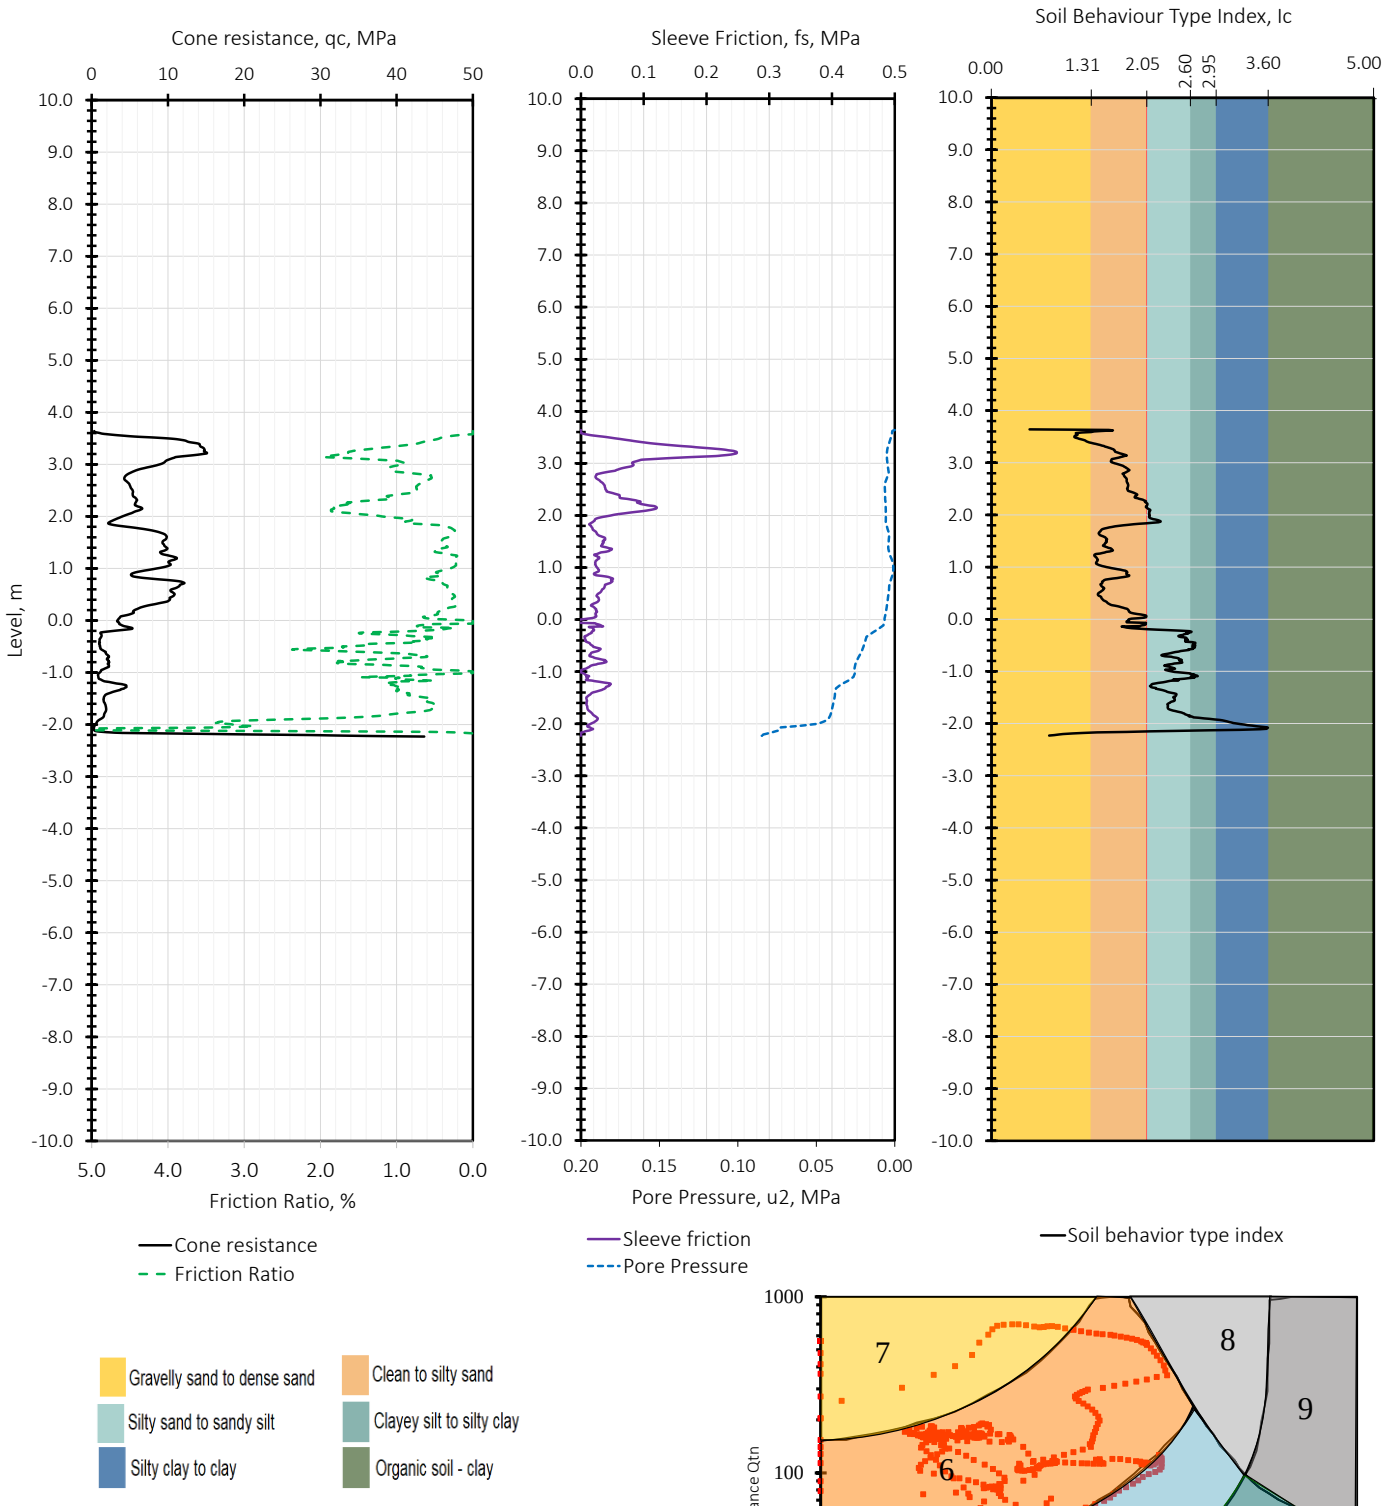

Main Contractor:	CTS GULF	
Test Location:	CPT-A2-B181-100	
Ground Elevation:	3.64	
	Easting	**Northing**
Coordinates:	421205.841	2927675.097
Cone ID:	DP15-CFPTxy.71424	
Test Date	14-Oct-2026	