

Client : SAUDI GLOBAL PORTS

Project : DAMMAM LOGISTICS ZONE

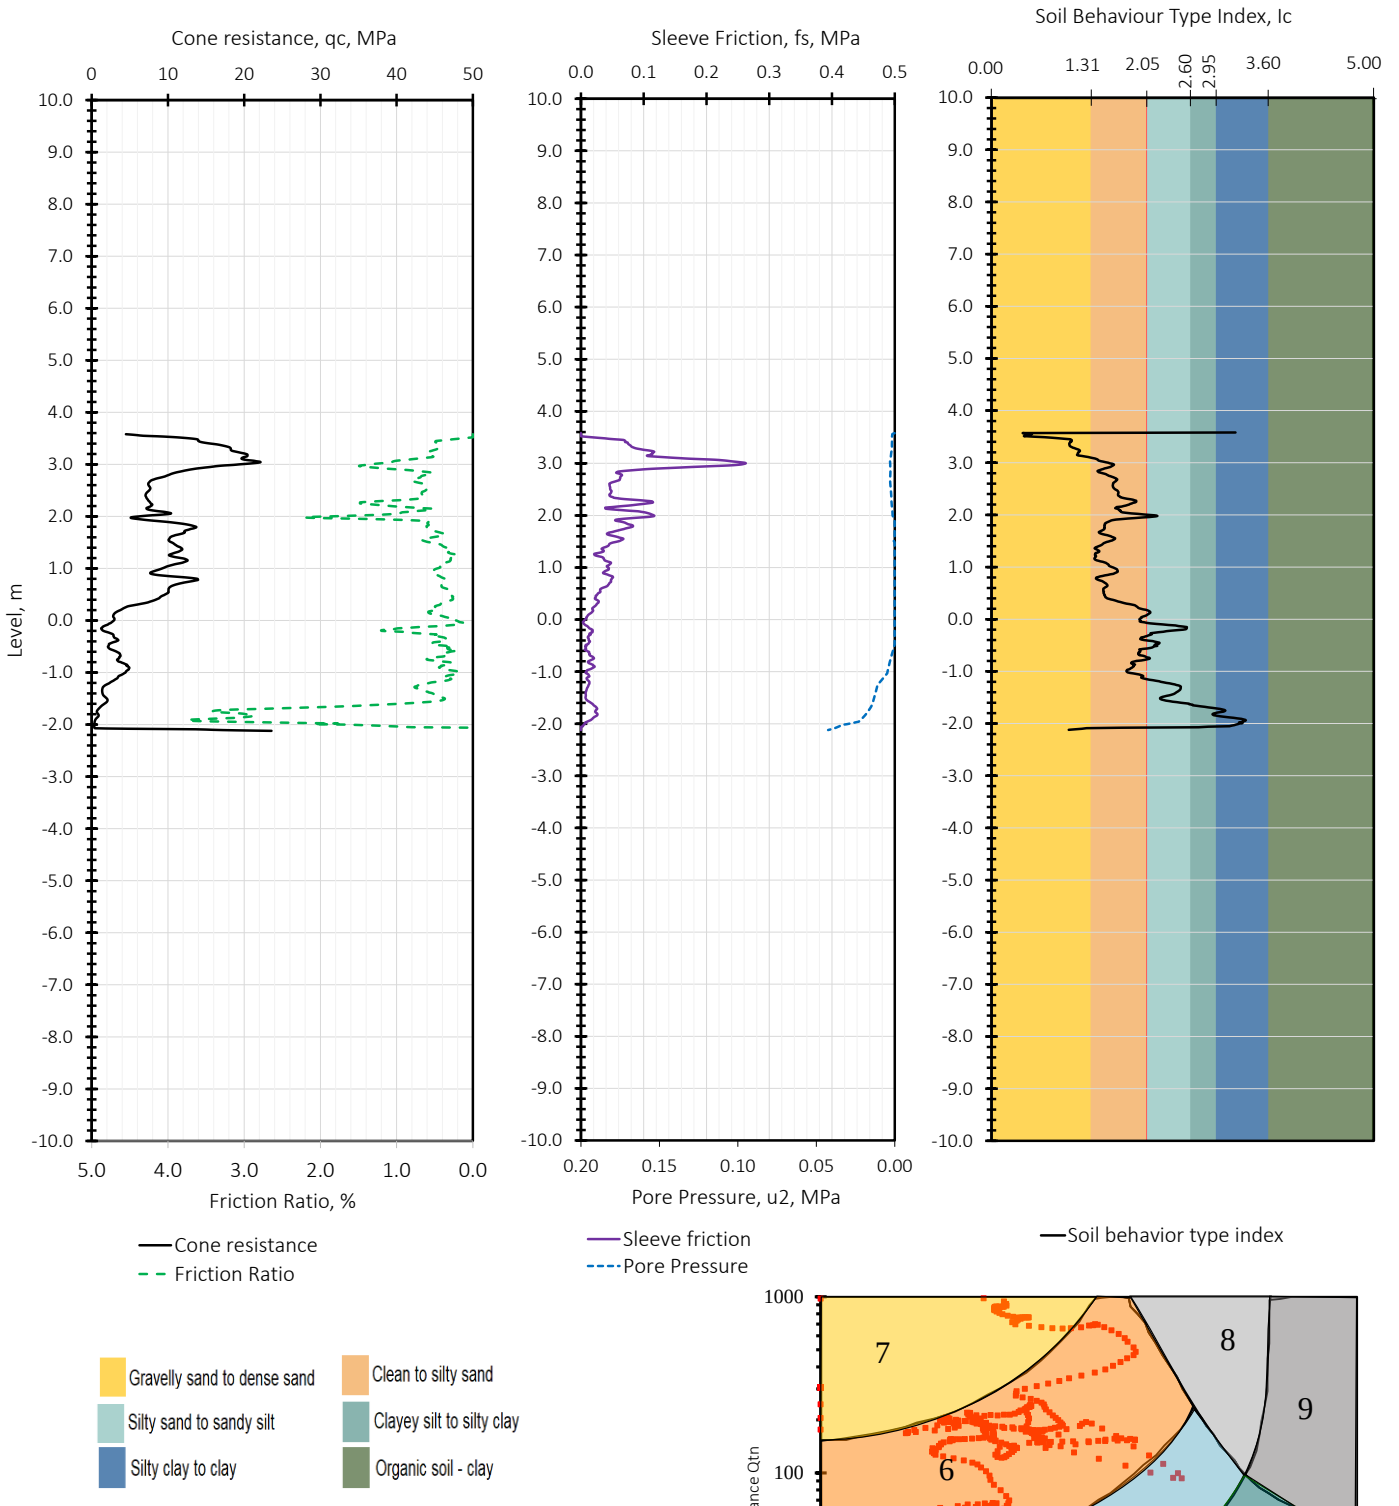

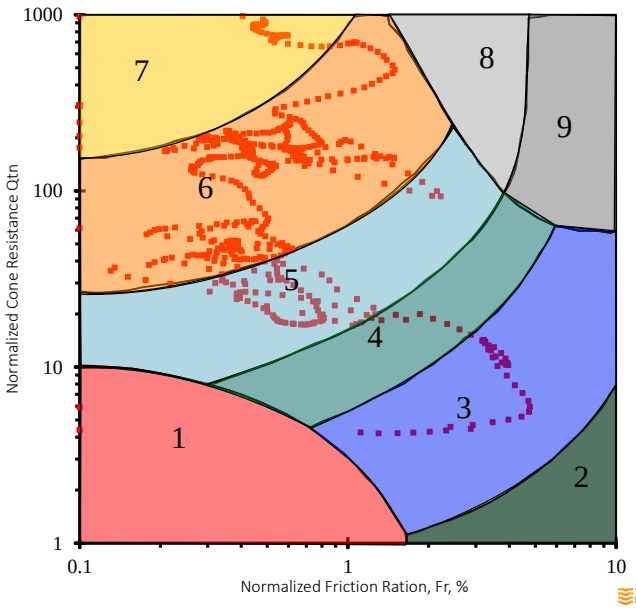

Main Contractor:	CTS GULF	
Test Location:	CPT-A2-B182-100	
Ground Elevation:	3.58	
	Easting	**Northing**
Coordinates:	421212.736	2927697.894
Cone ID:	DP15-CFPTxy.71424	
Test Date	14-Oct-2026	