

Client : SAUDI GLOBAL PORTS

Project : DAMMAM LOGISTICS ZONE

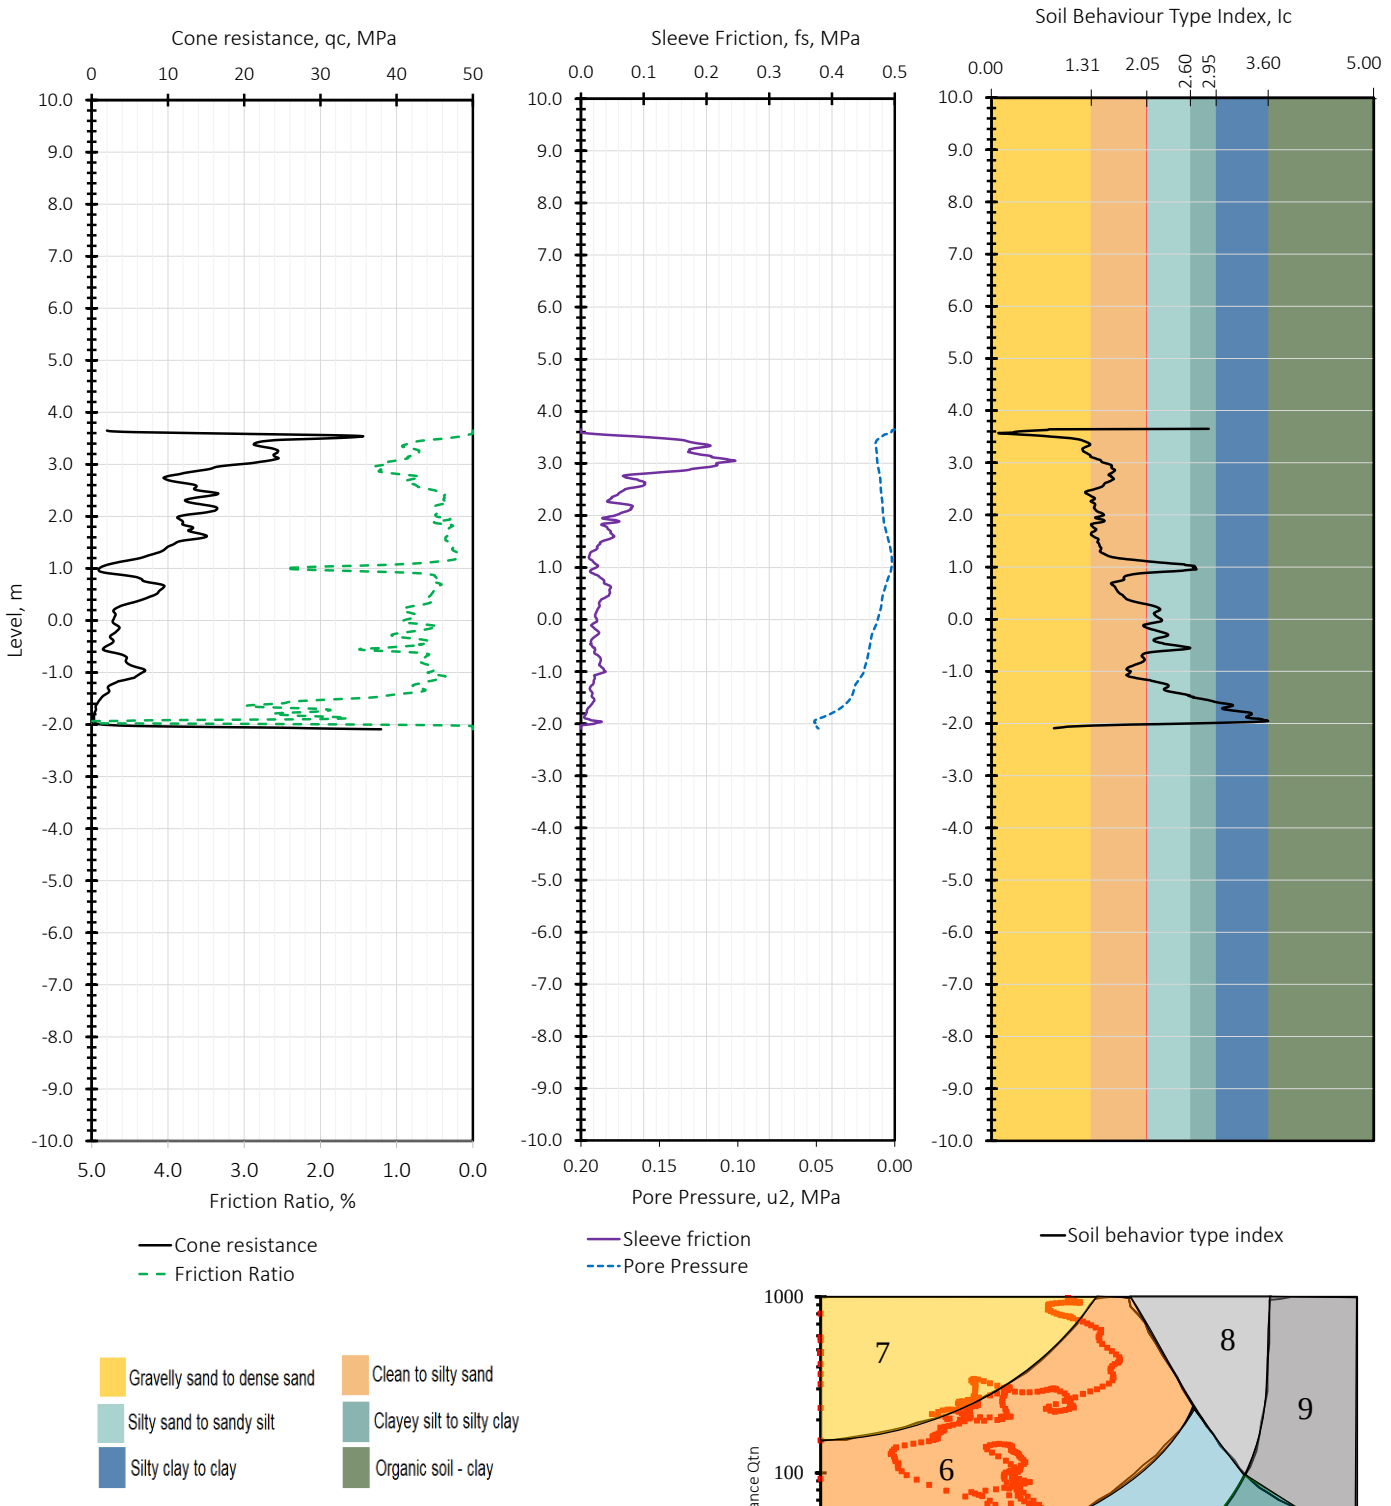

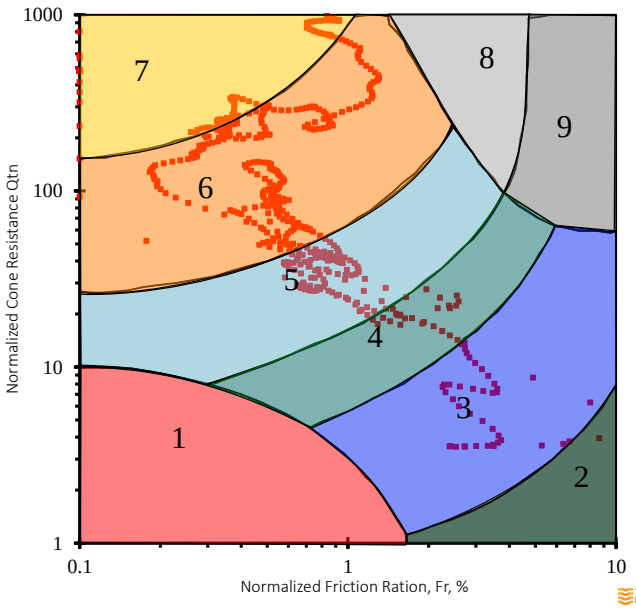

Main Contractor:	CTS GULF	
Test Location:	CPT-A2-B193-100	
Ground Elevation:	3.65	
	Easting	**Northing**
Coordinates:	421215.297	2927620
Cone ID:	DP15-CFPTxy.71424	
Test Date	14-Oct-2026	