
Client : SAUDI GLOBAL PORTS

Project : DAMMAM LOGISTICS ZONE

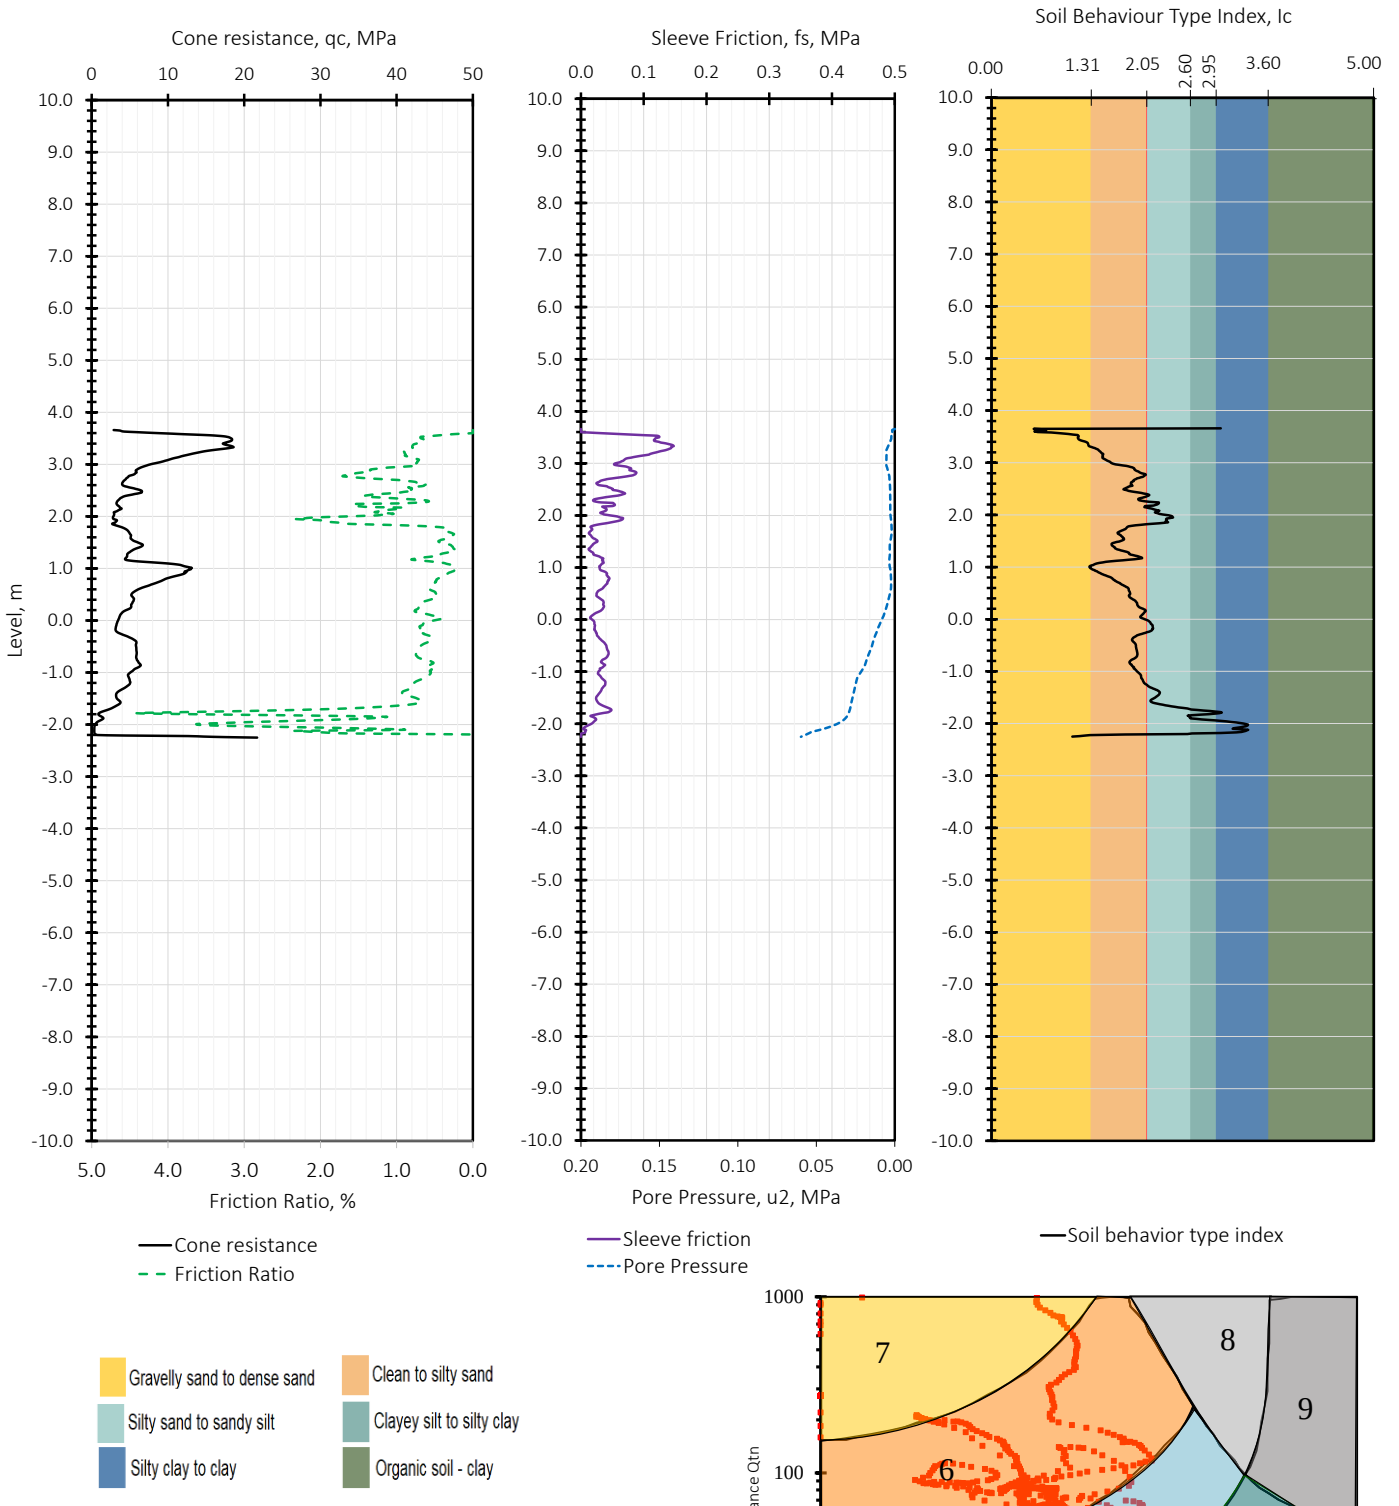

Main Contractor:	CTS GULF	
Test Location:	CPT-A2-B195-100	
Ground Elevation:	3.66	
	Easting	**Northing**
Coordinates:	421229.771	2927667.86
Cone ID:	DP15-CFPTxy.71424	
Test Date	14-Oct-2026	