
Client : SAUDI GLOBAL PORTS

Project : DAMMAM LOGISTICS ZONE

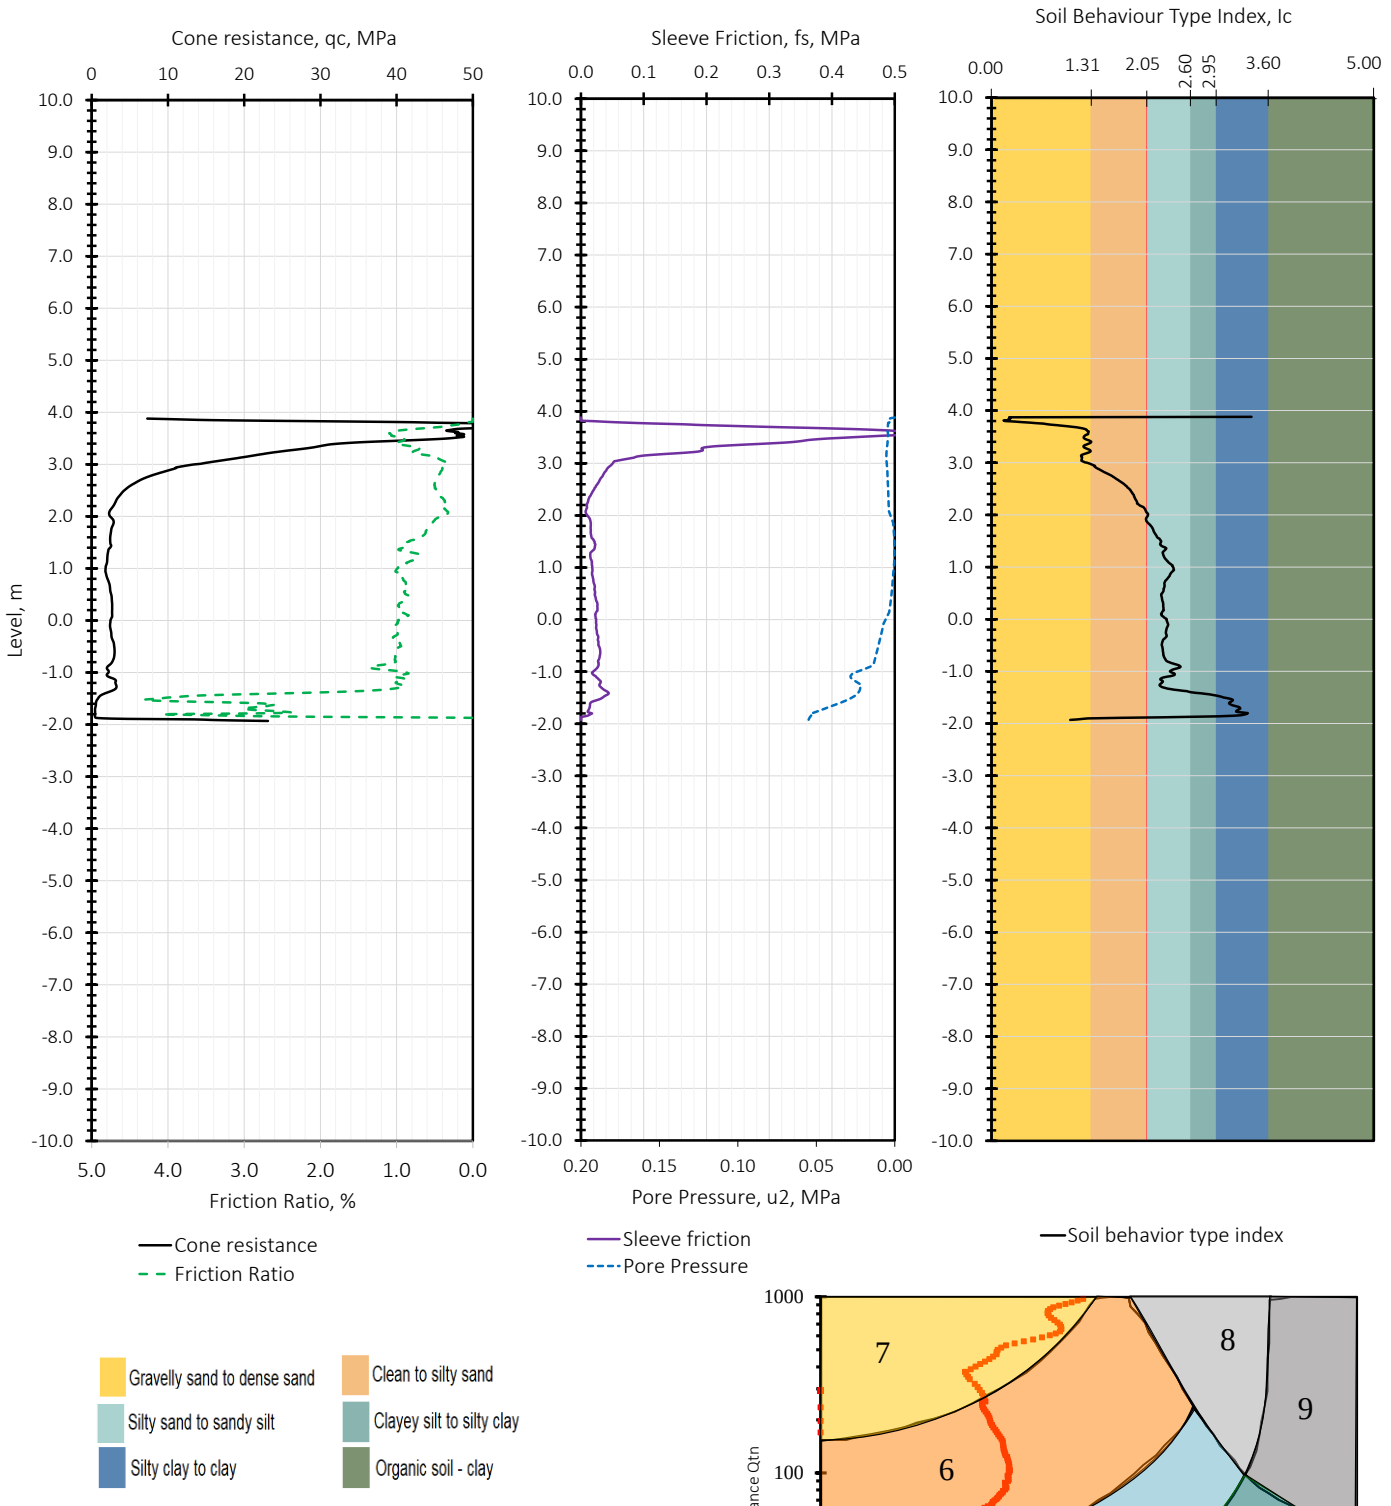

Main Contractor:	CTS GULF	
Test Location:	CPT-A2-B26-100	
Ground Elevation:	3.88	
	Easting	**Northing**
Coordinates:	420935.378	2927730.772
Cone ID:	DP15-CFPTxy.71424	
Test Date	13-Oct-2026	