
Client : SAUDI GLOBAL PORTS

Project : DAMMAM LOGISTICS ZONE

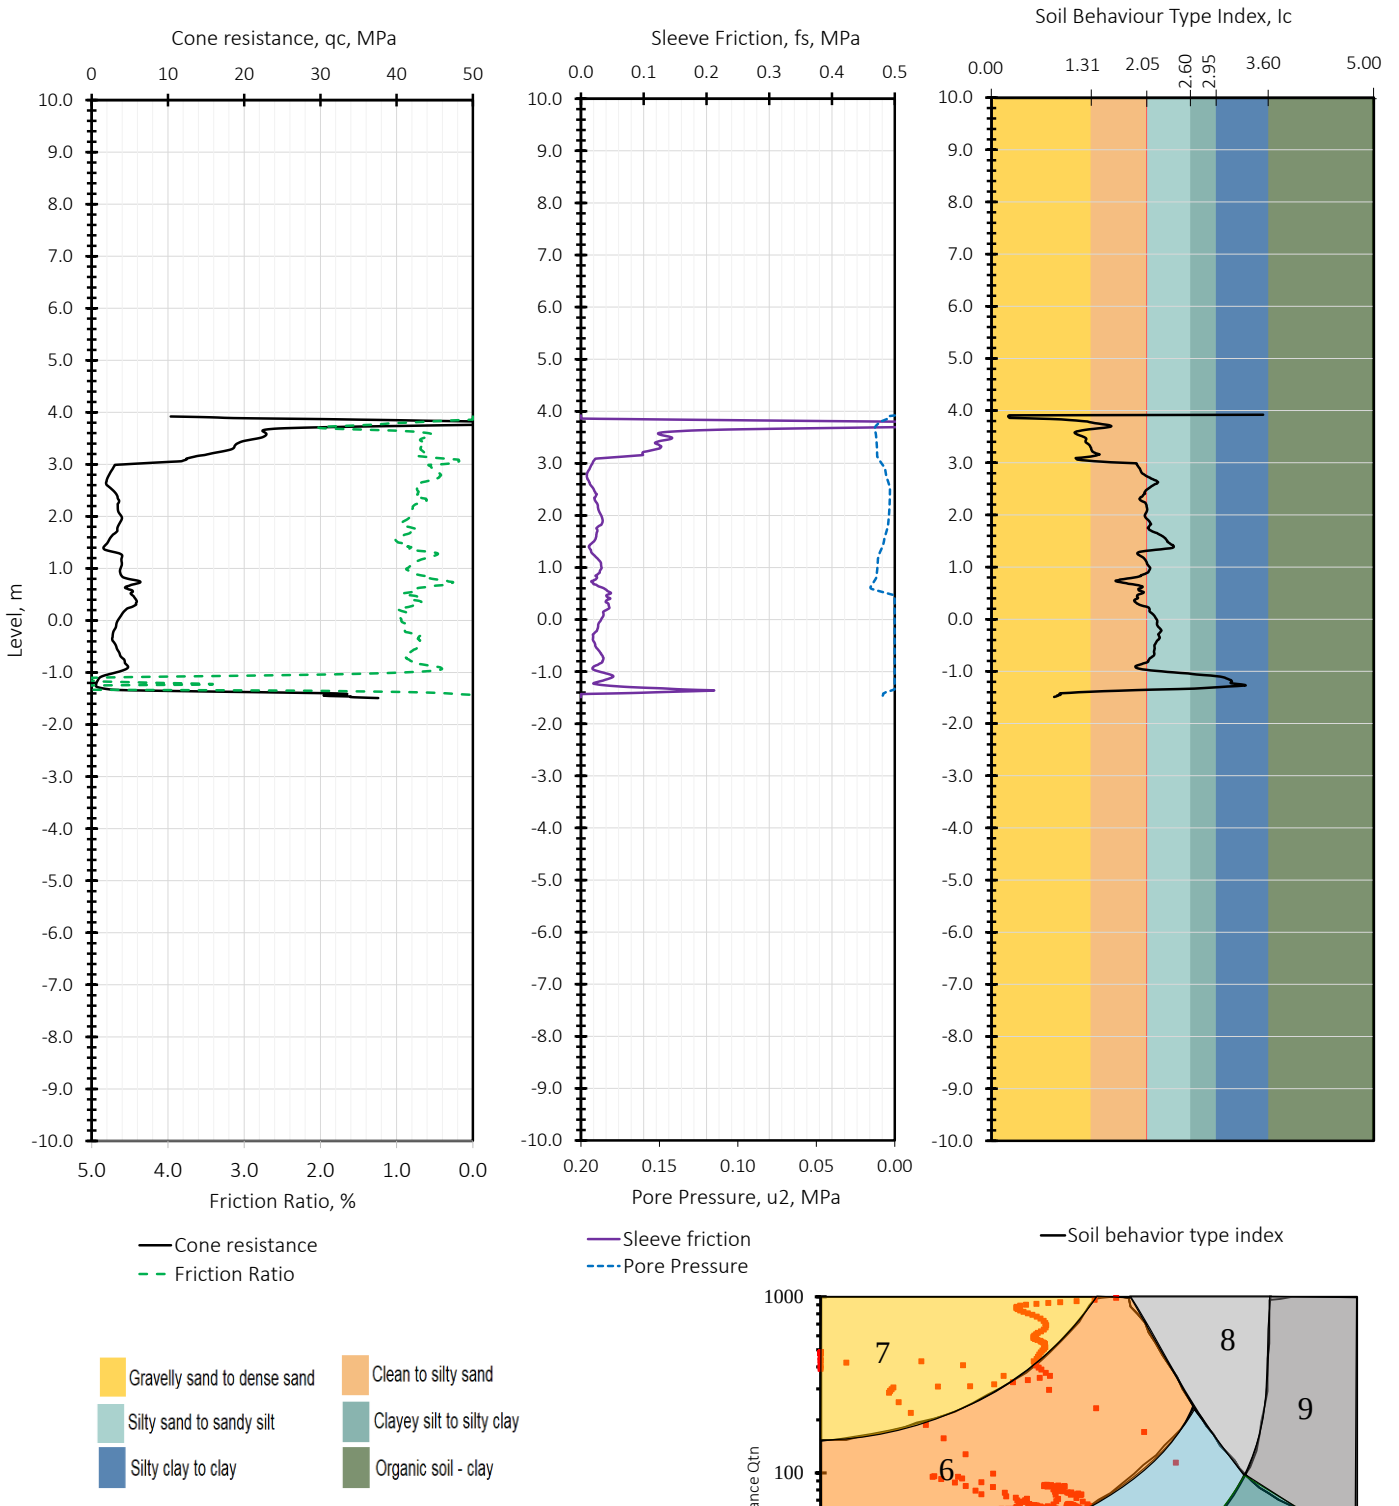

Main Contractor:	CTS GULF	
Test Location:	CPT-A2-B28-100	
Ground Elevation:	3.92	
	Easting	**Northing**
Coordinates:	420949.51	2927777.499
Cone ID:	DP15-CFPTxy.71424	
Test Date	13-Oct-2026	