
Client : SAUDI GLOBAL PORTS

Project : DAMMAM LOGISTICS ZONE

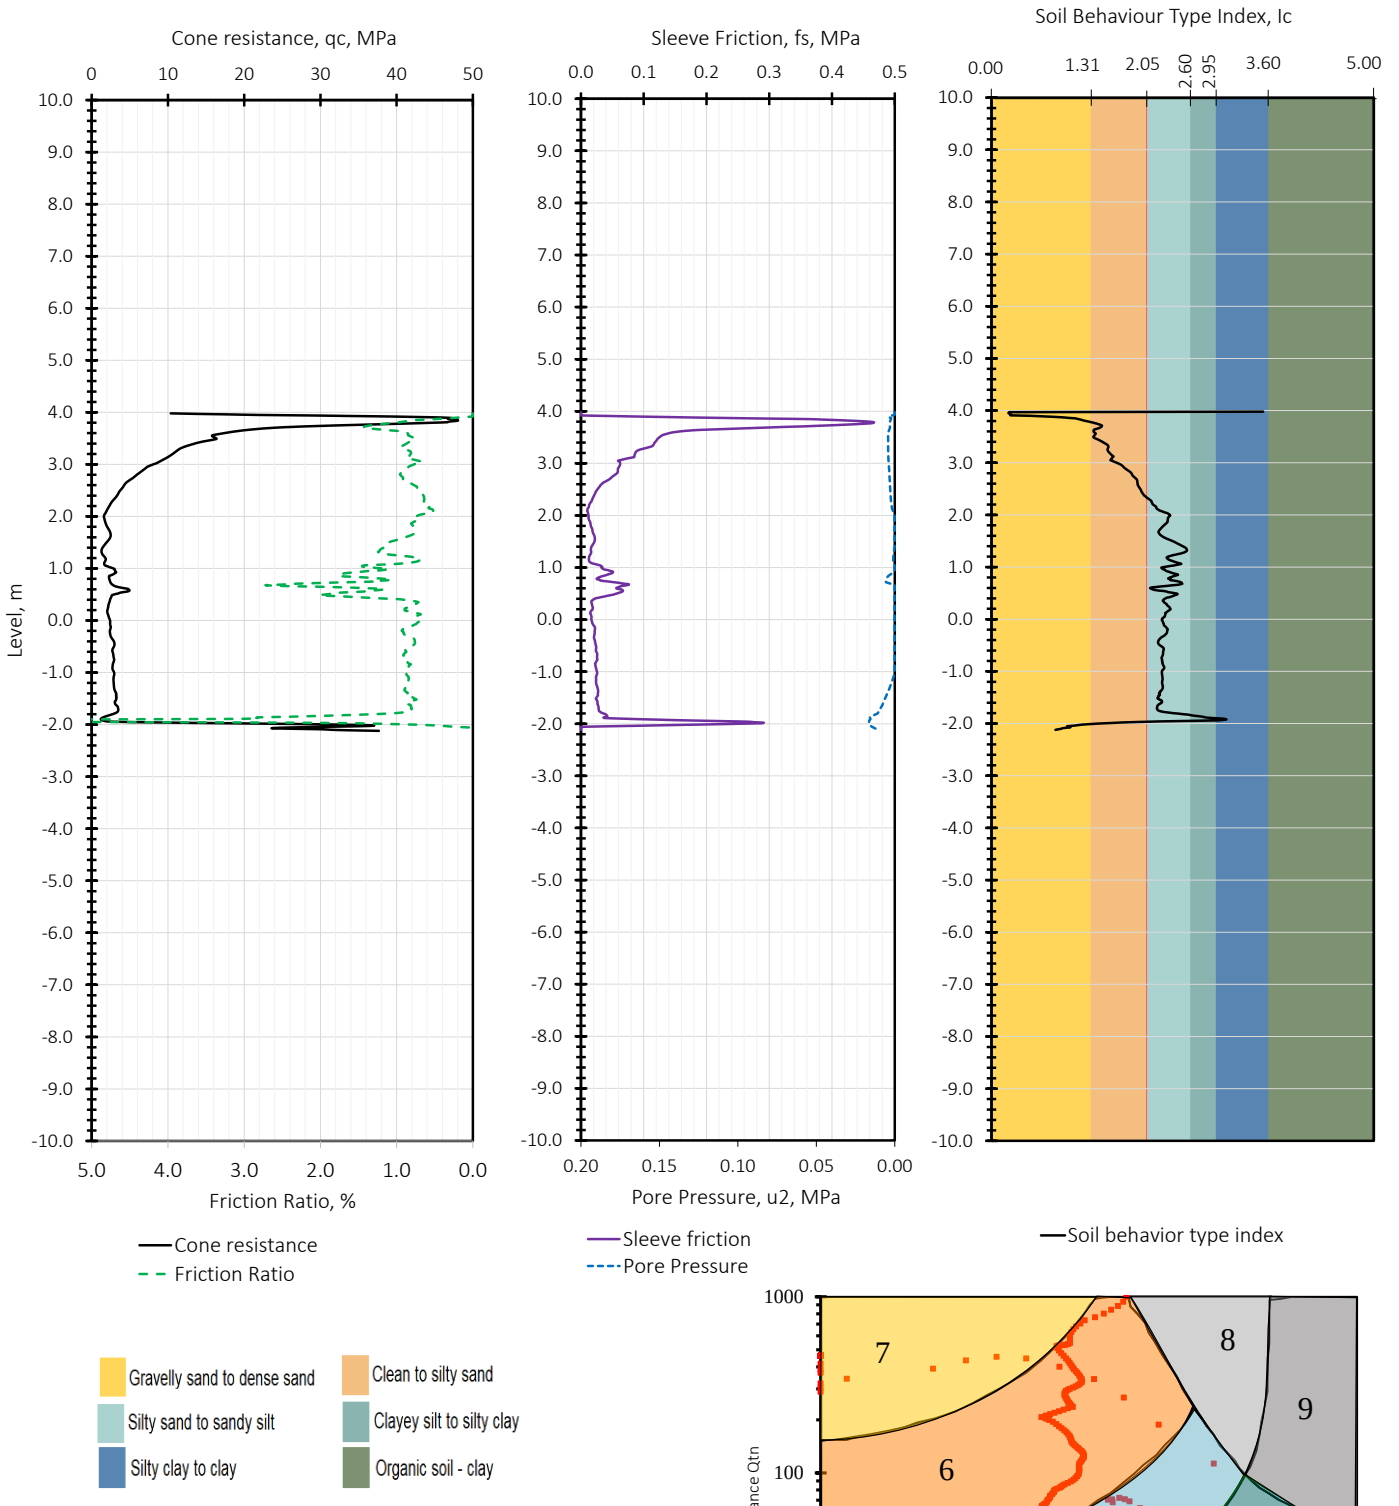

Main Contractor:	CTS GULF	
Test Location:	CPT-A2-B42-100	
Ground Elevation:	3.98	
	Easting	**Northing**
Coordinates:	420973.439	2927770.262
Cone ID:	DP15-CFPTxy.71424	
Test Date	13-Oct-2026	