
Client : SAUDI GLOBAL PORTS

Project : DAMMAM LOGISTICS ZONE

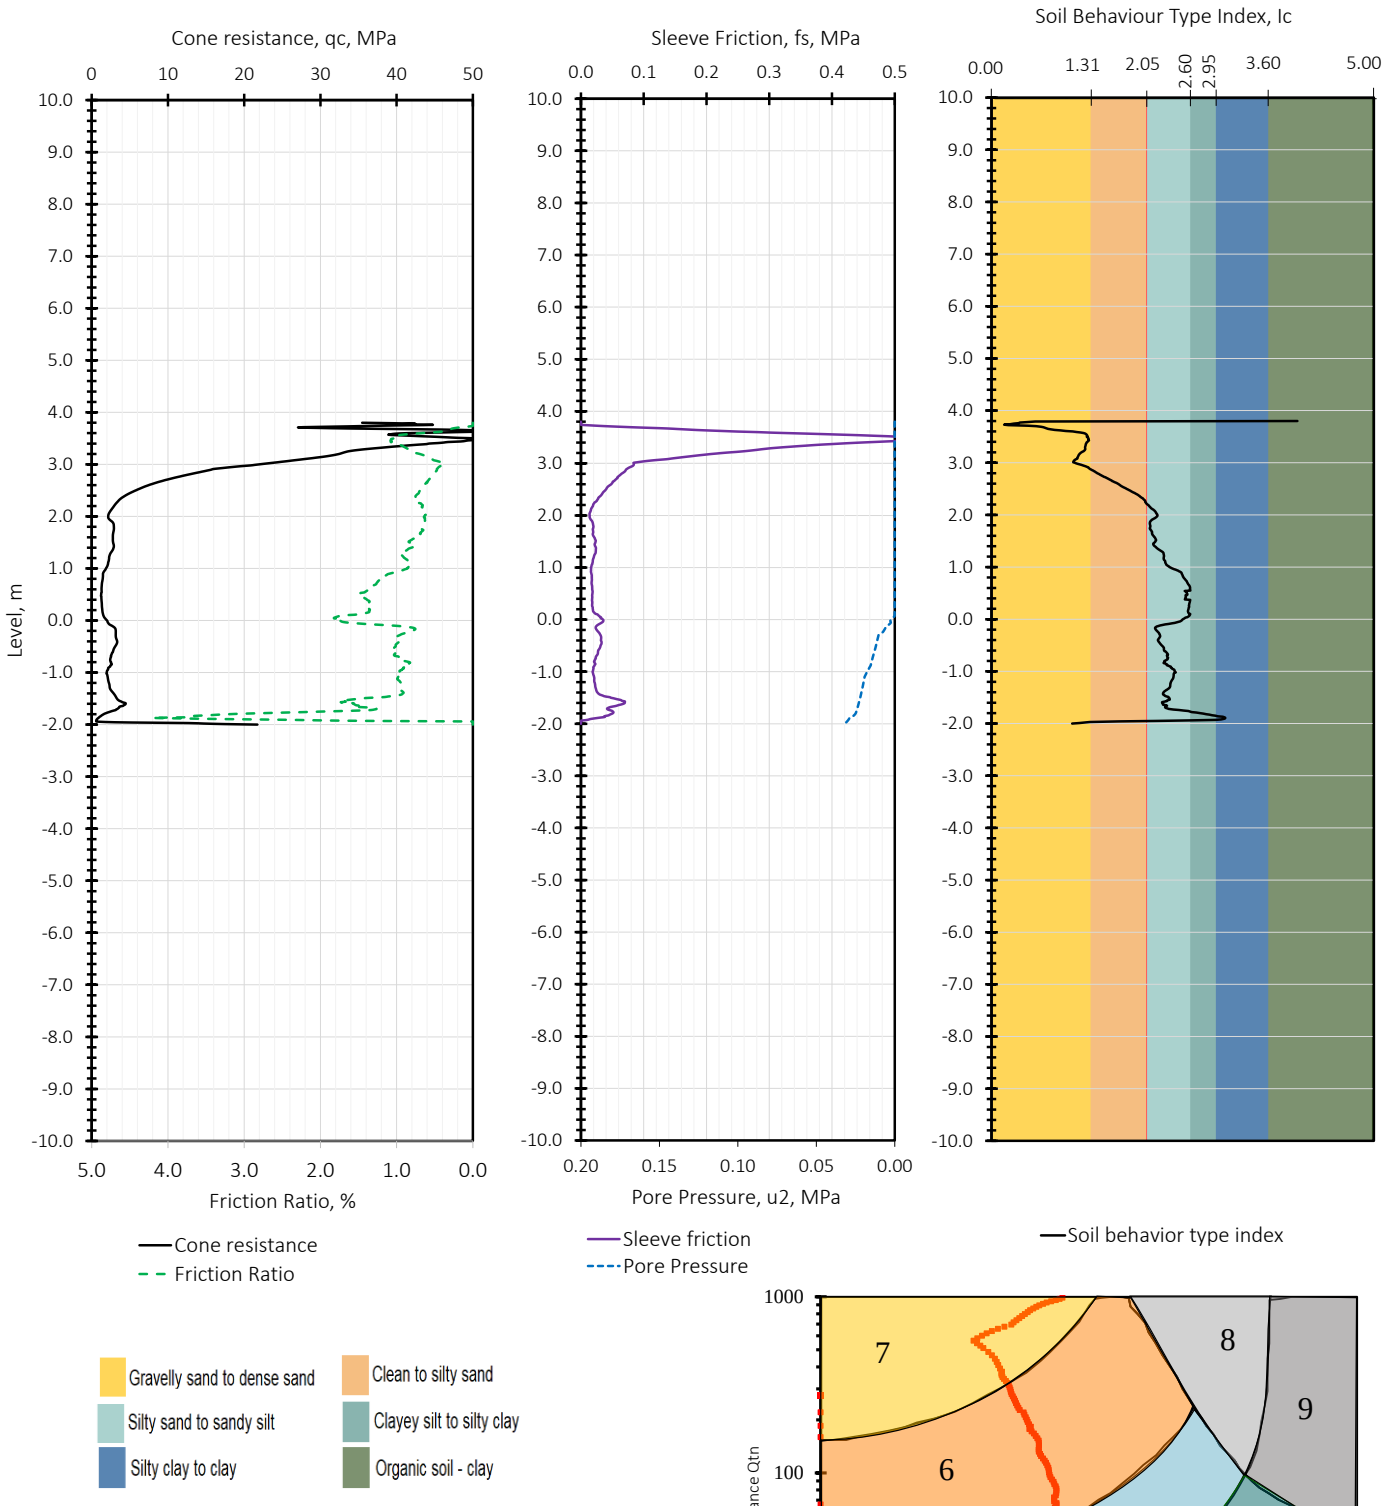

Main Contractor:	CTS GULF	
Test Location:	CPT-A2-B53-100	
Ground Elevation:	3.8	
	Easting	**Northing**
Coordinates:	420976.001	2927692.369
Cone ID:	DP15-CFPTxy.71424	
Test Date	13-Oct-2026	