
Client : SAUDI GLOBAL PORTS

Project : DAMMAM LOGISTICS ZONE

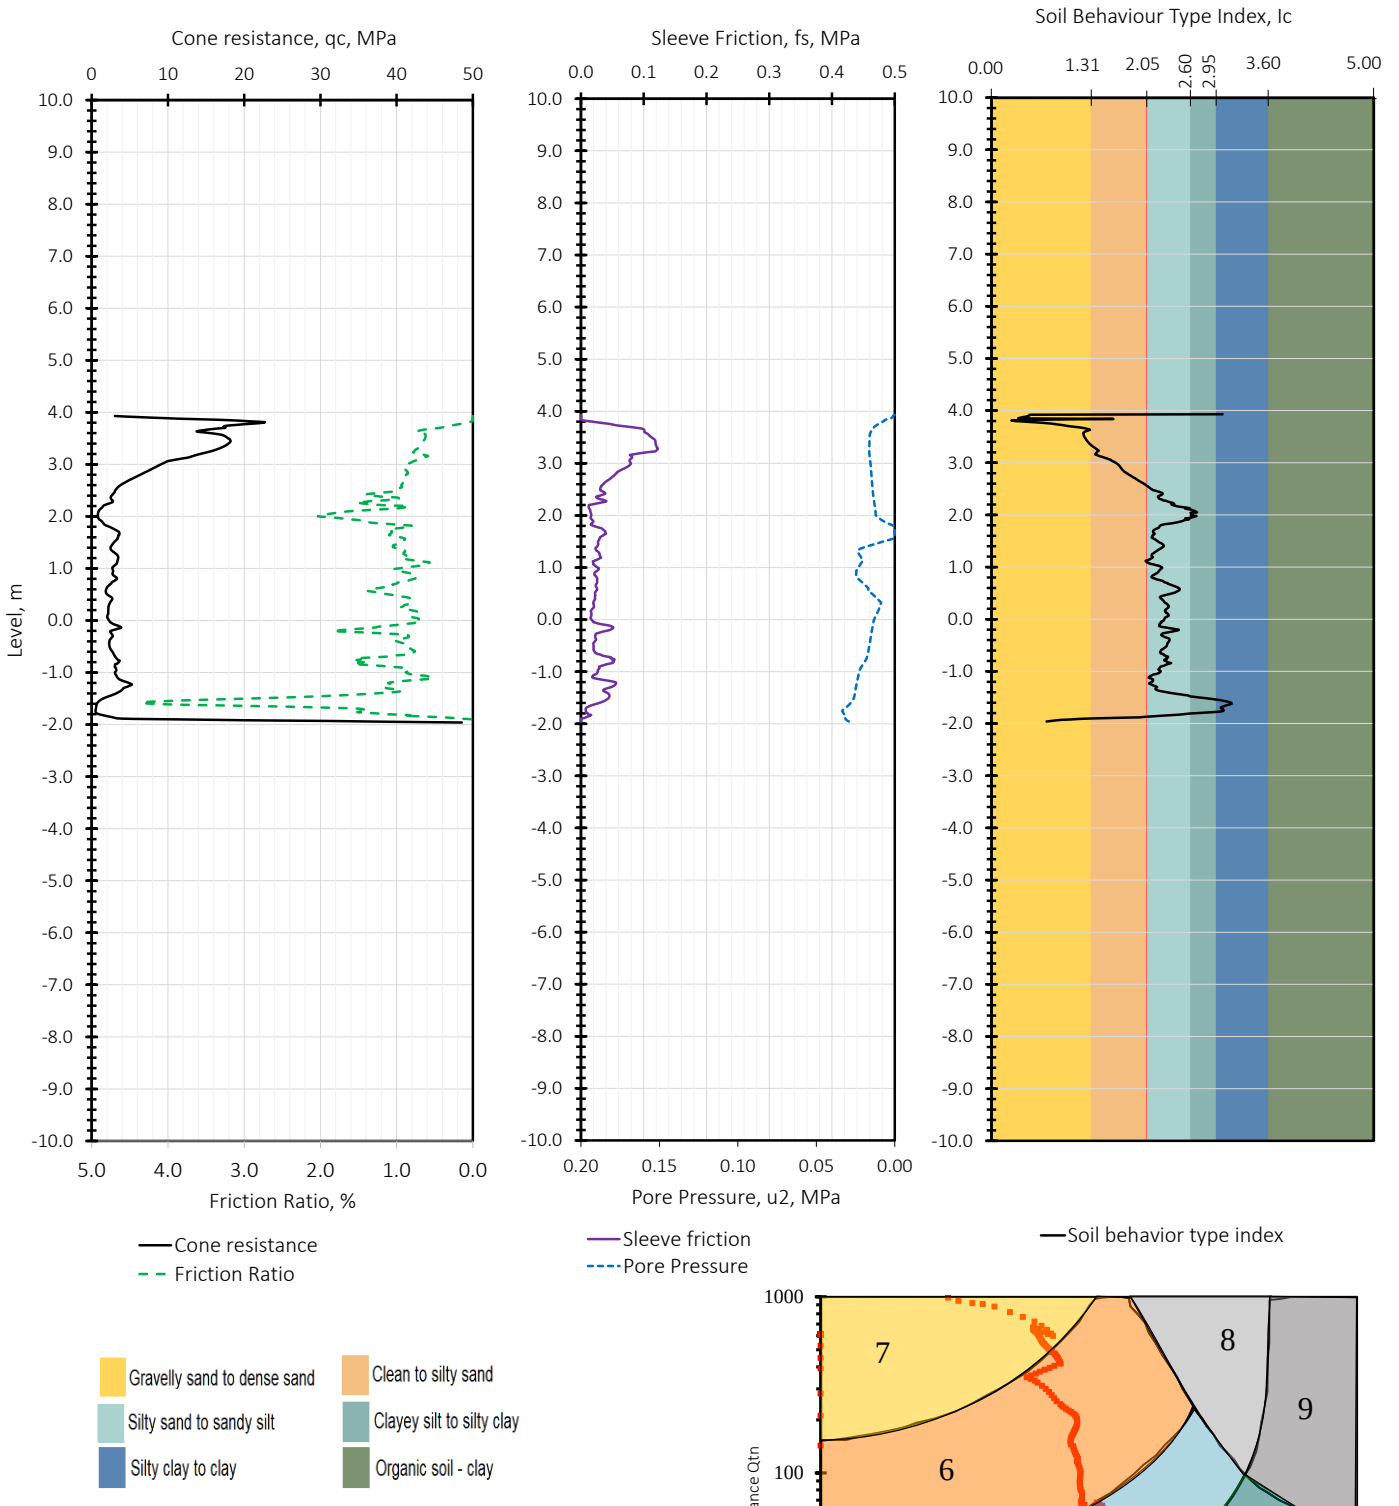

Main Contractor:	CTS GULF	
Test Location:	CPT-A2-B69-100	
Ground Elevation:	3.93	
	Easting	**Northing**
Coordinates:	421014.404	2927732.991
Cone ID:	DP15-CFPTxy.71424	
Test Date	13-Oct-2026	