
Client : SAUDI GLOBAL PORTS

Project : DAMMAM LOGISTICS ZONE

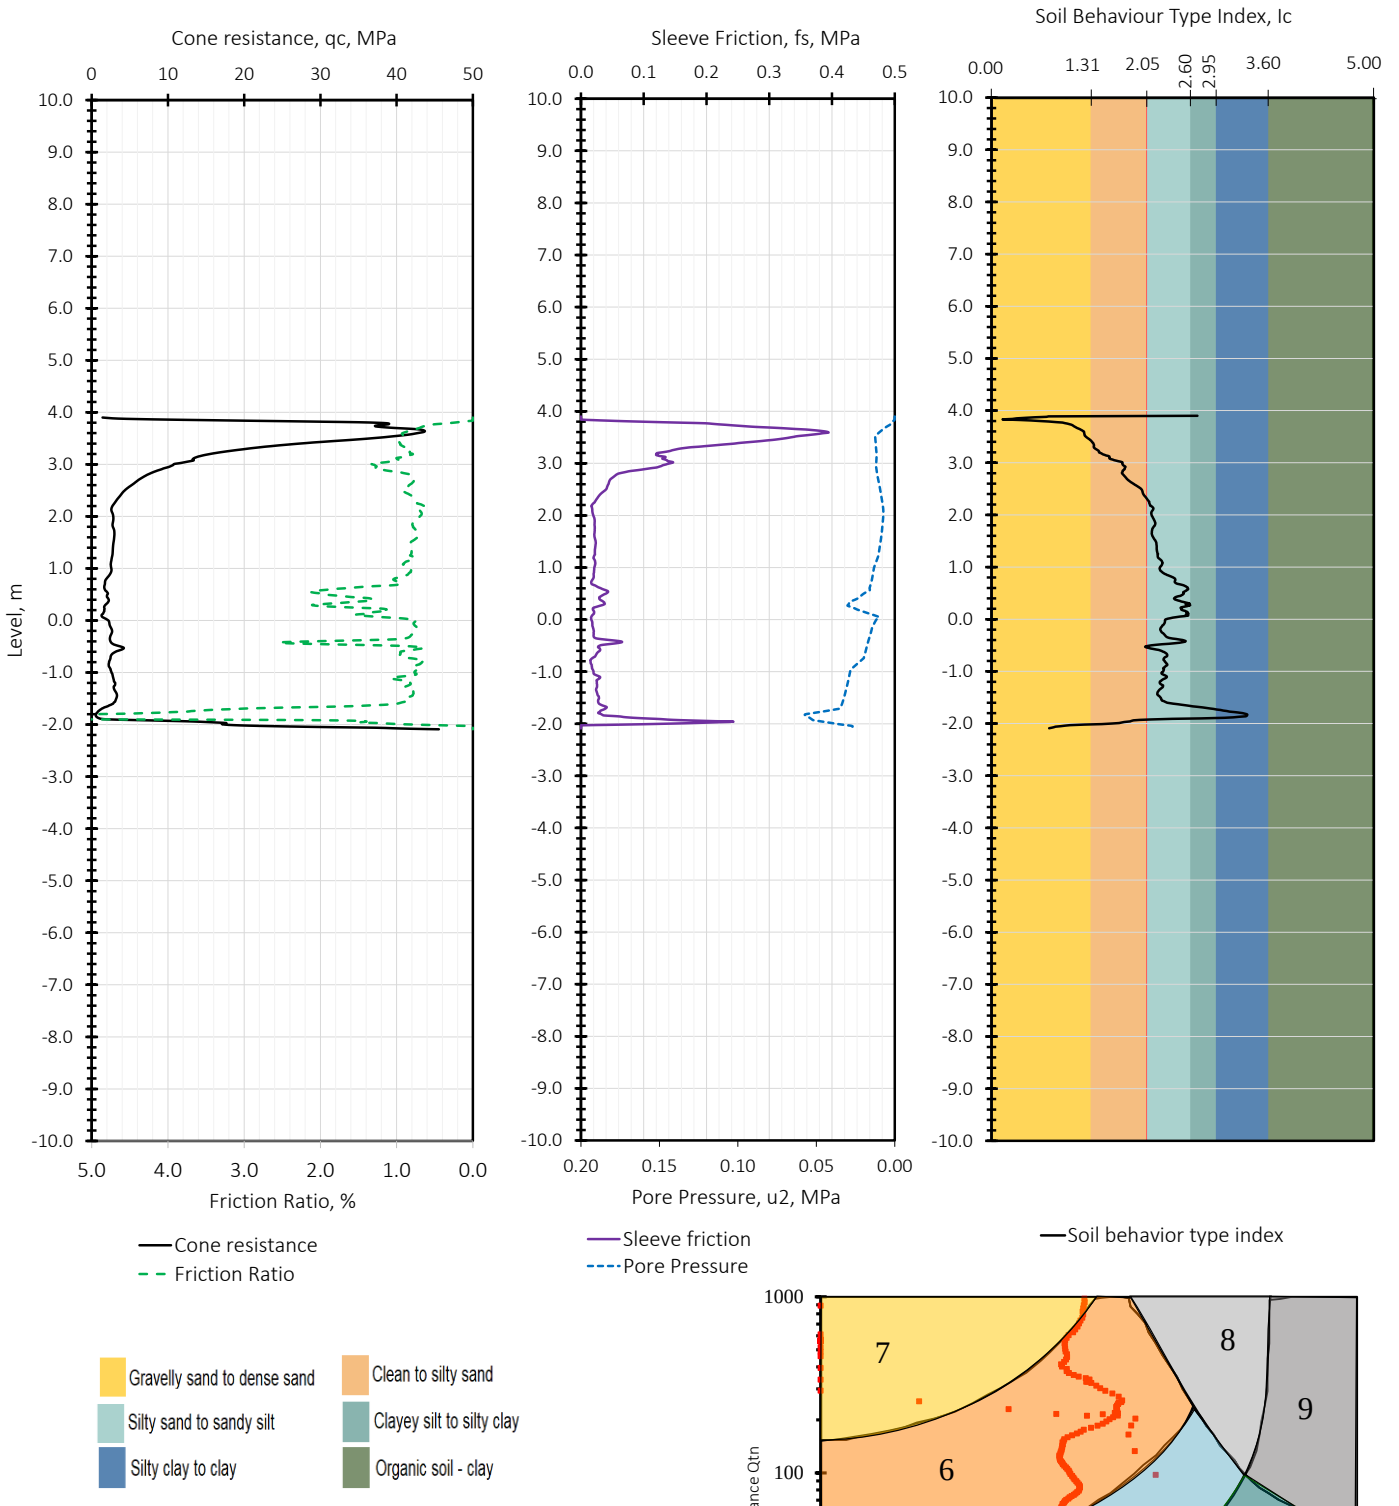

Main Contractor:	CTS GULF	
Test Location:	CPT-A2-B70-100	
Ground Elevation:	3.9	
	Easting	**Northing**
Coordinates:	421021.299	2927755.789
Cone ID:	DP15-CFPTxy.71424	
Test Date	13-Oct-2026	