
Client : SAUDI GLOBAL PORTS

Project : DAMMAM LOGISTICS ZONE

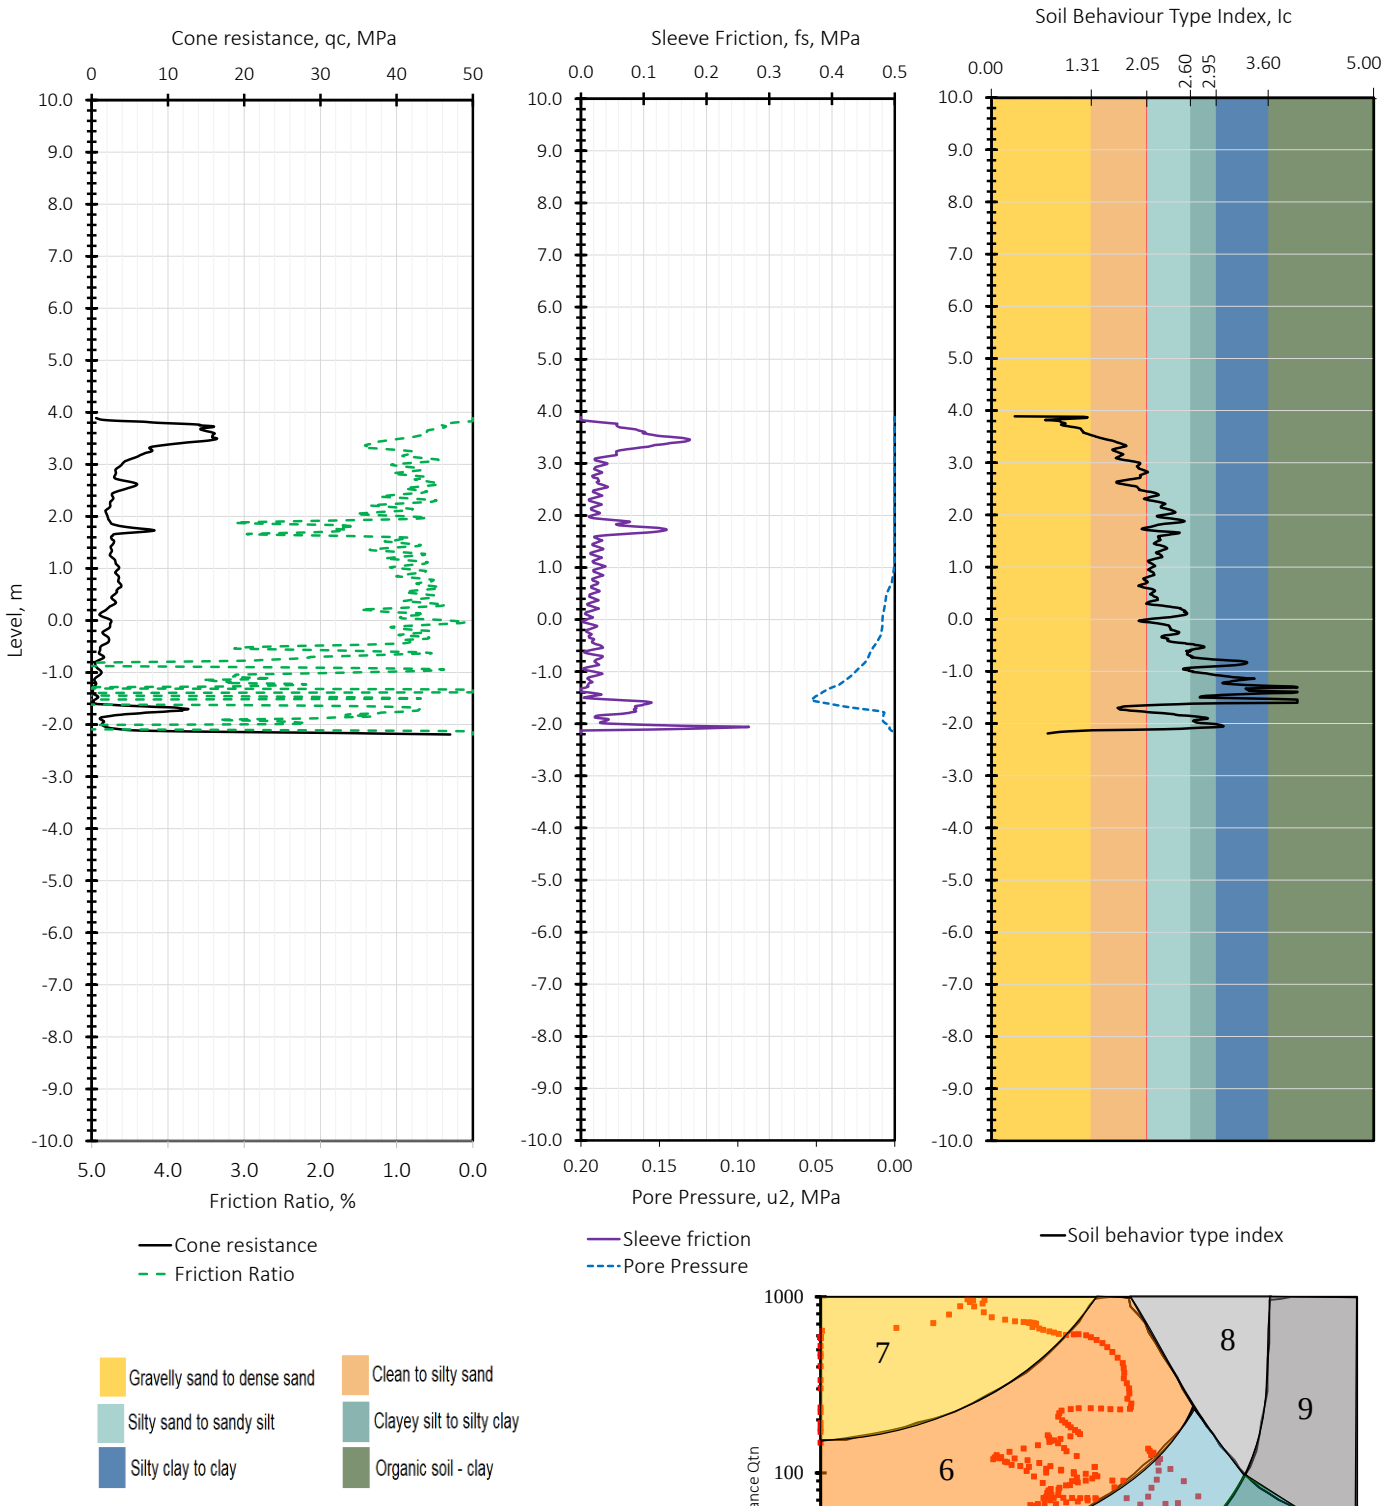

Main Contractor:	CTS GULF	
Test Location:	CPT-A2-B83-100	
Ground Elevation:	3.89	
	Easting	**Northing**
Coordinates:	421038.334	2927725.754
Cone ID:	DP15-CFPTxy.71431	
Test Date	13-Oct-2026	