
Client : SAUDI GLOBAL PORTS

Project : DAMMAM LOGISTICS ZONE

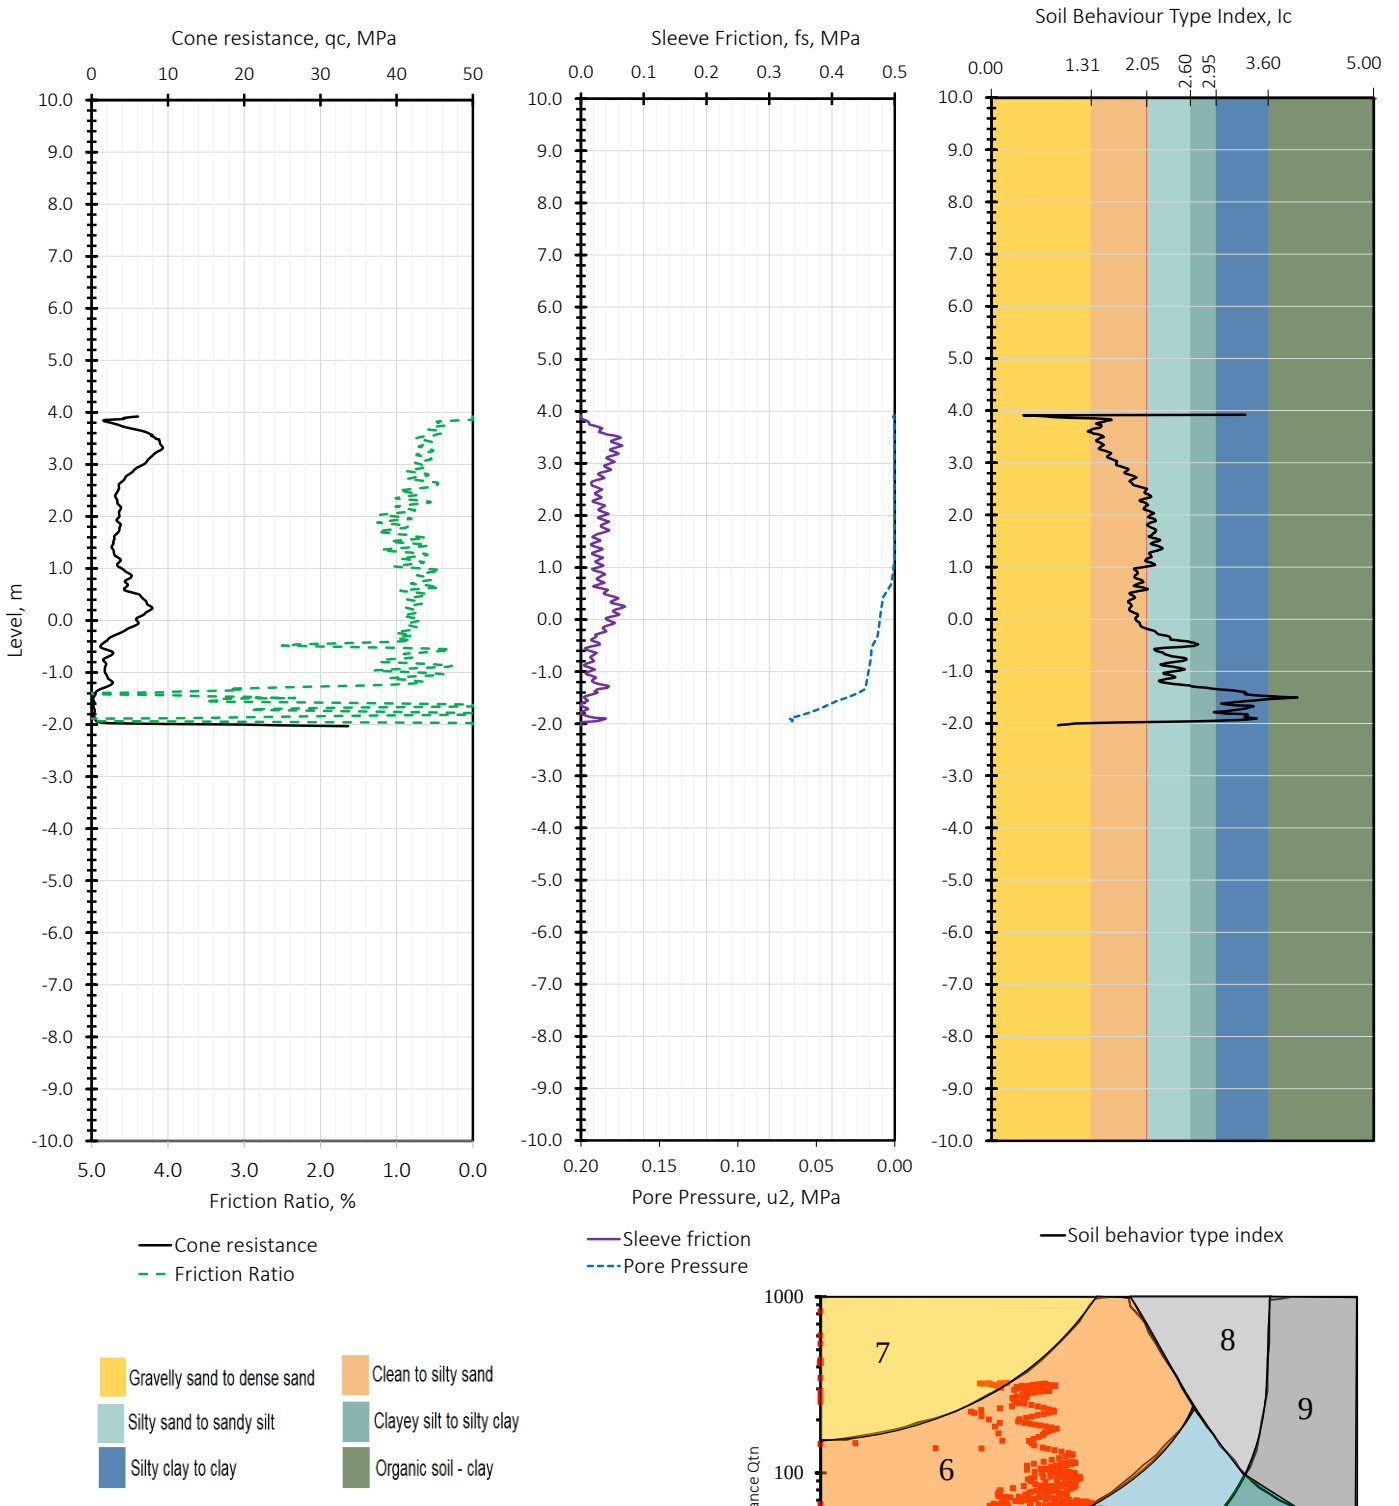

Main Contractor:	CTS GULF	
Test Location:	CPT-A2-B95-100	
Ground Elevation:	3.92	
	Easting	**Northing**
Coordinates:	421047.79	2927670.658
Cone ID:	DP15-CFPTxy.71431	
Test Date	13-Oct-2026	